
全馆建筑与动线总平面

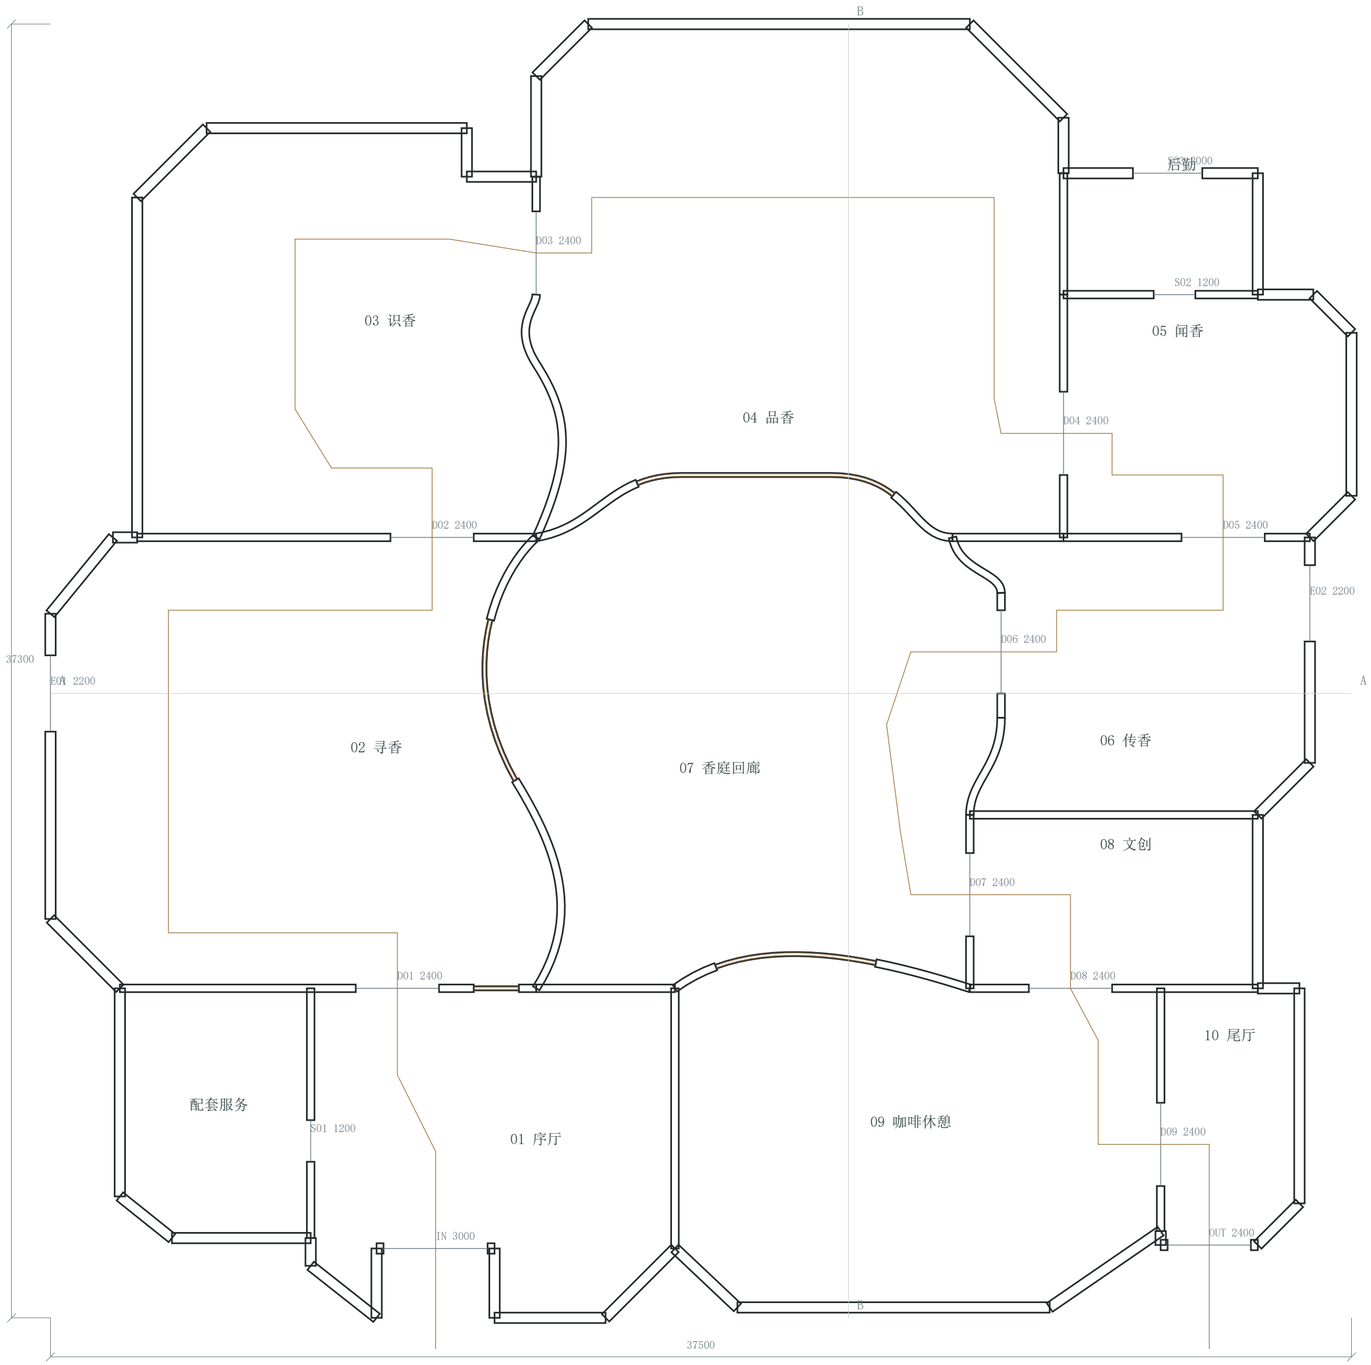

项目北

连续参观顺序

序厅 → 寻香 → 识香 → 品香 → 闻香 → 传香手作 → 香庭 → 文创 → 咖啡 → 尾厅出口

主线控制宽度：1800

外墙厚度按现有模型：300

门洞、墙线及分区沿用原布局

方向为项目坐标方向

坐标和展品明细另附CSV


各窗定位见第08张

柜台家具见第07张

四向立面见第03张

剖切位置：y=16500、x=21000

全馆陈设与展品定位平面

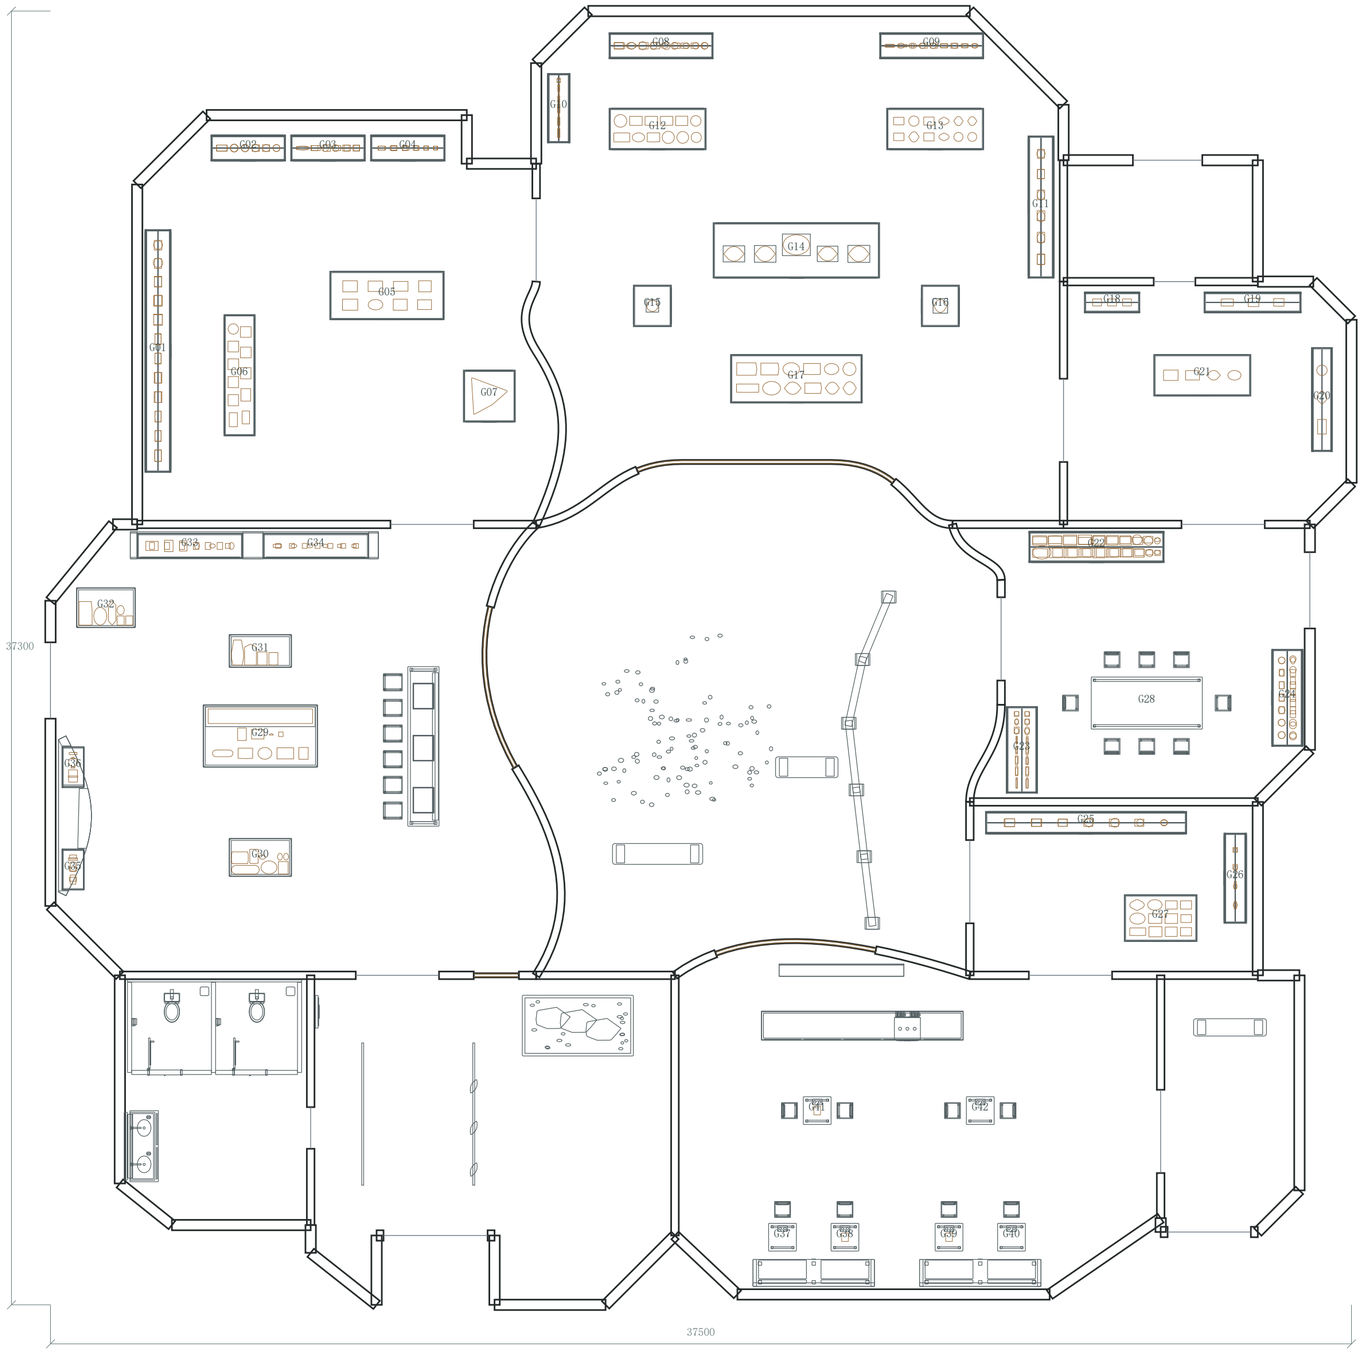

400件/组拟展品轮廓

图中棕色线为实物投影外轮廓

各展品按编号设为可编辑块

位置与编号对应附表CSV

展柜与家具编号：

G01 识香 • 西墙香材对照

G02 识香 • 北墙叶花

G03 识香 • 北墙果种

G04 识香 • 北墙结香

G05 识香 • 中央结香展台

G06 识香 • 纵向标本长柜

G07 识香 • 树体剖面

G08 品香 • 后墙香炉组

G09 品香 • 后墙香熏组

G10 品香 • 西侧香具

G11 品香 • 东侧生活用香

G12 品香 • 后左低柜

G13 品香 • 后右低柜

G14 品香 • 中央主展台

G15 品香 • 左侧重点台

G16 品香 • 右侧重点台

G17 品香 • 前排用香器具

G18 闻香 • 后左样品柜

G19 闻香 • 后右器具柜

G20 闻香 • 右侧对照柜

G21 闻香 • 中央体验台

G22 传香 • 后墙工序工具

G23 传香 • 西侧学习成果

G24 传香 • 东侧材料样品

G25 文创 • 后墙香礼

G26 文创 • 东侧工艺品

G27 文创 • 中央香礼岛

G28 八席手作桌

G29 寻香 • M • 香市重点主台

G30 寻香 • S1 • 香农与货包

G31 寻香 • S2 • 陆路运输

G32 寻香 • S3 • 水运与码头

G33 寻香 • W1 • 主墙·香市

G34 寻香 • W2 • 主墙·运输贸易

G35 寻香 • N1 • 弧墙前龛

G36 寻香 • N2 • 弧墙后龛

G37 咖啡卡座桌 • 1

G38 咖啡卡座桌 • 2


G39 咖啡卡座桌 • 3

G40 咖啡卡座桌 • 4


G41 咖啡独立桌 • 1

G42 咖啡独立桌 • 2


四向外立面

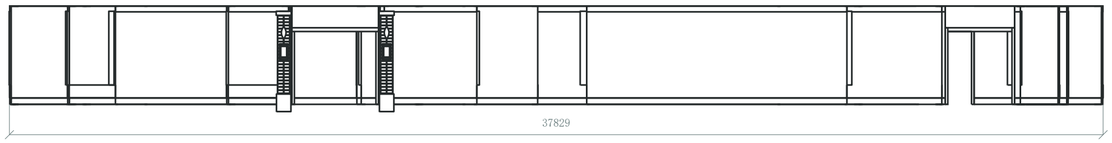

南向外立面

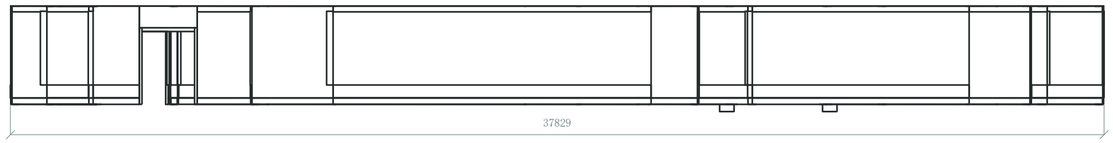

北向外立面

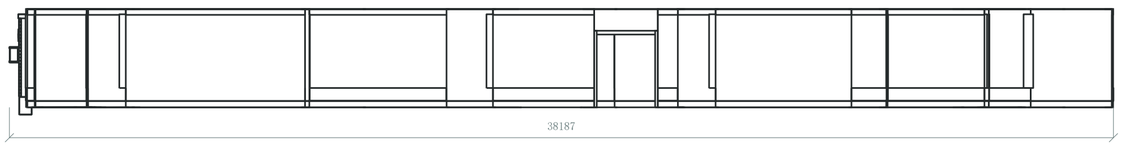

东向外立面



西向外立面

外立面取自现模型外墙、门窗及入口木作投影。全馆去顶；不补画已取消的屋面。


全馆两向剖切图

剖切图按现有模型几何提取。

层间、展具和装饰以模型高度为准。


±0.000 为项目室内地坪基准。

底板与装配核对见第13张。

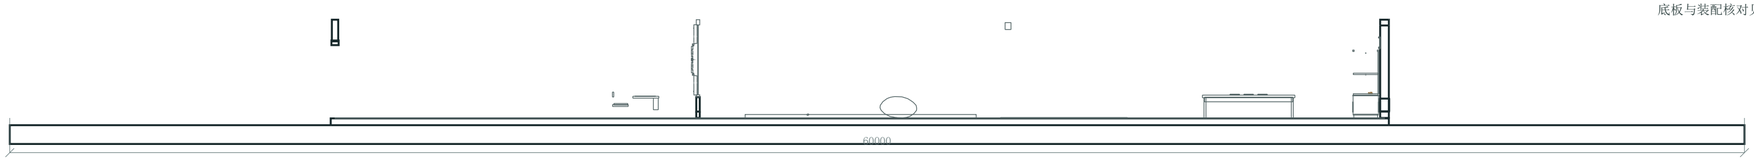

A—A 横剖面 / y=16500


粗线为真实模型与剖切平面相交轮廓

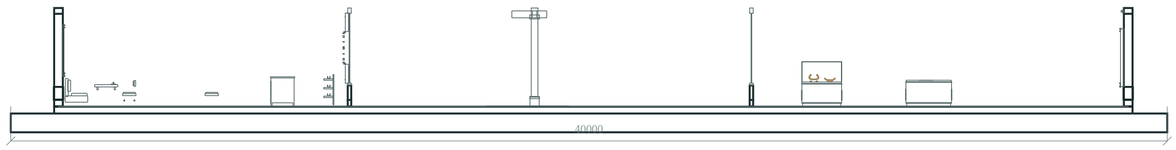

B—B 纵剖面 / x=21000

粗线为真实模型与剖切平面相交轮廓

寻香厅陈设与花窗定位详图

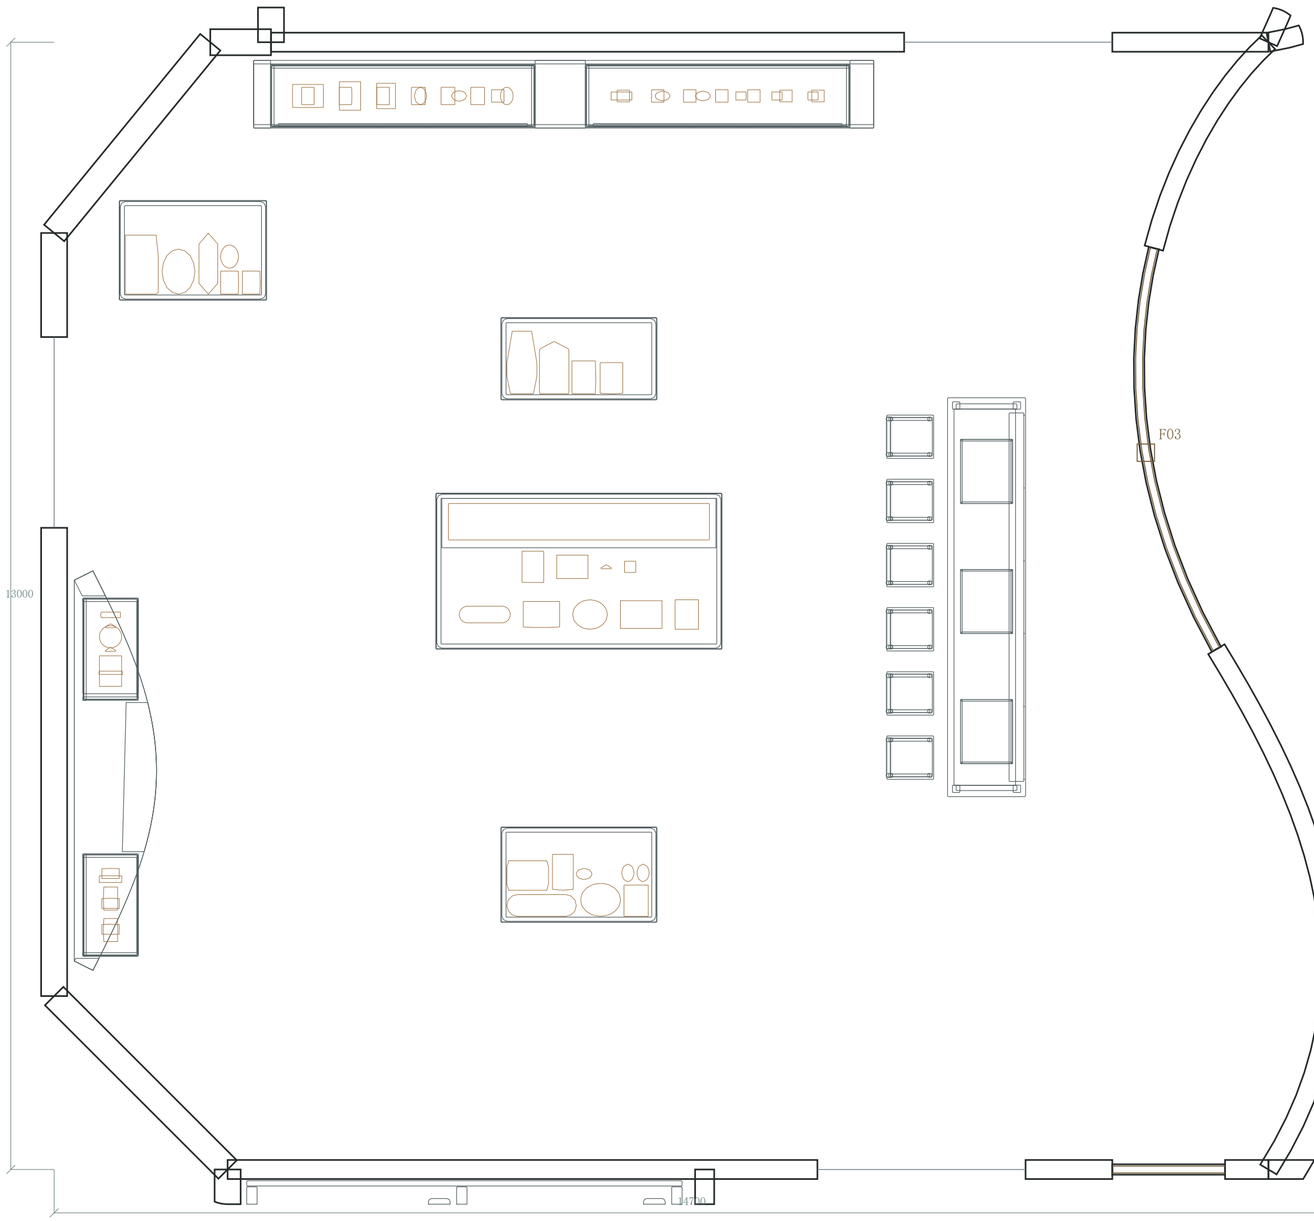

寻香厅

沿用弧墙、整合墙柜与六席长台

中央展台与物件位置保持

F03 菱花竹叶窗：1332×1332

窗中心标高：2020


图纸09—12为展开正面详图

主台：香市与地方记忆


沿墙：香农、运输与交易

六席：互动教学与手作示范

手作与咖啡家具布置详图

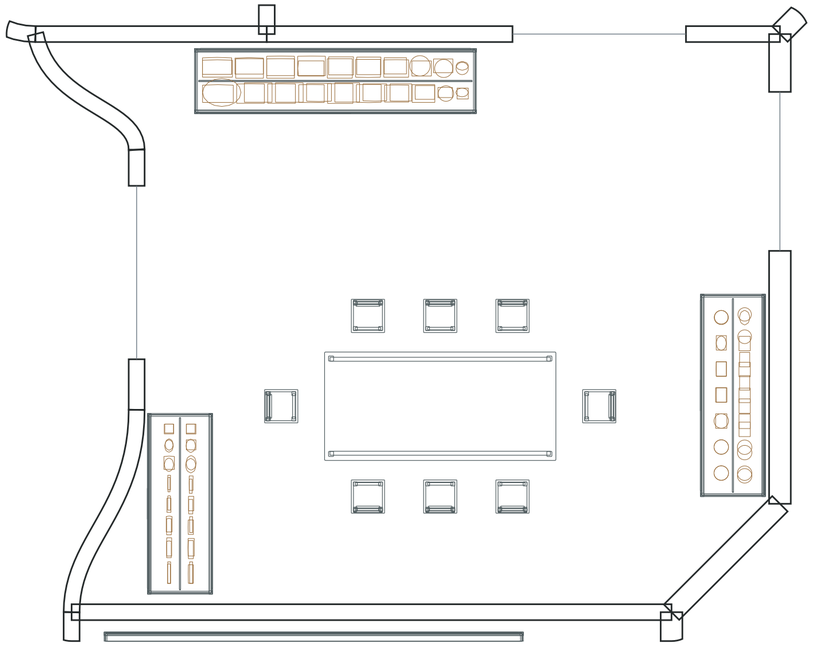

传香手作 • 八席

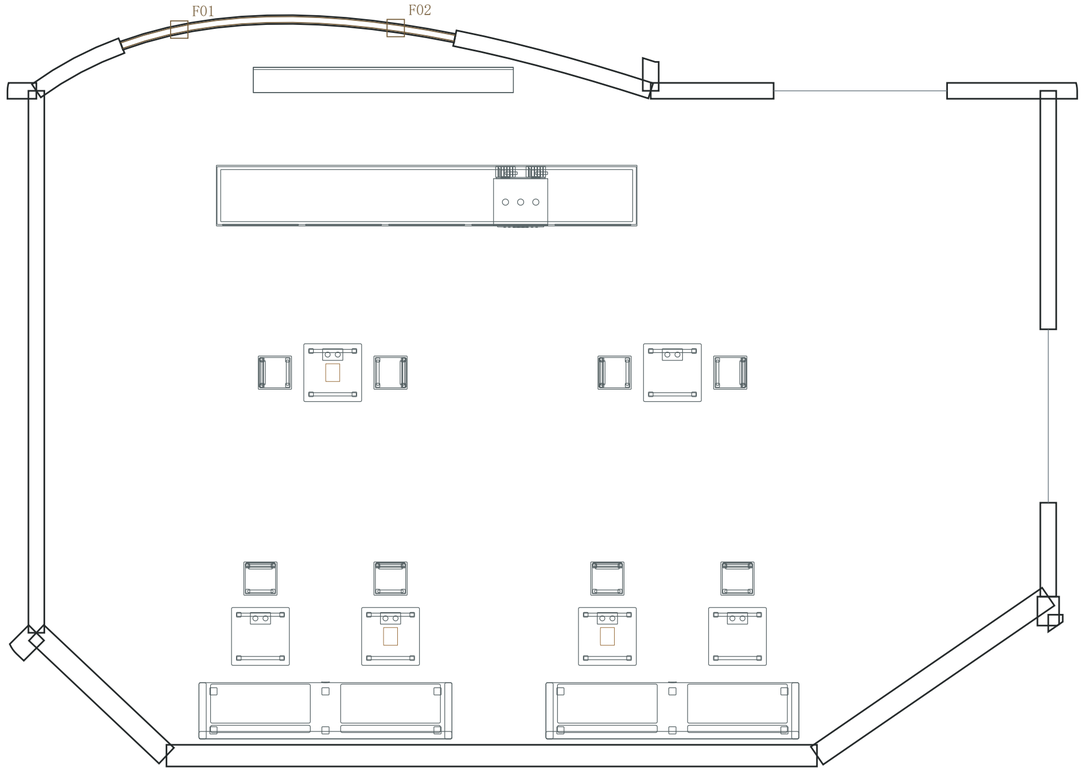

咖啡休憩 • 六桌十二席


手作桌椅沿用已确认位置。

咖啡保留两段卡座、八把活动椅。

吧台、清洗与储藏沿用现状模型。


图中展示实物外轮廓，窗详见第09张。

典型展柜与家具外形核对

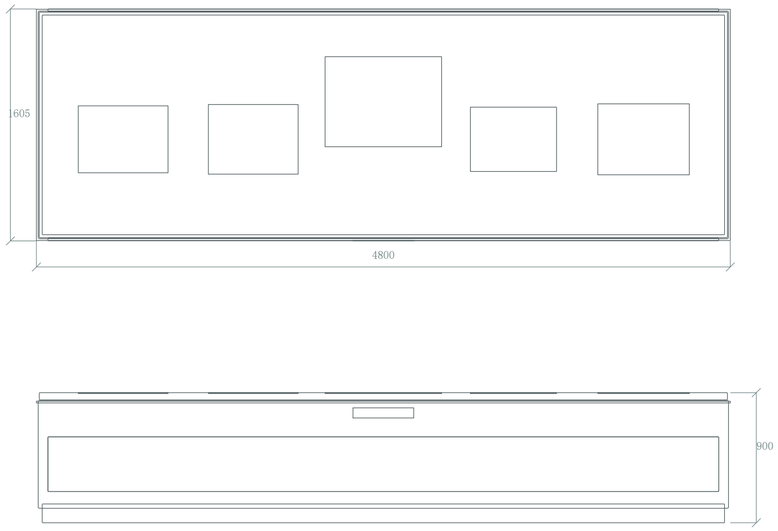


品香 • 中央主展台

上：平面 / 下：正面（不含展品）

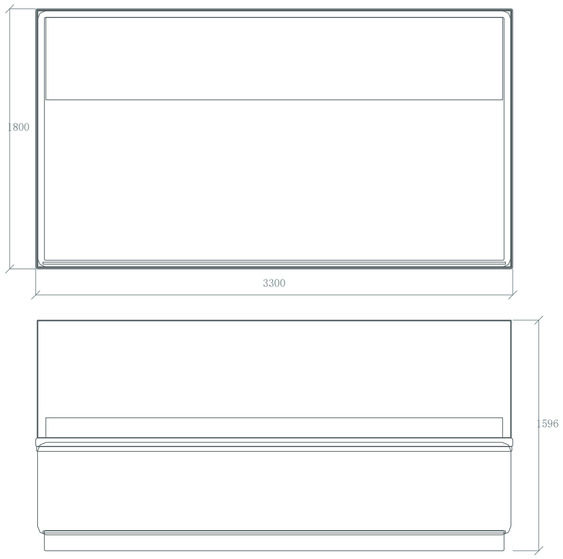

寻香 • M • 香市重点主台

上：平面 / 下：正面（不含展品）

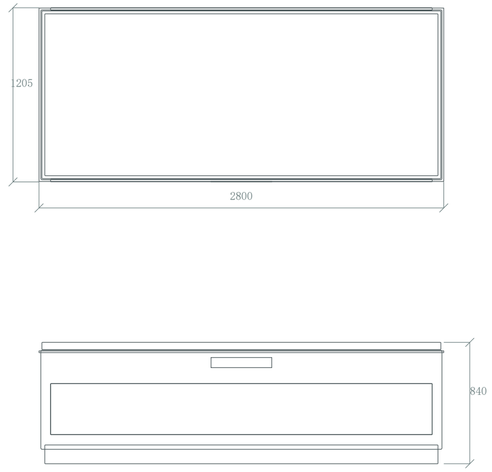


闻香 • 中央体验台

上：平面 / 下：正面（不含展品）




文创 • 中央香礼岛

上：平面 / 下：正面（不含展品）

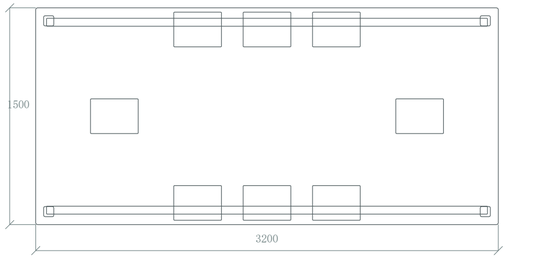

八席手作桌

上：平面 / 下：正面（不含展品）

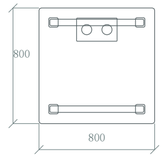


咖啡独立桌 • 1

上：平面 / 下：正面（不含展品）

本页为同源模型整体外形与占位核对；内部隔板、榫接和打印公差以后续加工深化为准。

五组花窗全馆定位与标高

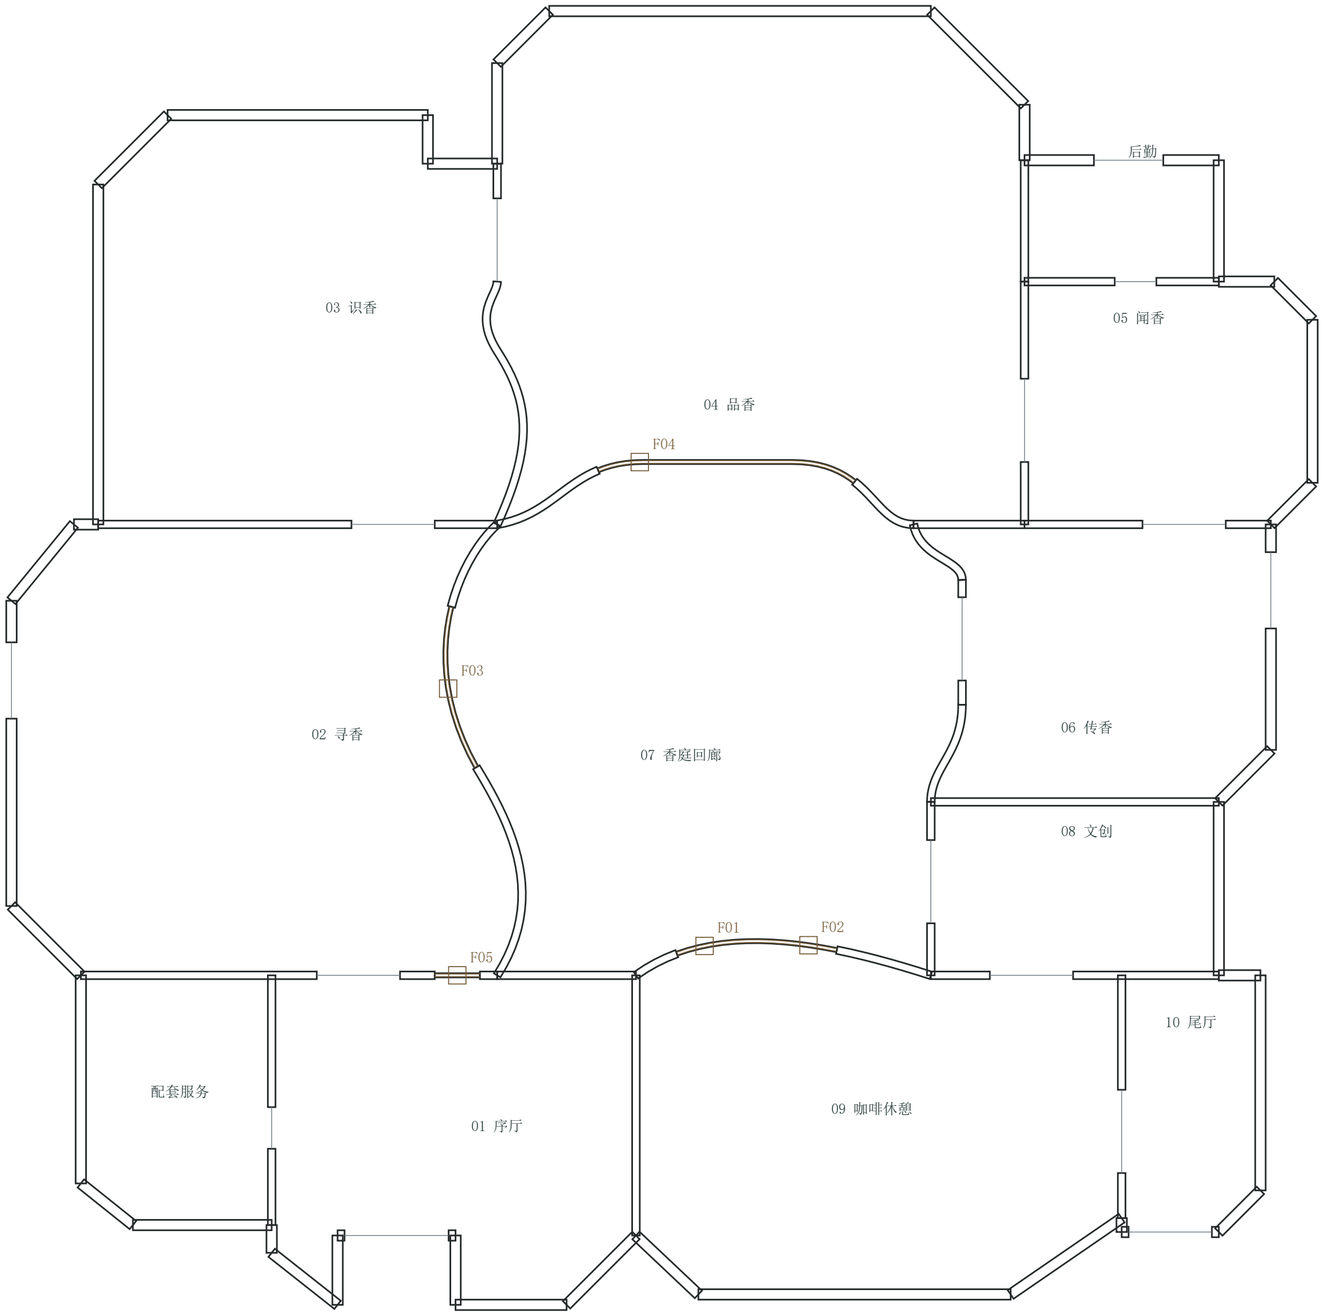

F01 咖啡左花窗

外框 1143 × 1143

中心标高 2020 / 如意回纹

定位 X 17977.0 Y 8847.5

F02 咖啡右花窗

外框 1143 × 1143

中心标高 2020 / 如意回纹

定位 X 20971.8 Y 8868.9

F03 寻香庭院花窗

外框 1332 × 1332

中心标高 2020 / 菱花竹叶

定位 X 10586.6 Y 16266.2

F04 品香回廊花窗

外框 1260 × 1260

中心标高 2020 / 海棠香叶

定位 X 16110.5 Y 22797.3

F05 序厅八角窗

外框 1080 × 1980

中心标高 2020 / 八角锦纹


定位 X 10850.0 Y 8000.0

定位数值对应原生模型项目坐标。

弧墙花窗详图采用沿墙展开坐标。

三维弧度以同期SKP为准。

咖啡左花窗纹样与构件详图

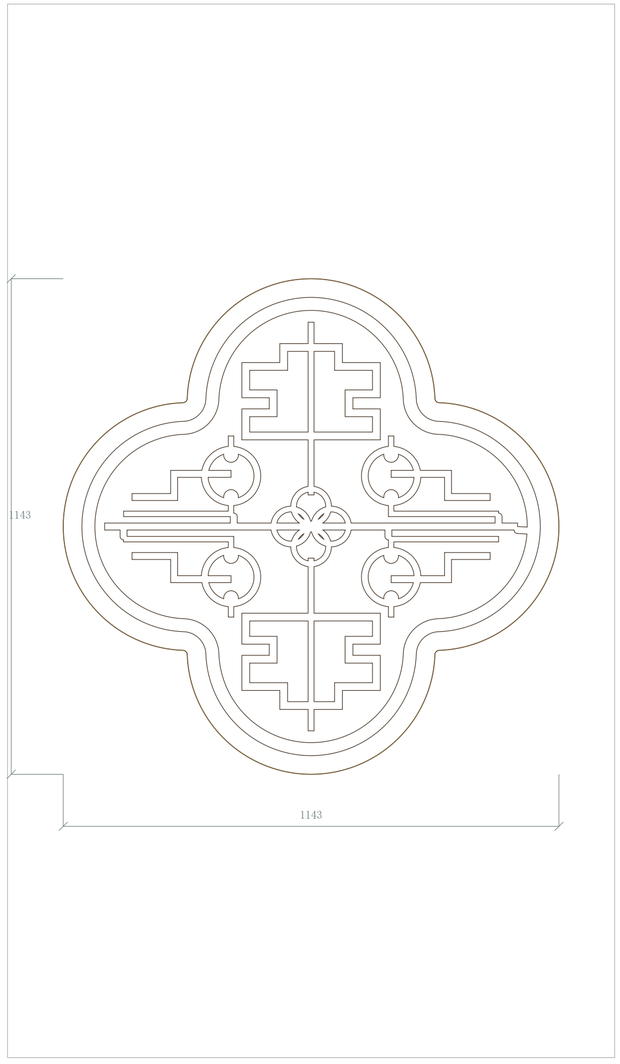

展开正面 • 原纹样保留

如意回纹

花窗外框：1143 × 1143

中心标高：2020

下沿标高：1448.5

上沿标高：2591.5

嵌板宽度：1400

嵌板高：2430

木纹样厚：50


暖灰框最大厚：60

木纹样与内框为连续封闭构件

F01、F02共用同一纹样与尺寸。

四瓣外框长宽相等，中心位置沿用。

法向层次 / 沿墙展开剖面

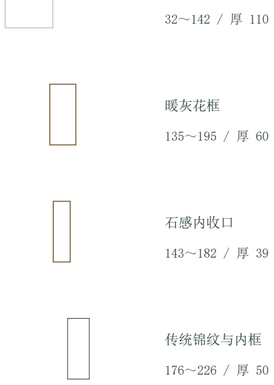

灰塑嵌板

32～142 / 厚 110

暖灰花框

135～195 / 厚 60

石感内收口

143～182 / 厚 39


传统锦纹与内框

176～226 / 厚 50

法向零点为原墙窗路径面，正方向按各窗所在侧。

展开详图用于核对花型与构件；现场弧度见原生模型。

寻香庭院花窗纹样与构件详图

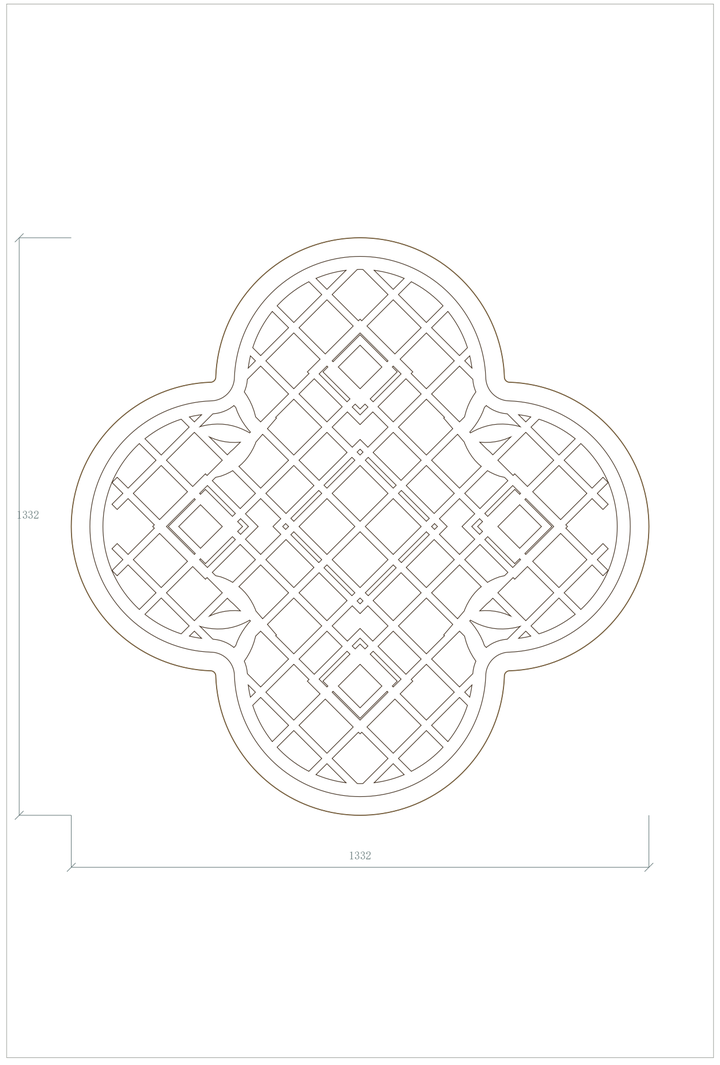

展开正面 • 原纹样保留

菱花竹叶

花窗外框：1332 × 1332

中心标高：2020

下沿标高：1354.0

上沿标高：2686.0

嵌板宽度：1630

嵌板高：2430

木纹样厚：50

暖灰框最大厚：60

木纹样与内框为连续封闭构件

法向层次 / 沿墙展开剖面



灰塑嵌板

32～142 / 厚 110



暖灰花框

135～195 / 厚 60



石感内收口

143～182 / 厚 39




传统锦纹与内框

176～226 / 厚 50

法向零点为原墙窗路径面，正方向按各窗所在侧。

展开详图用于核对花型与构件；现场弧度见原生模型。

品香回廊花窗纹样与构件详图

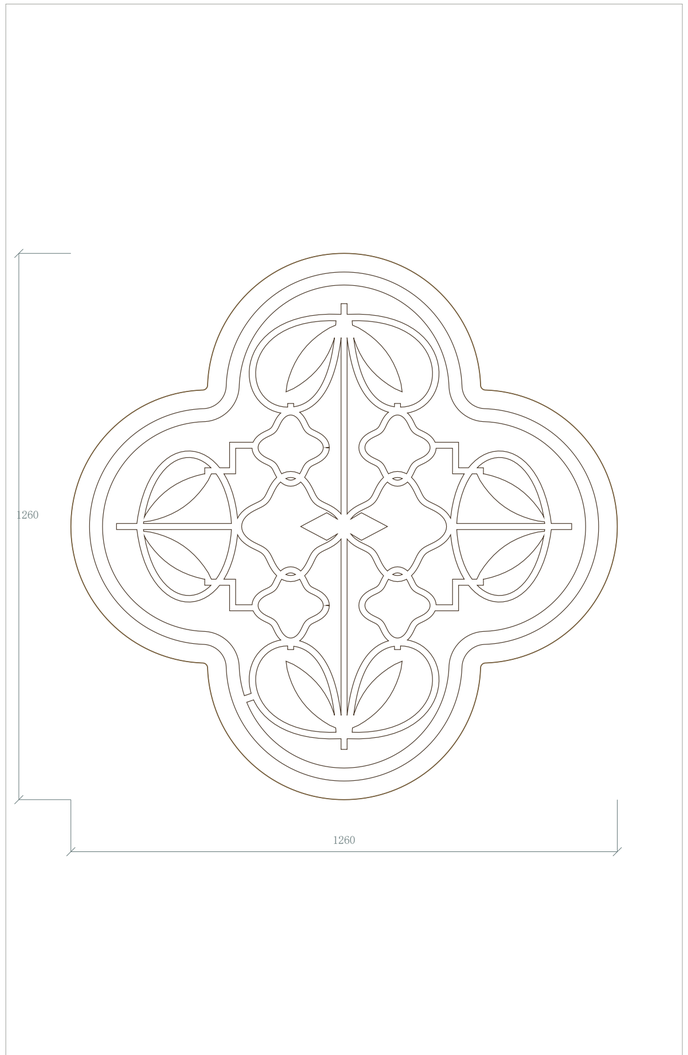

展开正面 • 原纹样保留

海棠香叶

花窗外框：1260 × 1260

中心标高：2020

下沿标高：1390.0

上沿标高：2650.0

嵌板宽度：1560


嵌板高：2430

木纹样厚：50

暖灰框最大厚：60

木纹样与内框为连续封闭构件

法向层次 / 沿墙展开剖面

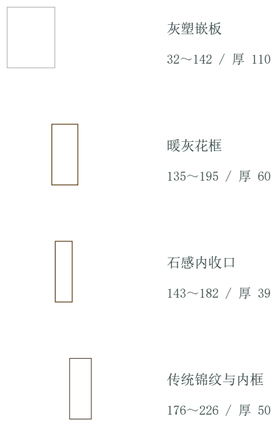

灰塑嵌板

32～142 / 厚 110

暖灰花框

135～195 / 厚 60

石感内收口

143～182 / 厚 39


传统锦纹与内框

176～226 / 厚 50

法向零点为原墙窗路径面，正方向按各窗所在侧。

展开详图用于核对花型与构件；现场弧度见原生模型。

序厅八角窗纹样与构件详图

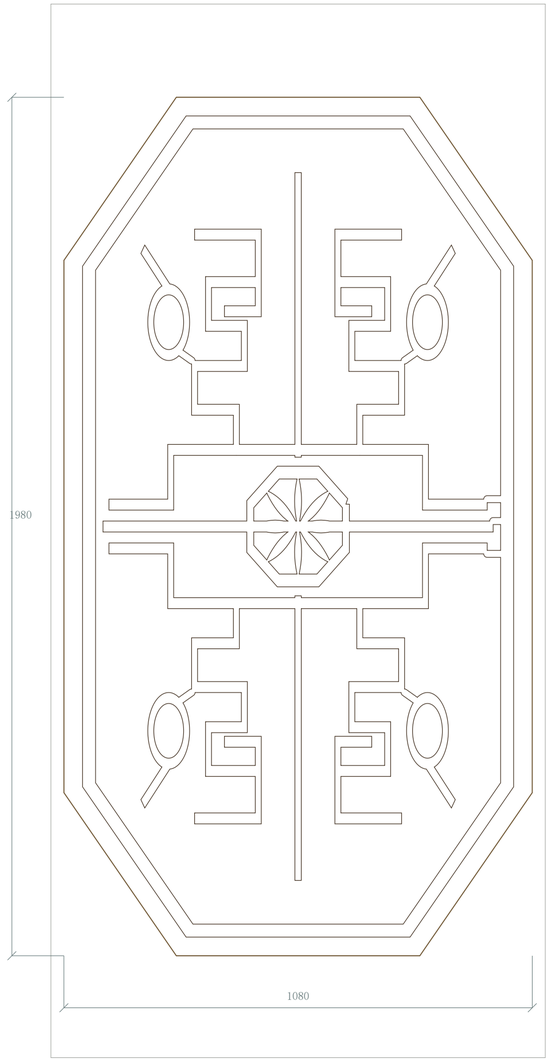

展开正面 • 原纹样保留

八角锦纹

花窗外框：1080 × 1980

中心标高：2020

下沿标高：1030.0

上沿标高：3010.0

嵌板宽度：1140


嵌板高：2430

木纹样厚：50

暖灰框最大厚：60

木纹样与内框为连续封闭构件

法向层次 / 沿墙展开剖面

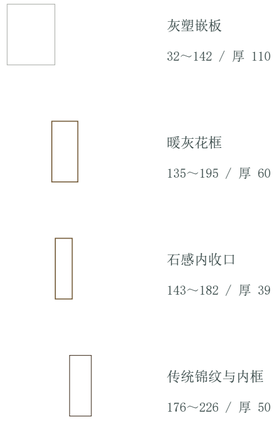

灰塑嵌板

32～142 / 厚 110

暖灰花框

135～195 / 厚 60

石感内收口

143～182 / 厚 39


传统锦纹与内框

176～226 / 厚 50

法向零点为原墙窗路径面，正方向按各窗所在侧。

展开详图用于核对花型与构件；现场弧度见原生模型。

微缩底板与全馆装配核对

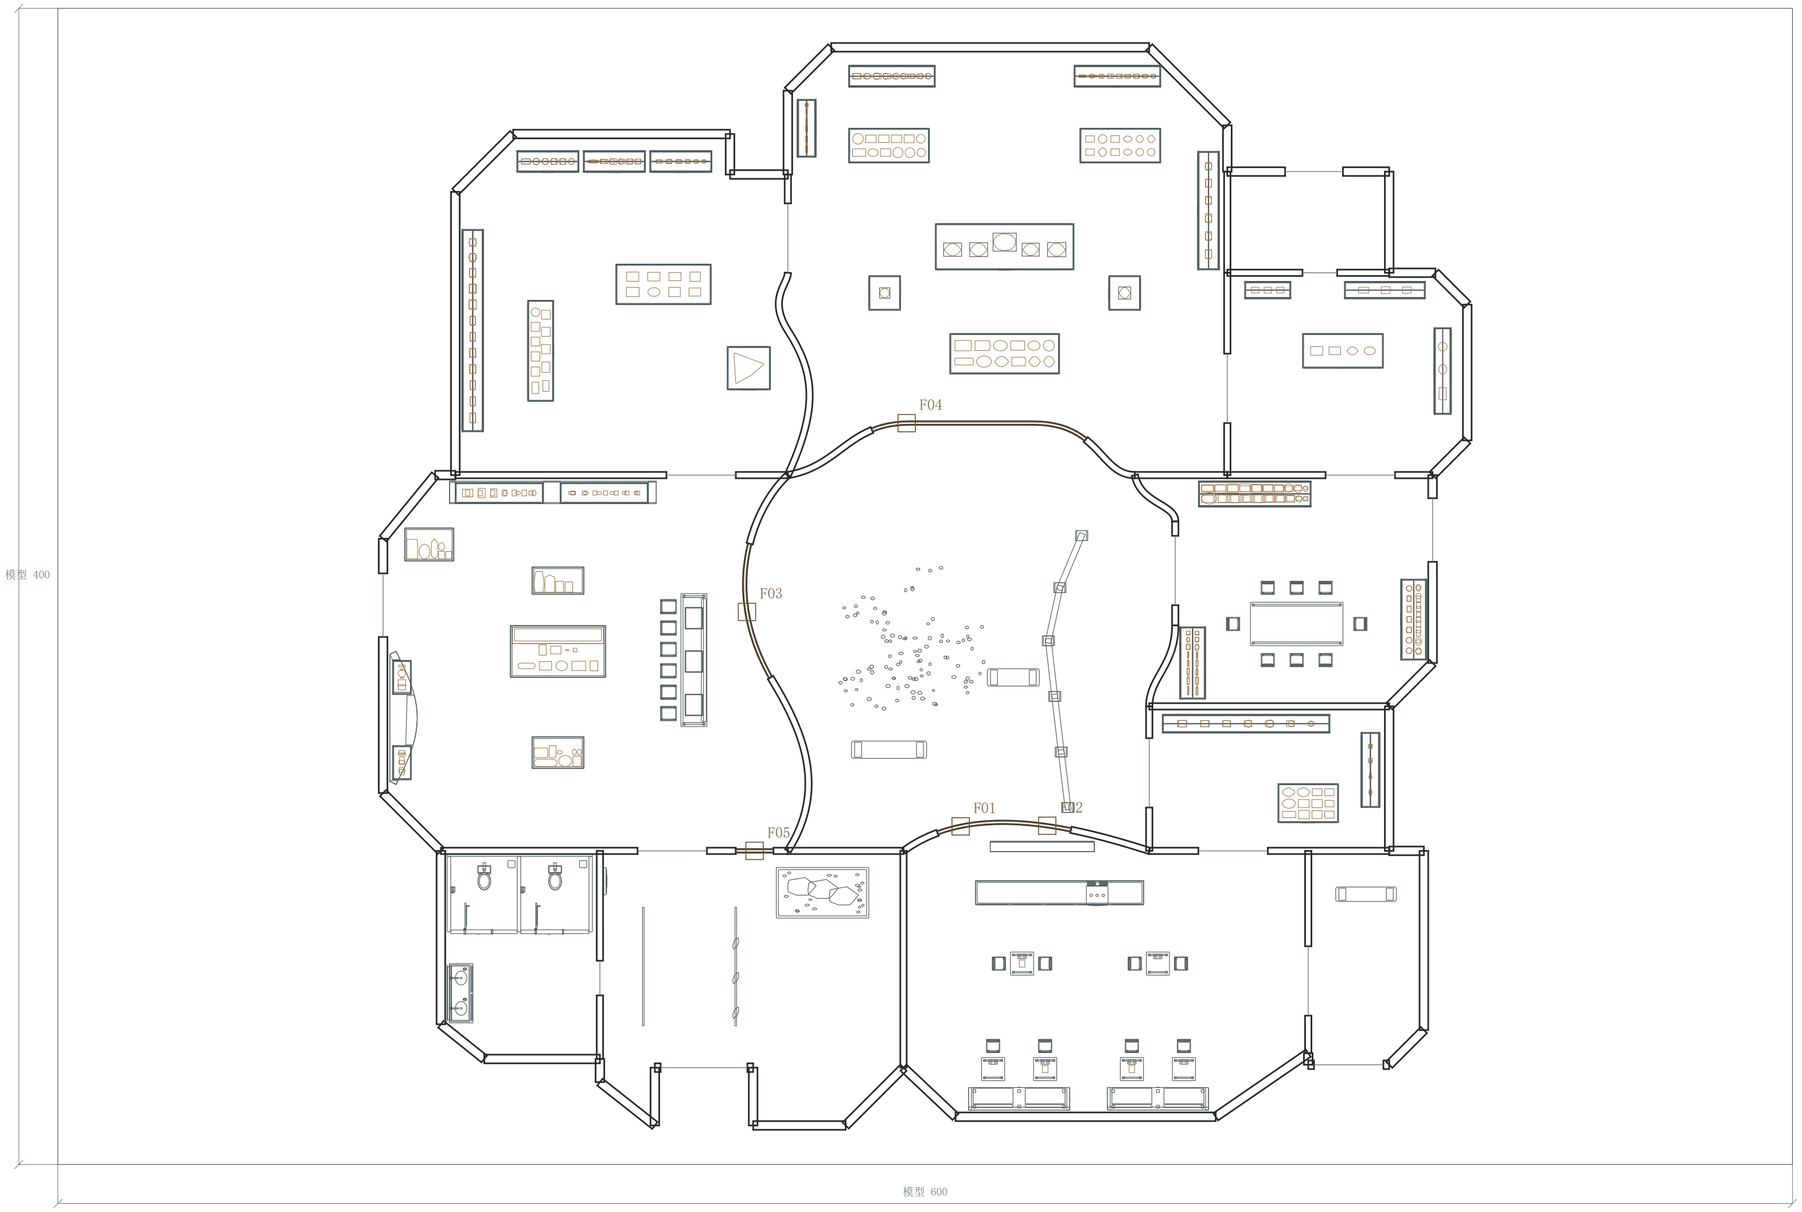

微缩模型比例 1:100

底板：600 × 400 mm

全馆保持去顶

上部无整顶装配件

本图DWG按实际毫米绘制

标注“模型”为尺寸×0.01

配套SKP另提供1:100文件

花窗模型外框：

咖啡：11.43 × 11.43 mm

寻香：13.32 × 13.32 mm

品香：12.60 × 12.60 mm

序厅：10.80 × 19.80 mm

白模、最小壁厚及公差

按商家设备另行深化