

莞香展馆

层院 · 时间剖面

技术图纸


十二类图纸 · 40张图页

图号 / 内容	合册页
D01 概念总平面	2—2
D02 全馆家具与公共服务区平面	3—4
D03 建筑开洞与展项定位	5—6
D04 地面材料分区与收边	7—10
D05 天花照明定位与高度	11—13
D06 建筑四向立面与门窗	14—14
D07 建筑剖面与接口关系	15—19
D08 寻香展区室内立面	20—20
D09 识香核心厅室内立面	21—21
D10 品香立面与体验陈设	22—25
D11 传香立面与站立示范	26—29
D12A 液晶墙安装与前维护协调	30—32
D12B 五柜构造与陈设	33—41

D12分为液晶墙与展柜两部分。

各图保留原始纸幅及比例；打印请选实际尺寸。

场地为概念假设；安装、产品及工程条件以各图注明范围为准。

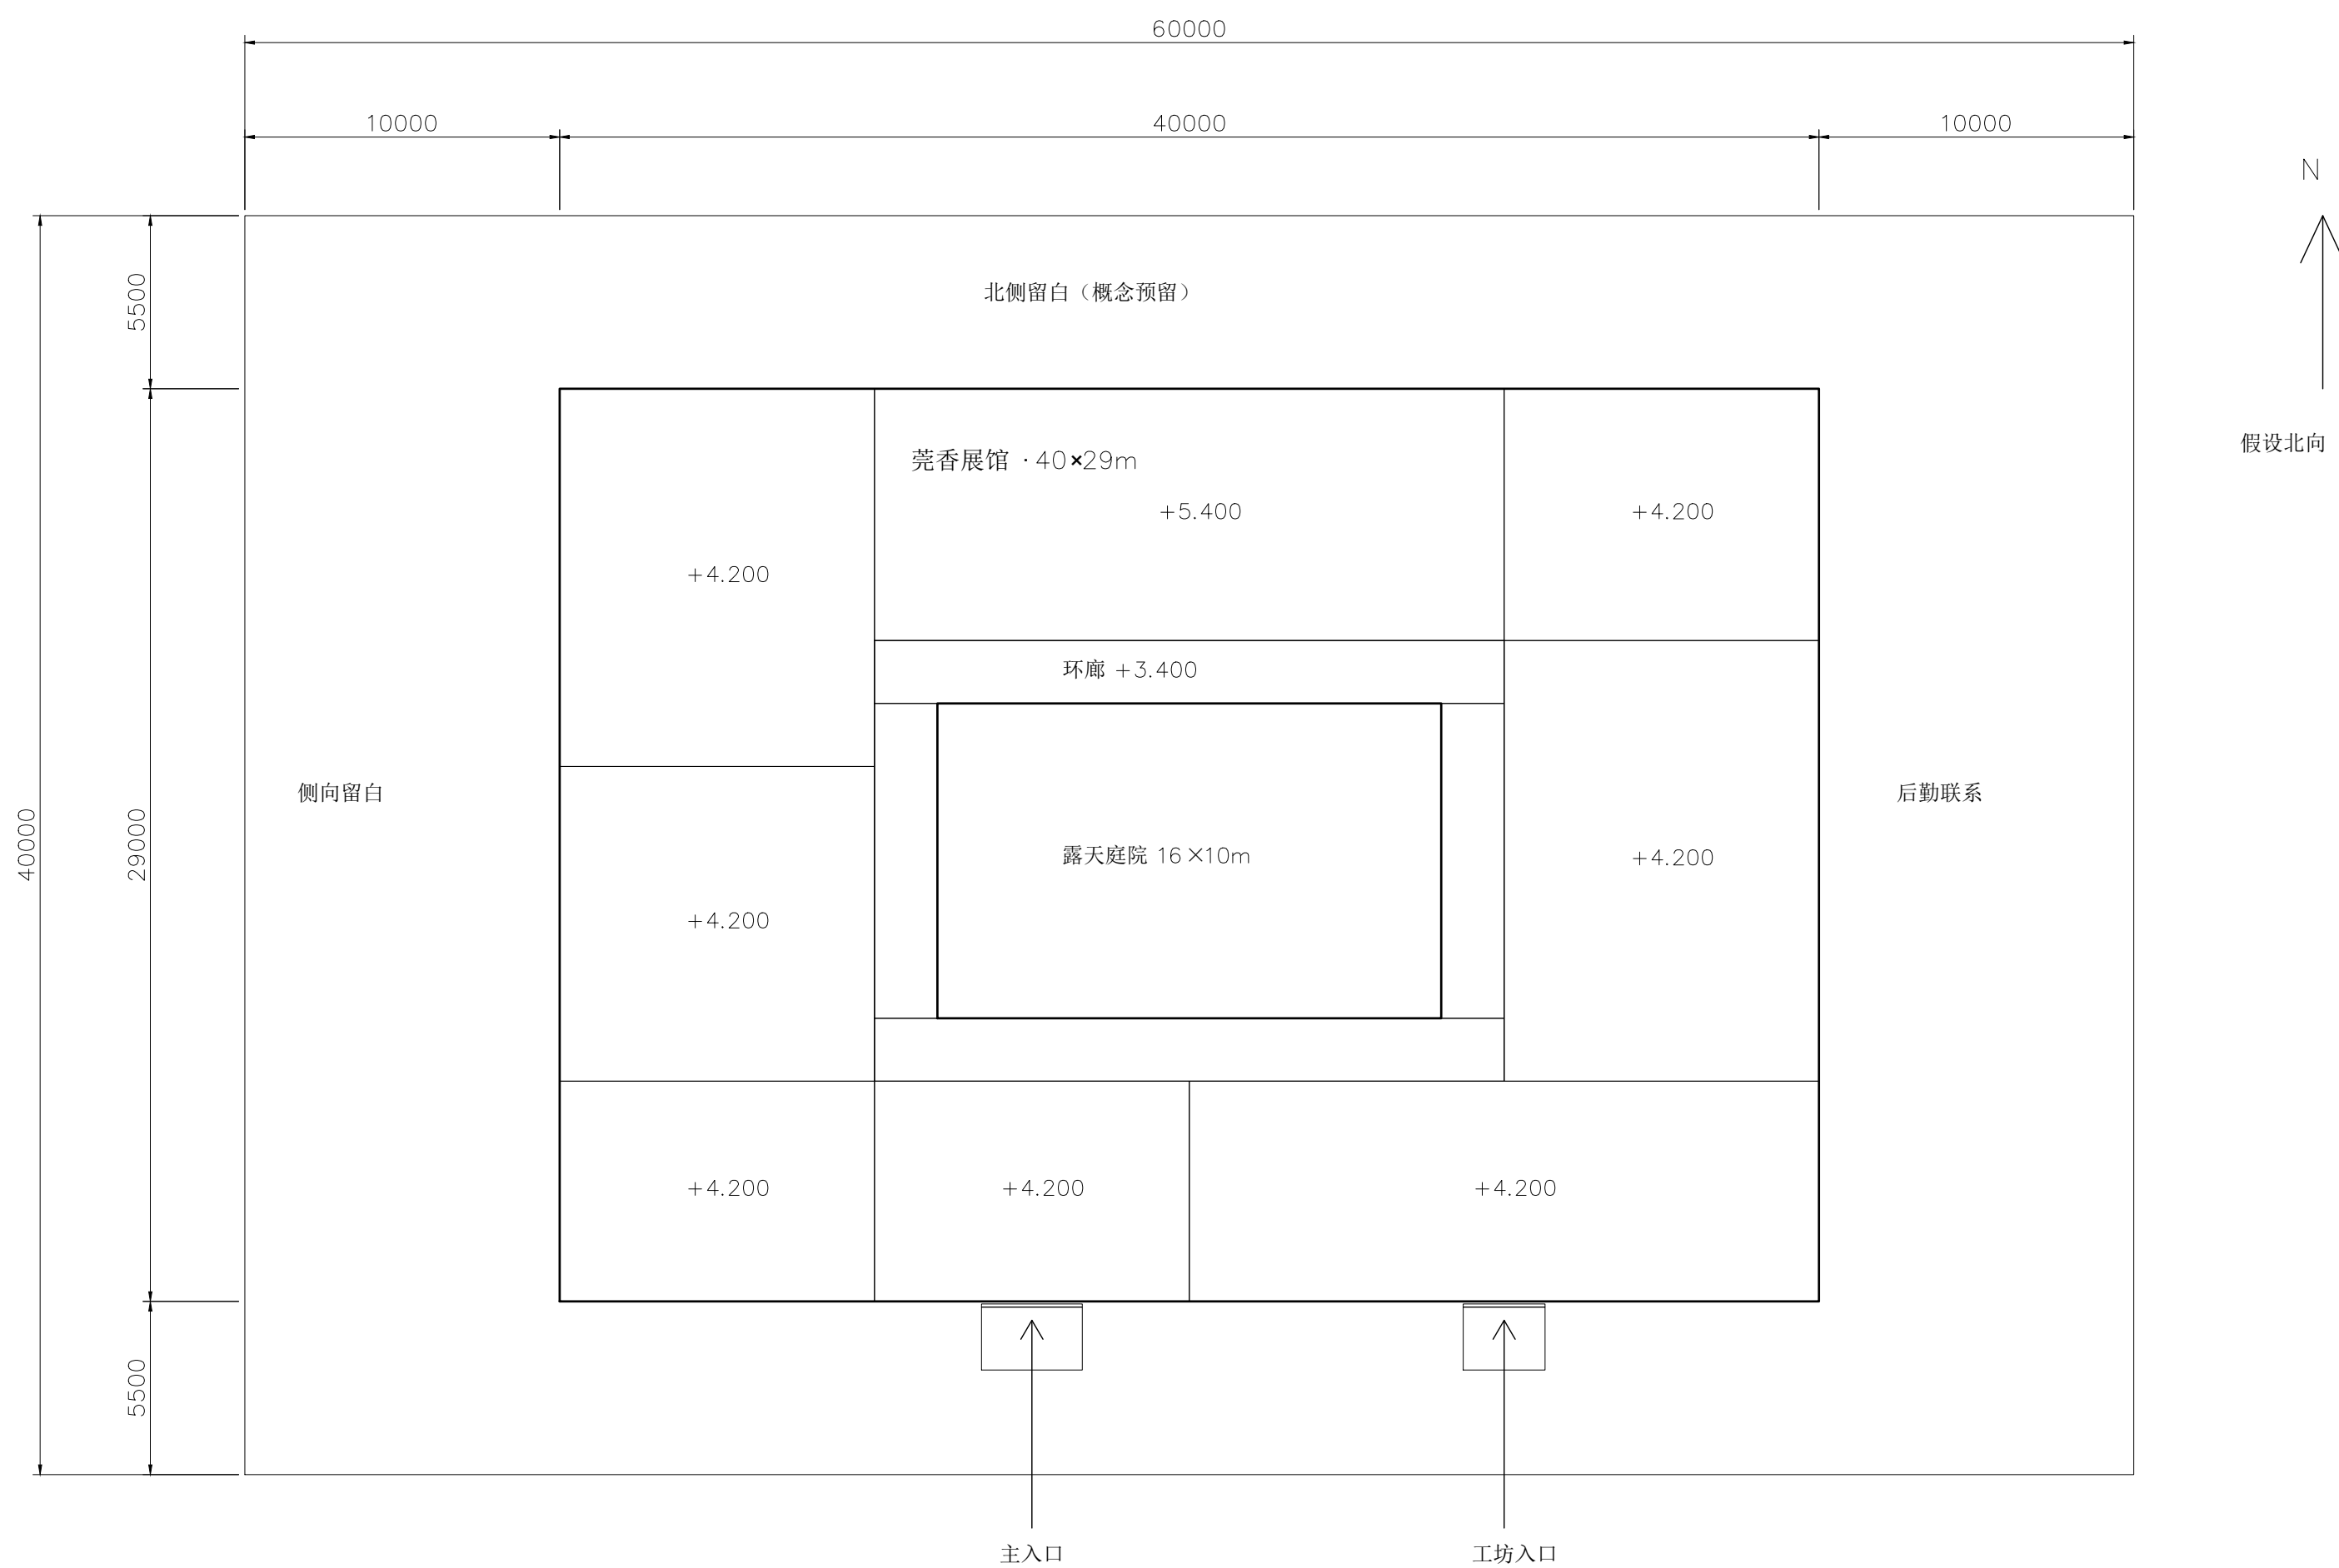

图面假设与面积口径

东莞莞城文化语境：真实地块未落实。

60×40m 为概念场地表达范围。

北向为假设；无实测道路或邻栋。

建筑外轮廓: $40 \times 29\text{m} = 1160\text{m}^2$ 。

露天庭院: $16 \times 10\text{m} = 160\text{m}^2$ 。

覆盖面积控制: $1160-160 = 1000 \text{ m}^2$ 。

该控制值不是法定建筑或净使用面积。

图中数值为屋面顶标高，非室内净高。


外部留白不代表工程退界或消防通道。

1:100微缩采用600×400mm底板。

图例

—— 建筑外轮廓
—— 屋面控制分块
—— 概念场地范围
—— 入口联系示意

图示比例尺

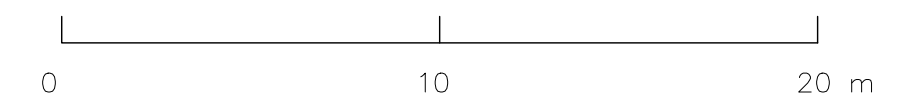

建筑坐标原点: $X=10000$, $Y=5500$ 。


施工节点及实测地块需另行深化。

入口外平台：主入口 3200×2000 、工坊入口 2600×2000 ；均向外1%找坡。

平台边缘顶-0.023；门前截水沟宽100。局部接口见D07/J04。

D02A 全馆家具平面

水平剖切+1.200，向下投影；玻璃保留透明轮廓。地面铺装接缝见D04。

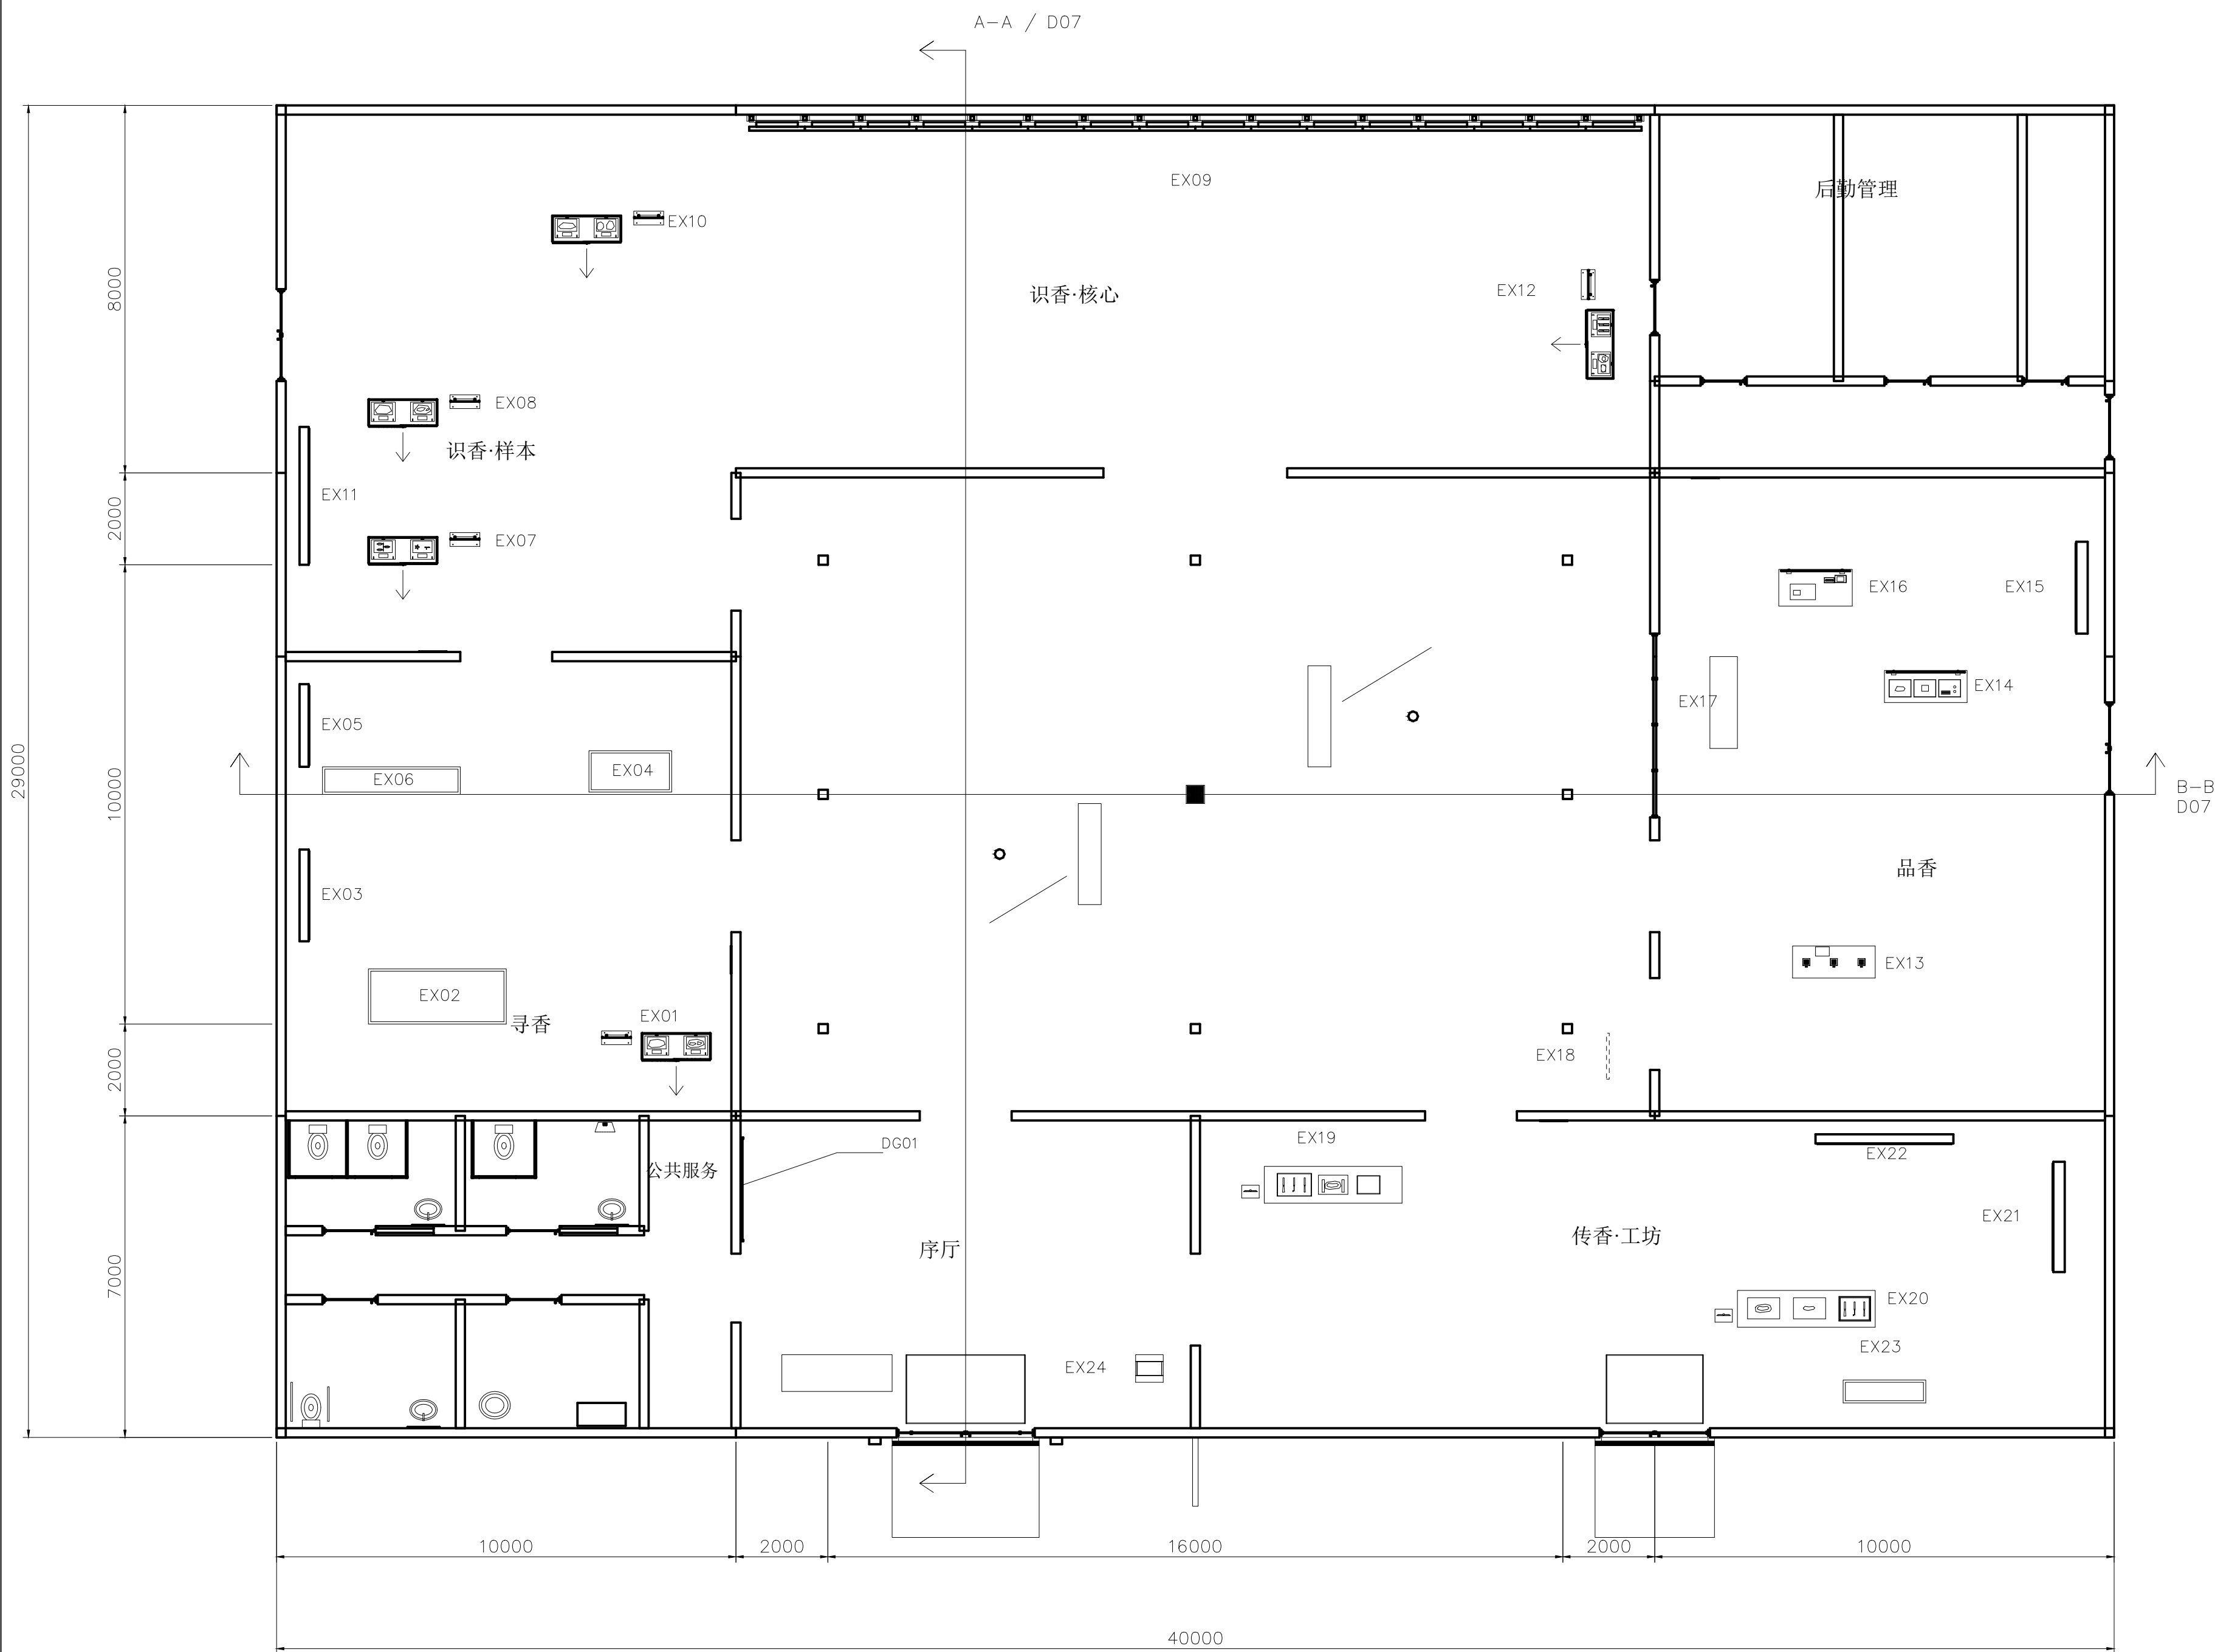

建筑原点O(0,0)，X向东、Y向北（假设北向）；外轮廓40×29m。

展项合并外包与开洞定位见D03；本图展具按水平切面及下方可见轮廓表达。

门扇按闭合位置绘制；开启示意见D02B。

图面读取

粗线：切到的墙、板与构件轮廓。

细线：切面以下可见的柜体、台面及器具。

玻璃不遮蔽后方内容；高于切面的部件不投影。

五柜小箭头指向正面；EX12朝西，其余朝南。

北墙为整墙液晶，中央保留观看空间。

未绘铺装接缝，避免与家具轮廓混淆。

EX18悬挂导引牌高于切面，用虚线作位置参考。

品香与站立示范

EX13闻香台、EX14香材与香品台、EX16参与台。

EX14/EX16信息板沿X展开，朝南；平面呈薄板切线。

EX17为休息点，EX18为导引服务牌。

EX19/EX20为站立观看手工艺示范区。

EX24知识终端采用600×600mm独立基座。

四章与编号

寻香：EX01—EX06

识香：EX07—EX12

品香：EX13—EX18（含两处服务点）

传香：EX19—EX24

图纸互引

D03定位 / D04地坪排水 / D05照明


D07剖面 / D10品香台 / D11站立工坊

D12A液晶墙 / D12B五柜详图

公共服务区详图见D02B。

D02B 公共服务区放大平面

水平剖切+1.200；虚线表示门扇开启范围及空间预留。

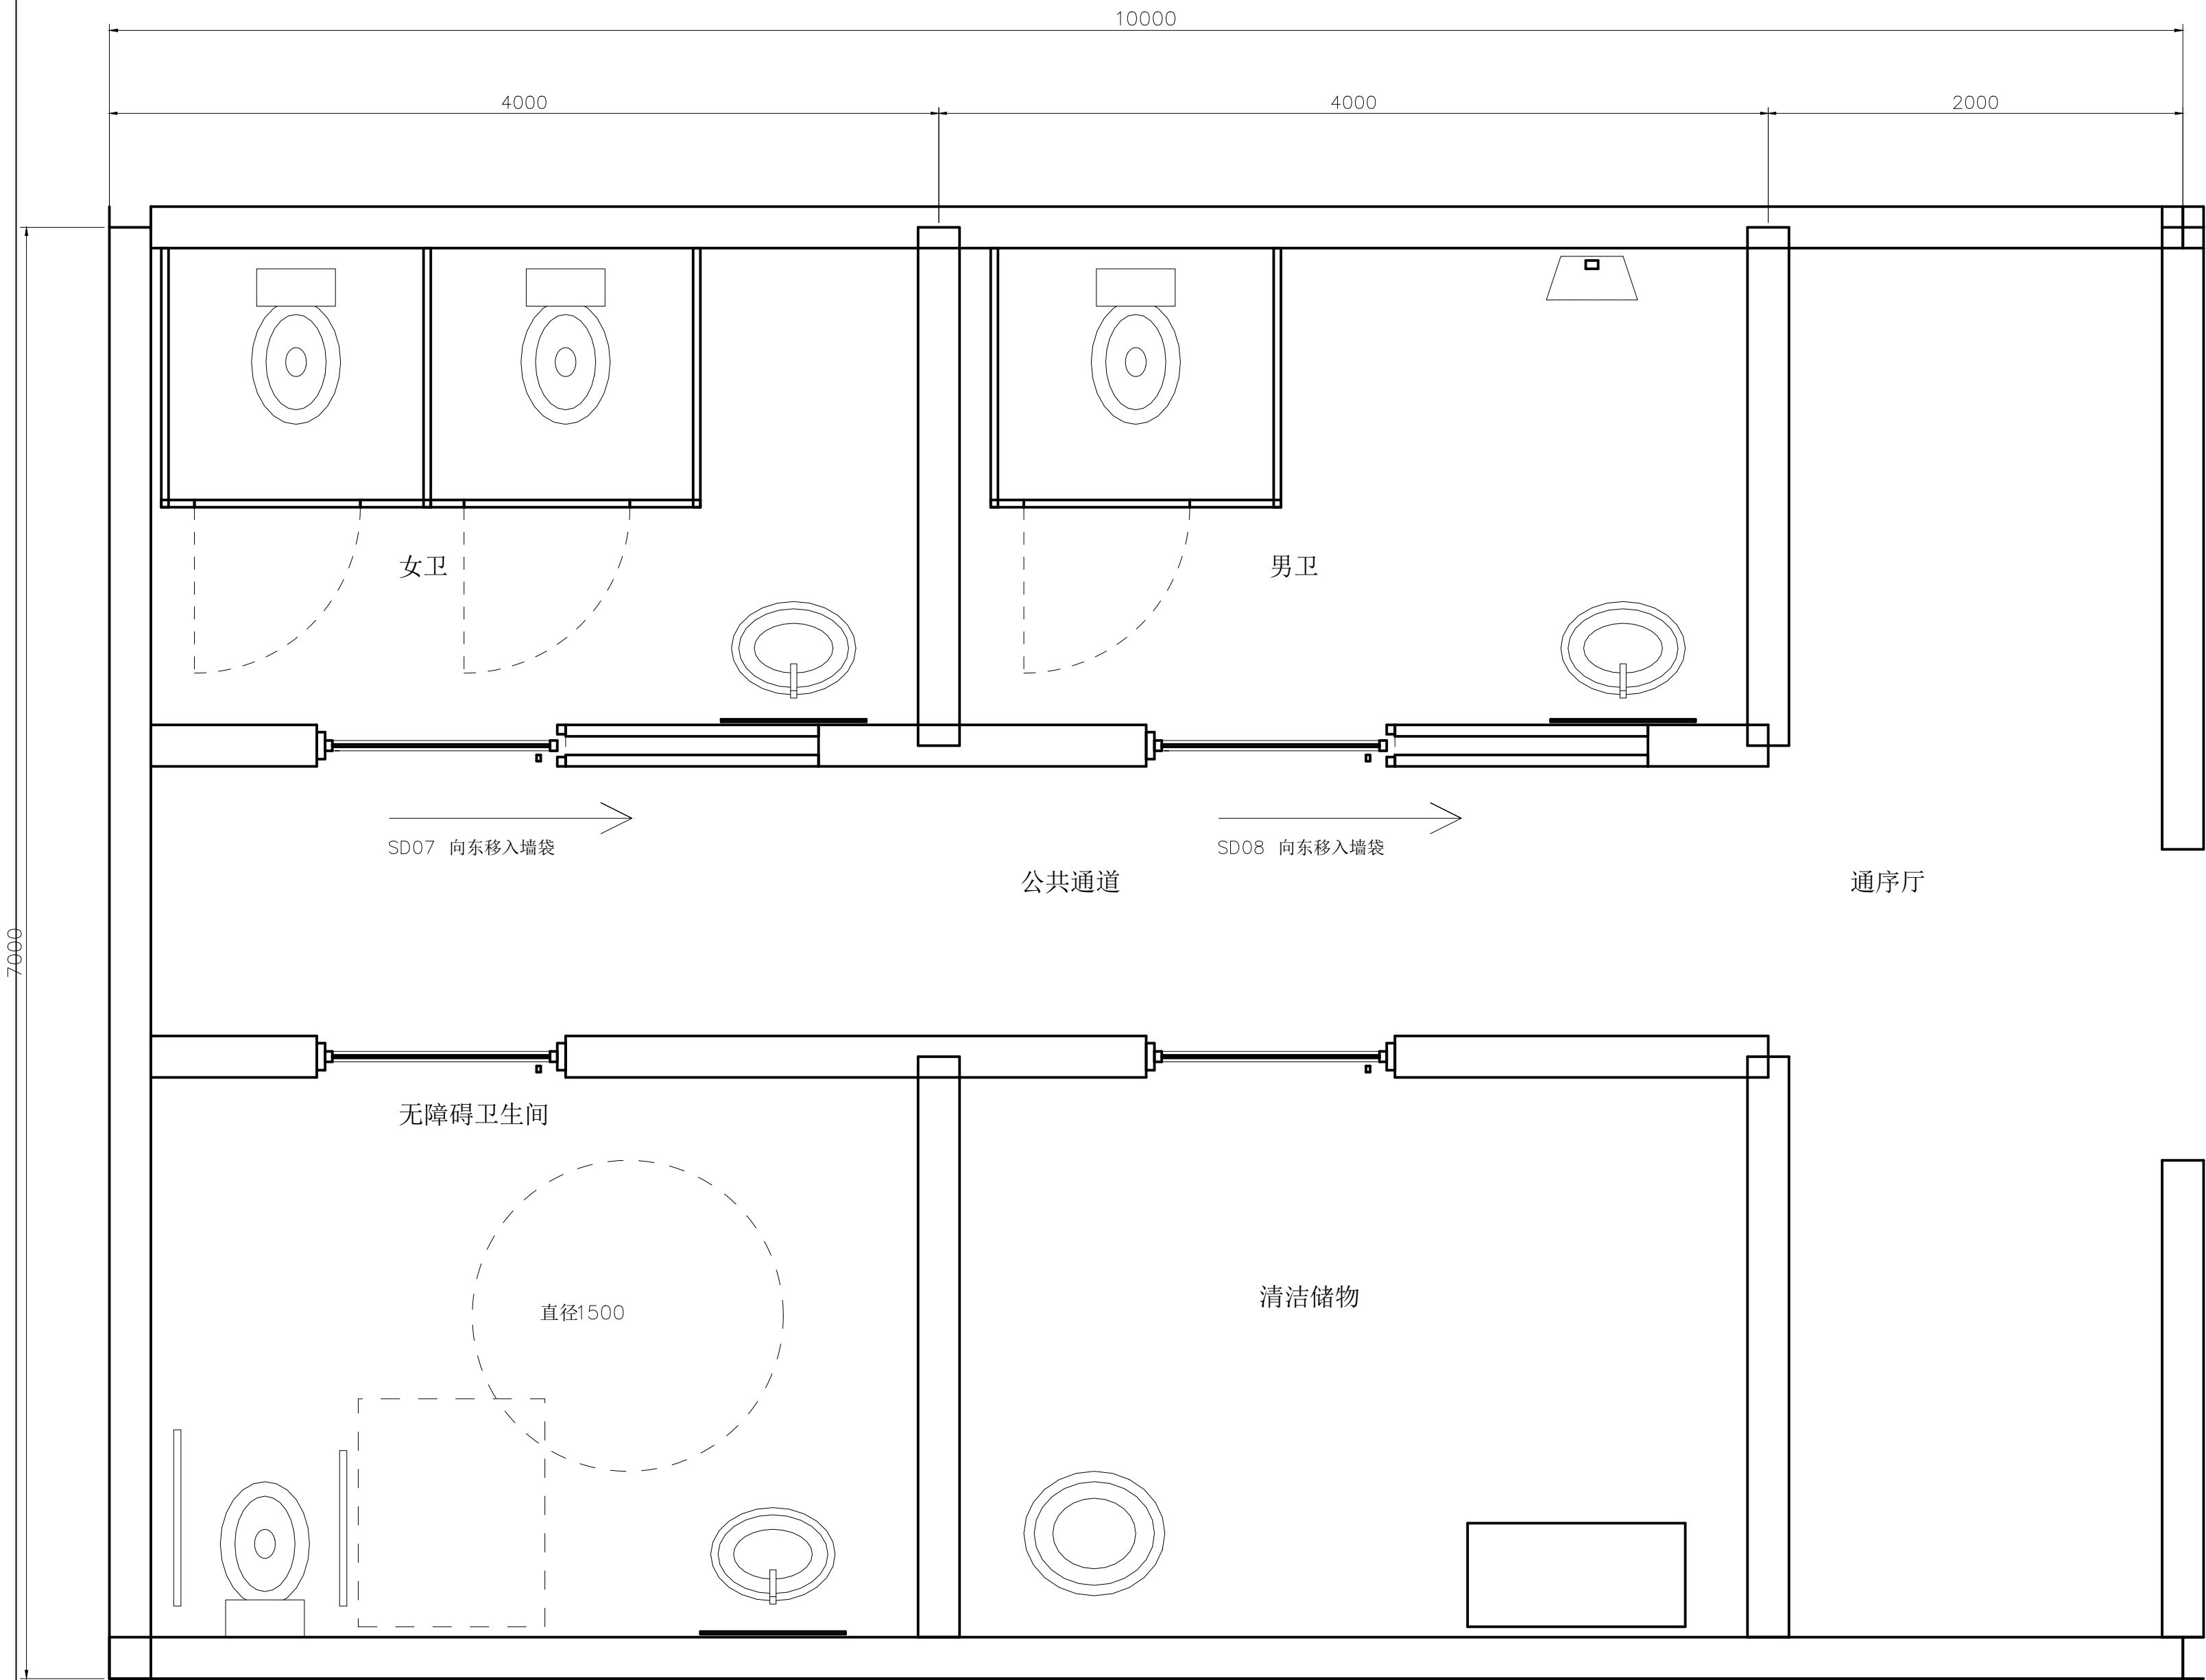

器具与空间尺寸

女卫：2坐便、1洗手盆。

男卫：1坐便、1小便、1洗手盆。

无障碍间：1坐便、1洗手盆。

清洁间：拖布池及储物。

SD07/O8向东暗藏，移动1170。

墙袋净预留1220，门扇闭合示于实线。

厕位前参考净通道1050；

隔间参考净深1215。

圆形为轮椅回转空间，

矩形为侧向移乘预留。

门袋、五金、给排水和器具选型

仍需后续专项深化。


实线：构件轮廓
短虚线：开启范围/空间预留
门洞编号与名义尺寸见D03B。

本页裁切至X=10100、Y=7100。
裁切边缘不表示建筑在此断开。
服务区与序厅相接。

D03A 全馆定位 / 原点为建筑外轮廓西南角

定位包络含展具、图文架及附属标识；26处开洞见D03B。

墙体切面+1.200；展项框为全部附件外包。小箭头指柜体正面。

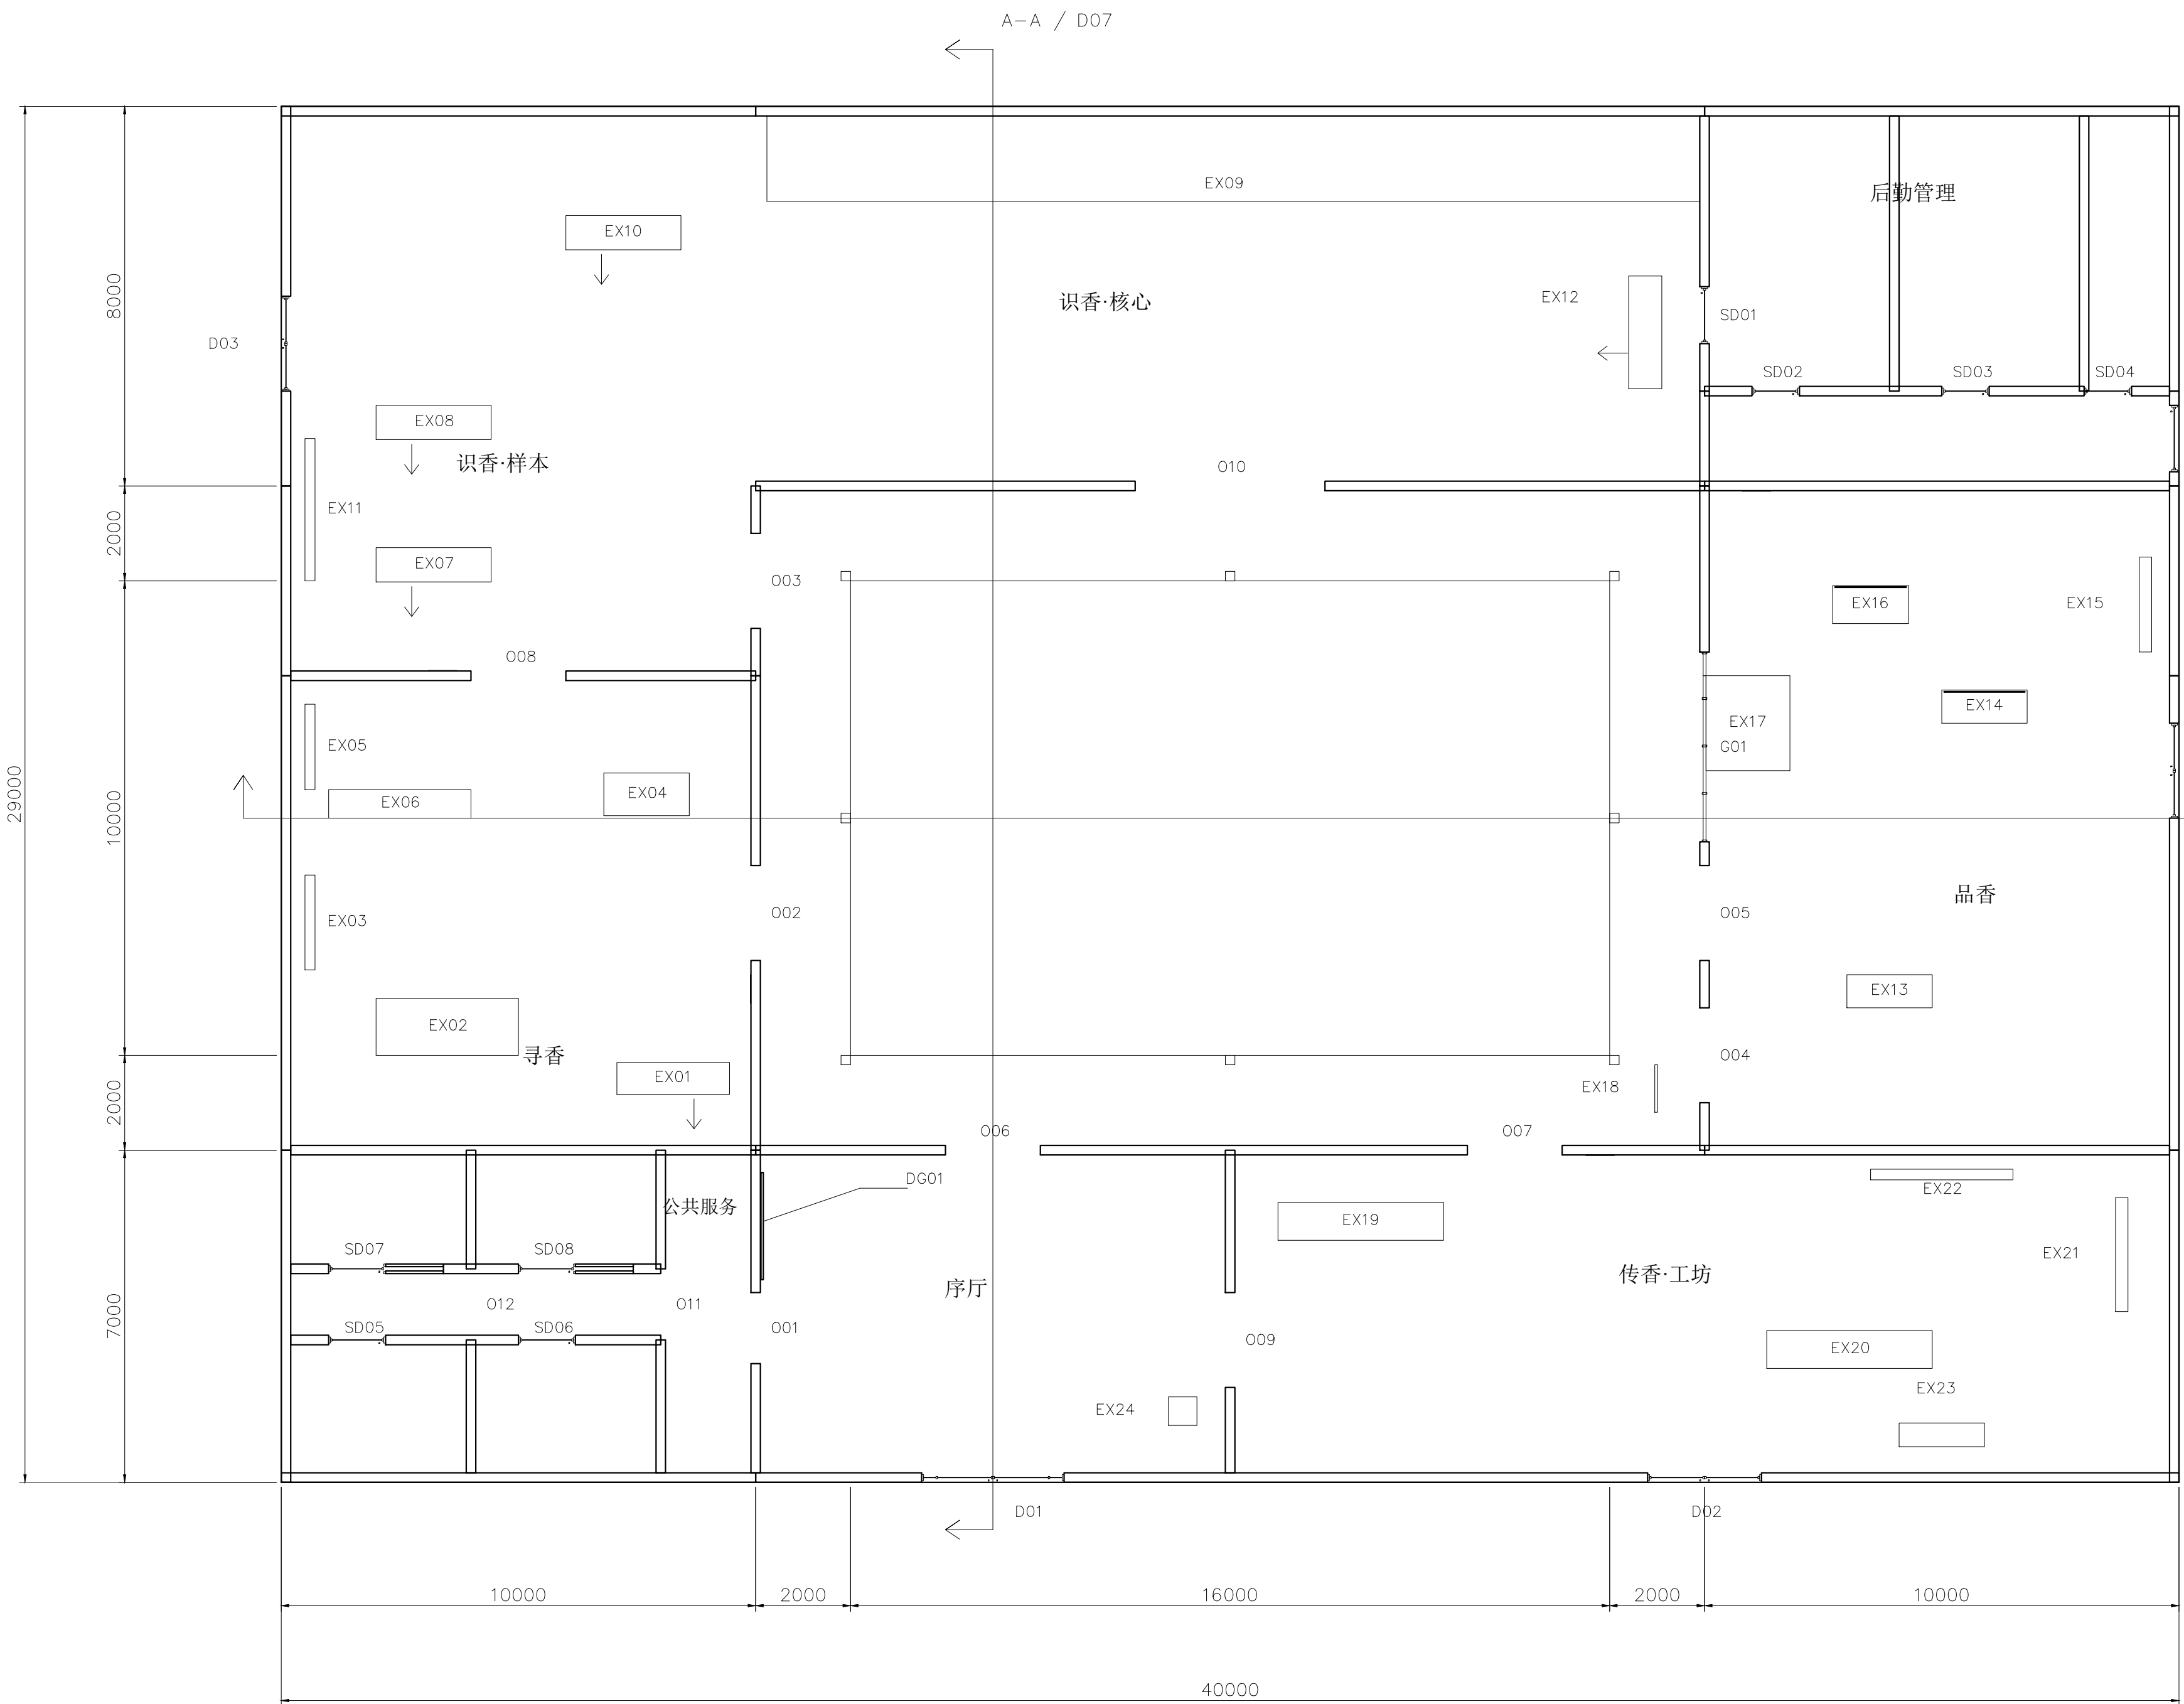

坐标原点 O(0,0)；X向东、Y向北（假设北向）；名义外轮廓40×29m。

外轮廓1160㎡ / 庭院160㎡ / 覆盖面积控制约1000㎡，非法定建筑面积。

DG01 序厅导览：内容面2200×1540，底标高+0.700；安装于W11东侧。

展项合并包络与定位 / mm

编号	X	Y	宽	深	高
EX01	7075	8176.85	2375	673.15	1540
EX02	2000	9000	3000	1200	772
EX03	500	10800	212	2000	1650
EX04	6800	14050	1800	900	772
EX05	500	14600	212	1800	1650
EX06	1000	14000	3000	600	772
EX07	2000	18976.8	2425	723.15	1540
EX08	2000	21976.8	2425	723.15	1980
EX09	10237.4	27000	19662.6	1800	4454
EX10	6000	25976.8	2425	723.15	1540
EX11	500	19000	212	3000	1650
EX12	28400	23050	700	2375	1540
EX13	33000	10000	1800	700	906
EX14	35000	16000	1800	700	1440
EX15	39163	17500	262	2000	1650
EX16	32700	18100	1600	800	1540
EX17	30030	15000	1770	2000	1200
EX18	28950	7800	60	1000	300
EX19	21010	5100	3490	800	1200
EX20	31310	2400	3490	800	1200
EX21	38663	3600	262	2400	1650
EX22	33500	6374	3000	226	1650
EX23	34100	750	1800	500	772
EX24	18700	1200	600	600	1000

包络包含支架/附件，不能当作展品实物尺寸。
EX09含屏体及支承；画布另见D12A。
EX19/EX20为站立手工艺示范区。

- Z01 600×1000主板 X9888 Y10100 Z1000
- Z02 600×1000主板 X3100 Y17100 Z1000
- Z03 600×1000主板 X30800 Y20888 Z1000
- Z04 600×1000主板 X27500 Y6888 Z1000


EX14/EX16竖向信息板：沿X展开、朝南；加粗短线示板位。

详图引用：
D06 门窗立面 / D07 A-A、B-B剖面
D08-D11 四章展陈立面
D12A 液晶墙 / D12B 五柜详图

图例：粗线墙体 / 细线框件与展具
D、SD为门；O为无门扇通口；G01为玻璃界面。

D03B 沿墙开洞尺寸链 / 与D03A 编号对应

条带横向为1:100，竖向仅表达墙段和开口关系；尺寸为名义开洞，非完成净宽。

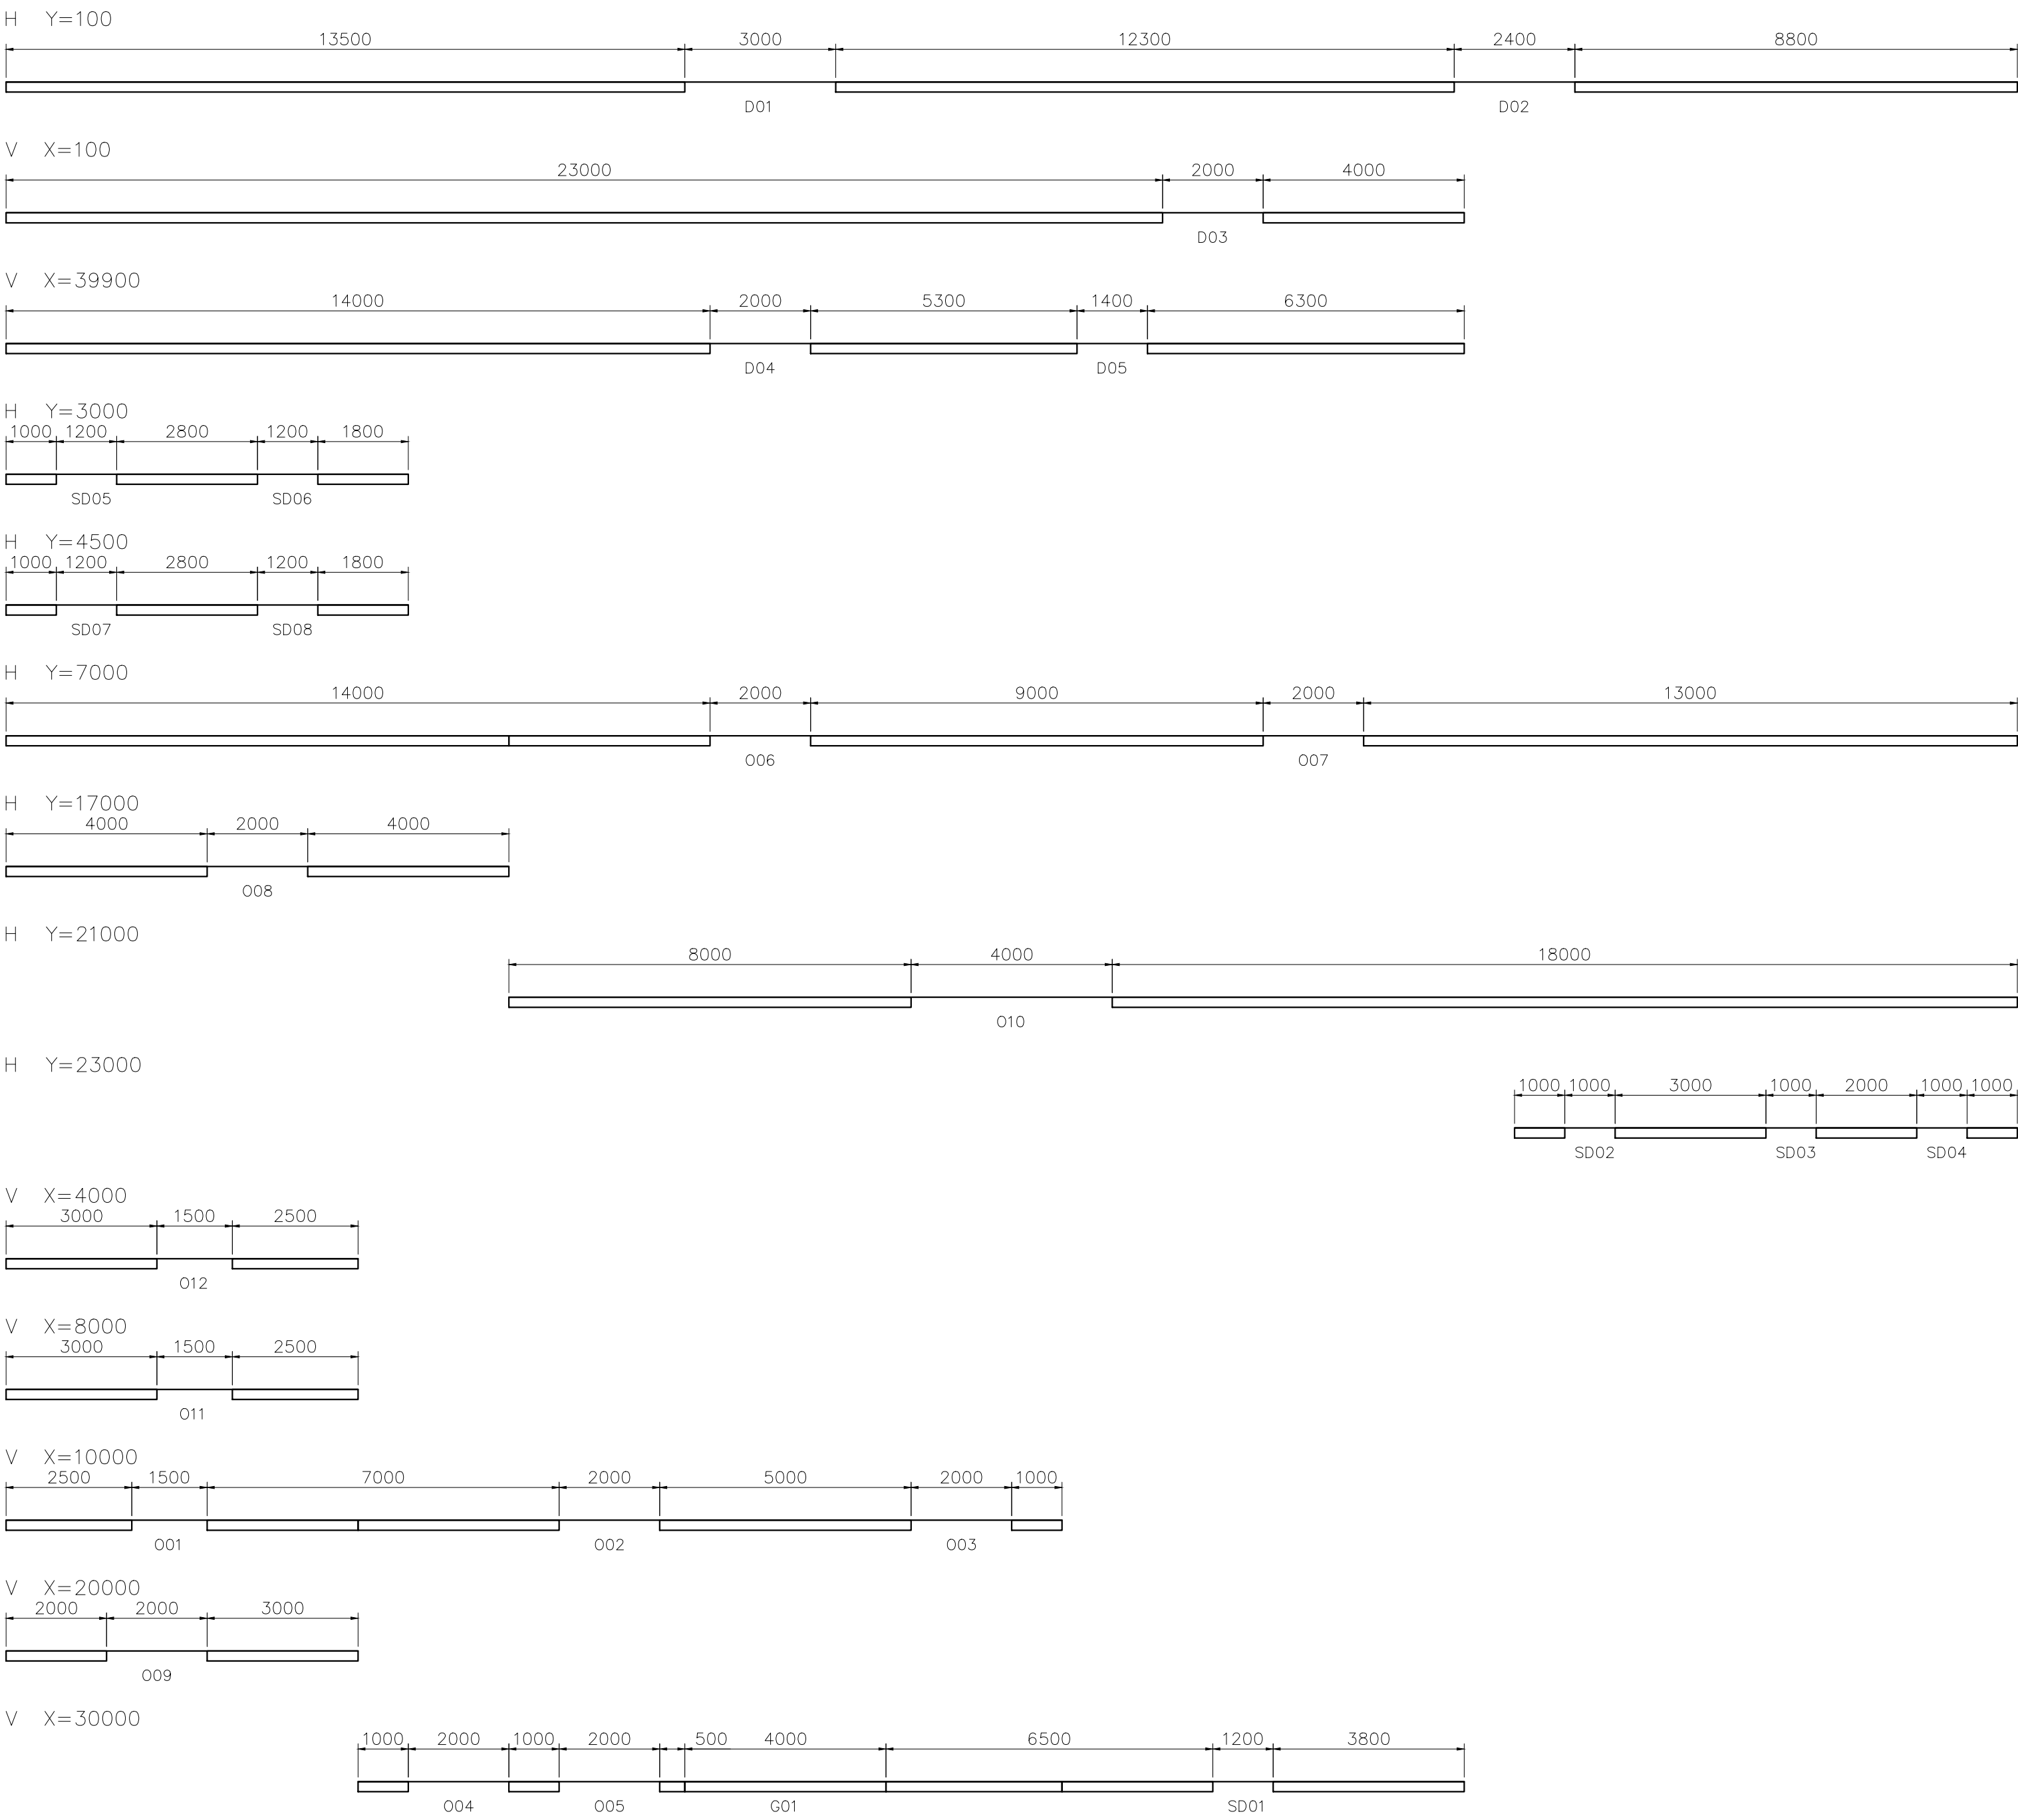

开洞与玻璃界面表 / mm

编号	轴线	起点	宽	高	属性
D01	H100	13500	3000	2800	门
D02	H100	28800	2400	2800	门
D03	V100	23000	2000	2800	门
D04	V39900	14000	2000	2800	门
D05	V39900	21300	1400	2400	门
O01	V10000	2500	1500	2400	洞口
O02	V10000	11000	2000	2800	洞口
O03	V10000	18000	2000	2800	洞口
O04	V30000	8000	2000	2800	洞口
O05	V30000	11000	2000	2800	洞口
SD01	V30000	24000	1200	2400	门
O06	H7000	14000	2000	2800	洞口
O07	H7000	25000	2000	2800	洞口
O08	H17000	4000	2000	2800	洞口
O09	V20000	2000	2000	2800	洞口
O10	H21000	18000	4000	2800	洞口
SD02	H23000	31000	1000	2400	门
SD03	H23000	35000	1000	2400	门
SD04	H23000	38000	1000	2400	门
O11	V8000	3000	1500	2400	洞口
SD05	H3000	1000	1200	2400	门
SD06	H3000	5000	1200	2400	门
SD07	H4500	1000	1200	2400	门
SD08	H4500	5000	1200	2400	门
O12	V4000	3000	1500	2400	洞口
G01	V30000	13500	4000	2800	玻璃

H轴线：沿X读起点；V轴线：沿Y读起点。
高度为模型洞口顶标高相对±0.000。
SD07/08为藏入东侧墙袋的移门方案。
门框、门扇、五金会影响完成净宽。
G01为4m玻璃界面，不是4m通行口。


26处界面，14组沿墙尺寸链；编号及位置见D03A。

门窗材料、门框及五金选型应与洞口尺寸协调。

D04A 地面材料 / 方向与边界控制

五类面层与铺装分格：暖灰与灰米色。定位单位mm。

细线为模数板缝中心，标注处断开：缝宽2/3，场界两侧各2.5。分格坐标见D04C。

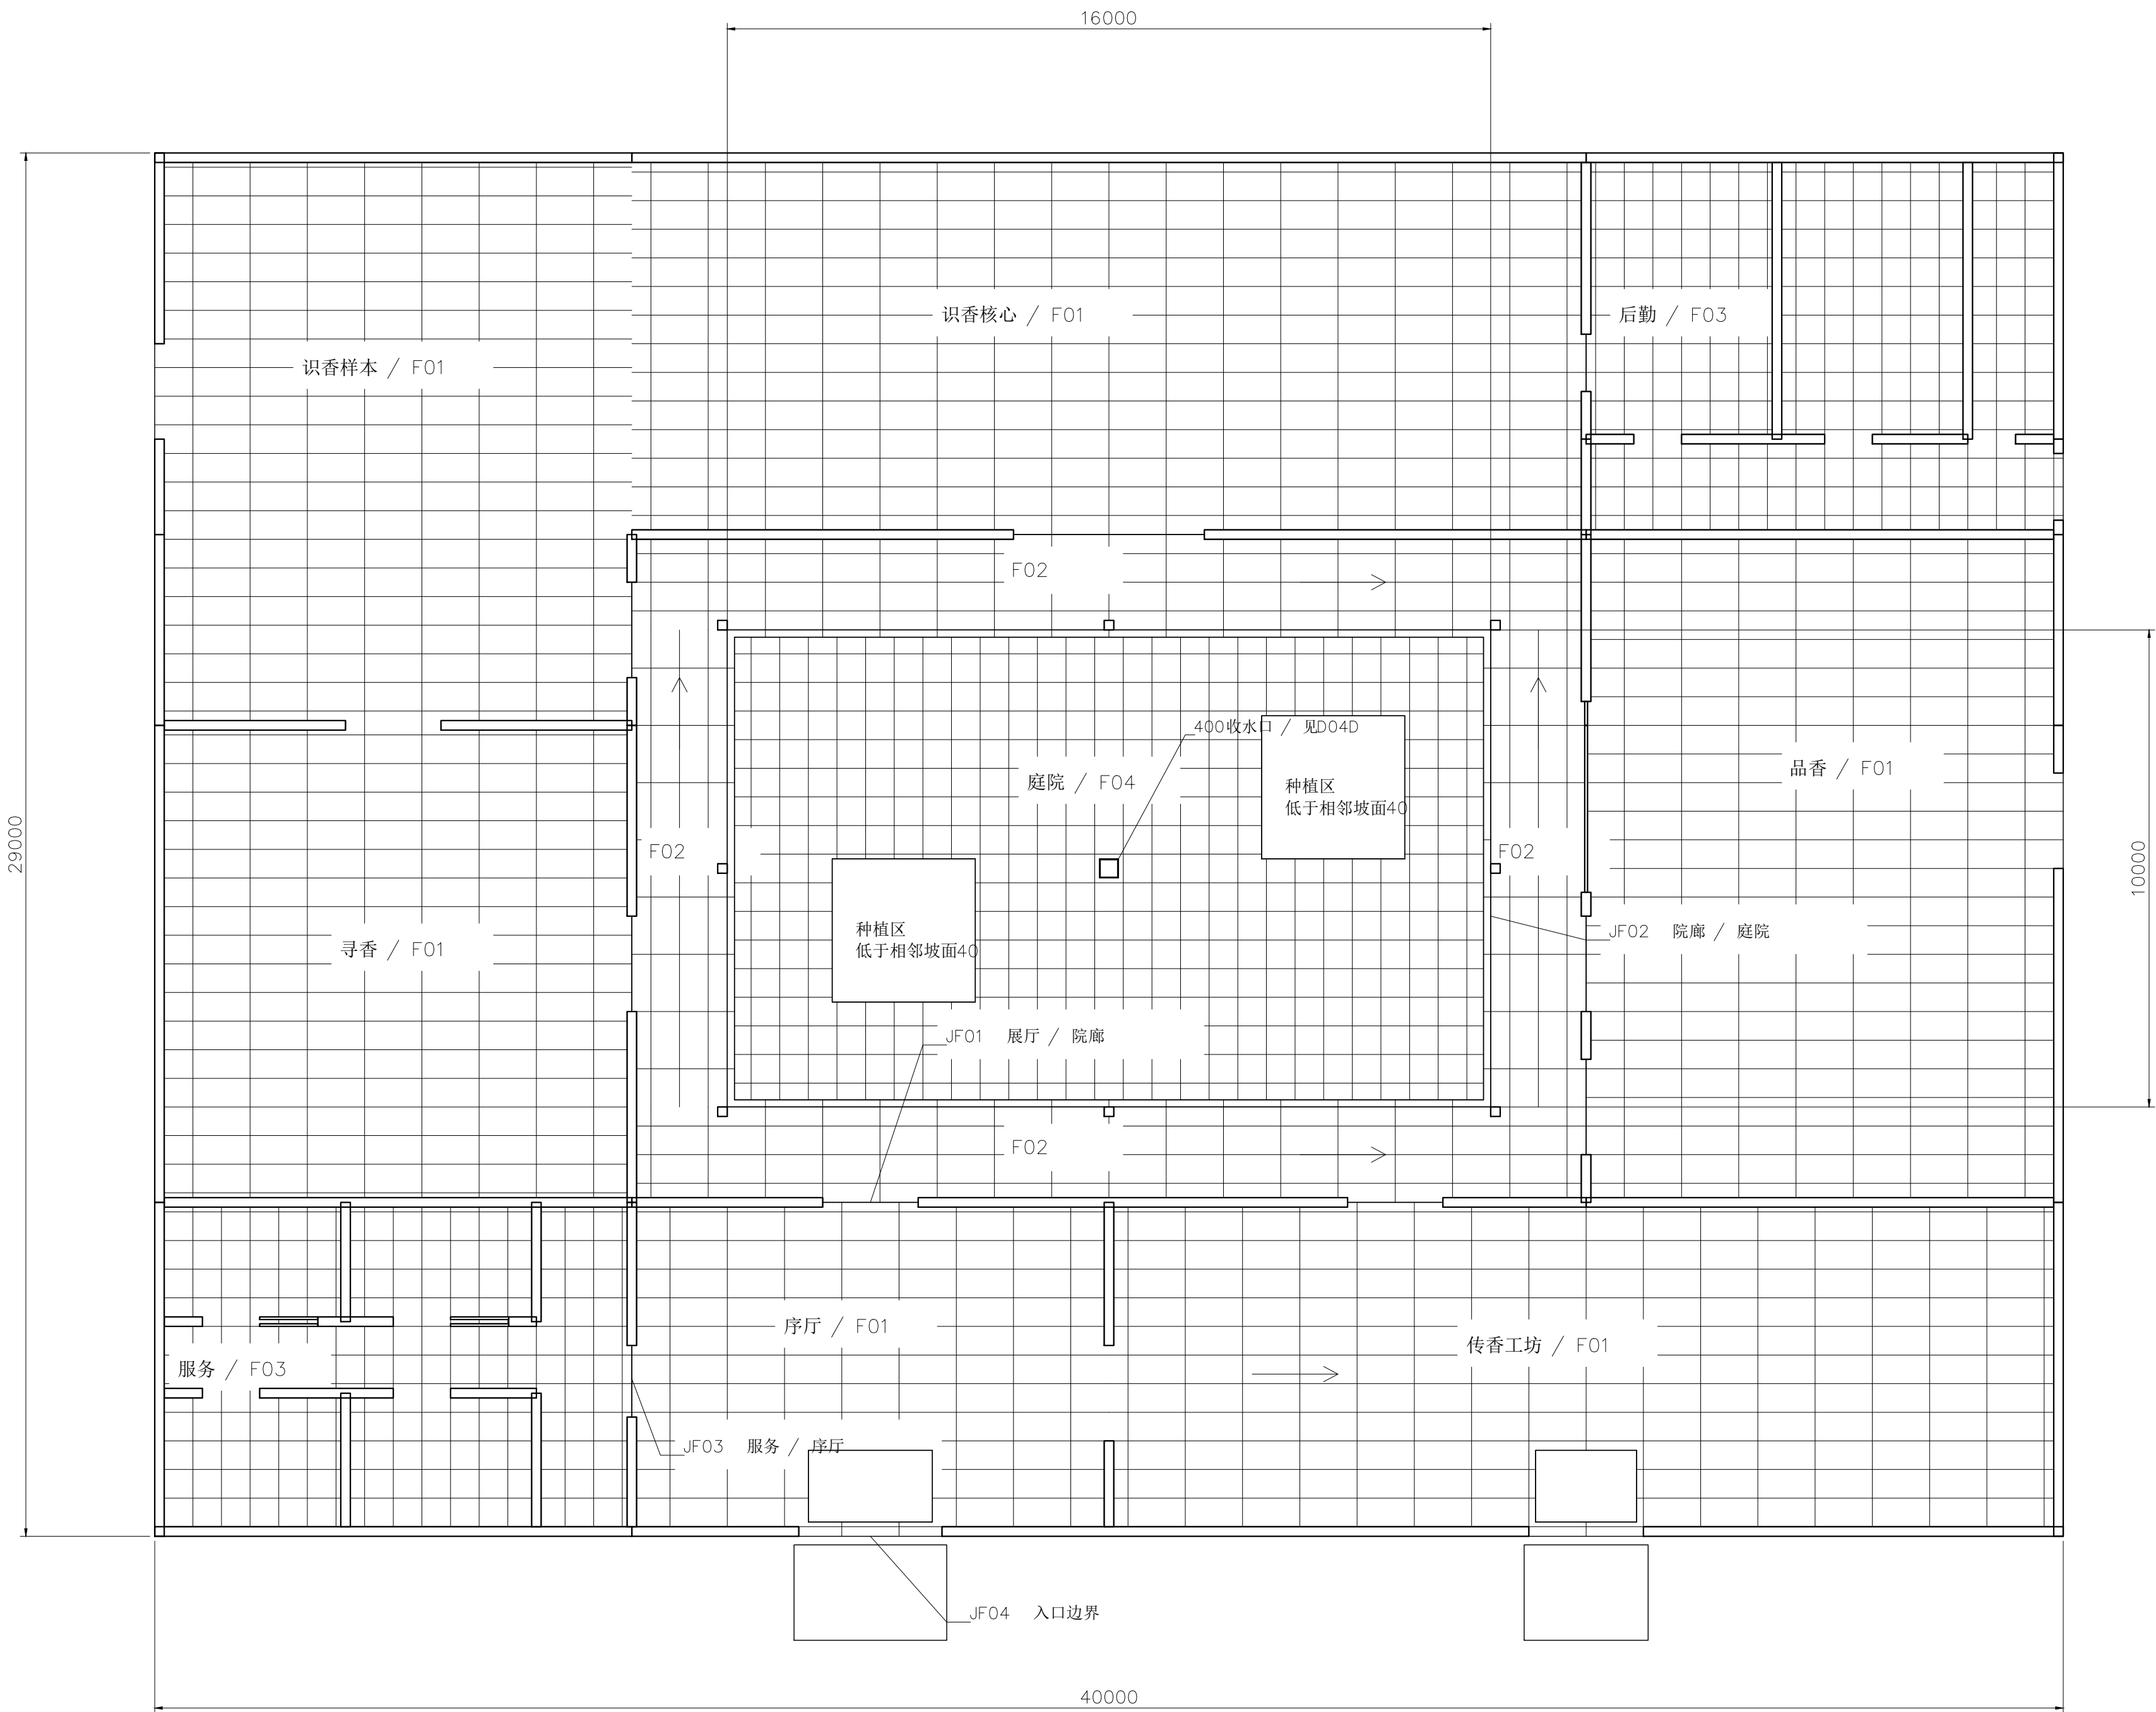

F01—F05材质范围含接缝：面积不作为采购用量。

湿区防滑、防水、庭院排水及入口内外高差需结合实际条件深化；本图不表示性能审查已完成。

材料与范围表

F01 展厅 / 暖灰哑光石感砖

模数1200×600，长边沿X向

本图投影净范围 691.82㎡

F02 院廊 / 灰米色哑光石感砖

模数1200×600，长边沿环廊

本图投影净范围 114.80㎡

F03 服务后勤 / 易清洁哑光砖

模数600×600，湿区另核性能

本图投影净范围 132.64㎡

F04 庭院 / 灰色户外石材

模数600×600，找坡与收水见D04D

本图投影净范围 134.13㎡

F05 庭院边缘 / 齐平石材收边

宽150，顶±0.000

本图投影净范围 7.71㎡

面积扣除墙、玻璃、廊柱：未扣门框、家具和设备，不作为采购用量。
扣除尘垫7.08㎡及收水口0.16㎡。
种植土18.00㎡；庭院总界160㎡。

完成面与材料交接

室内及F05边界±0.000；庭院中央收水口-0.060。

F05收边厚40；种植土低于相邻坡面40。

JF01/JF03：完成面齐平，材料界位于门口控制线。


JF02：保留150齐平收边；坡面至收水口见D04D。

JF04：局部门槛、除尘与截水见D07/J04。

JF01—JF03放大见D04B，入口条件见同页说明。


D04B 地面材料交接 / 方案接口放大

JF01 展厅F01 / 院廊F02

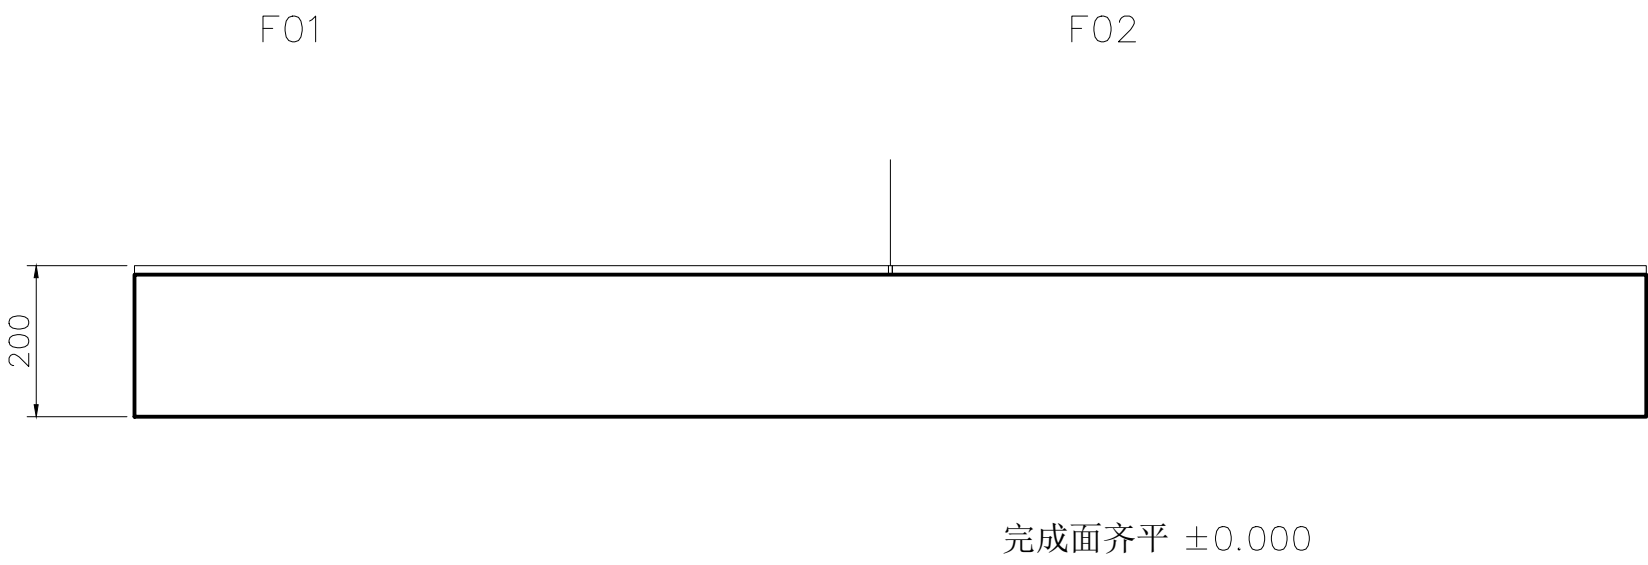


面层预留12，场界缝5；200总厚保持，非施工层次。

JF03 服务F03 / 序厅F01

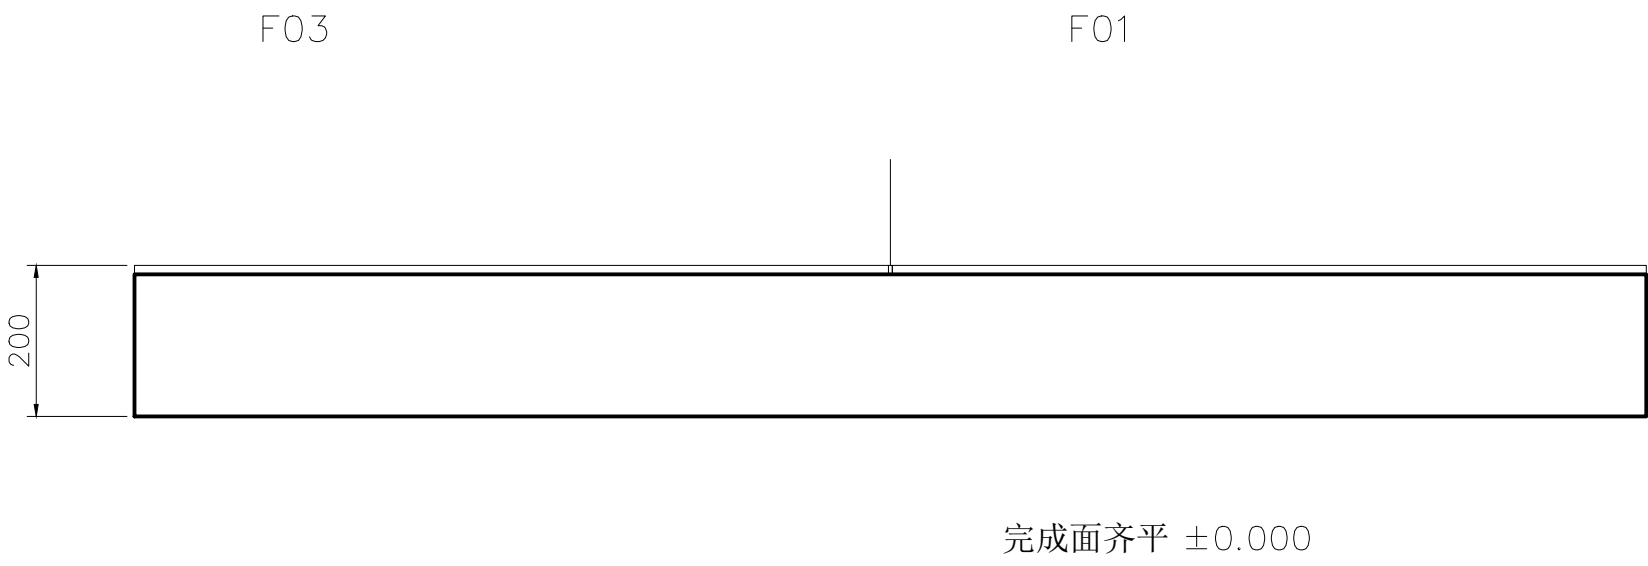

面层预留12，场界缝5；200总厚保持，非施工层次。

JF02 院廊 / 庭院齐平收边

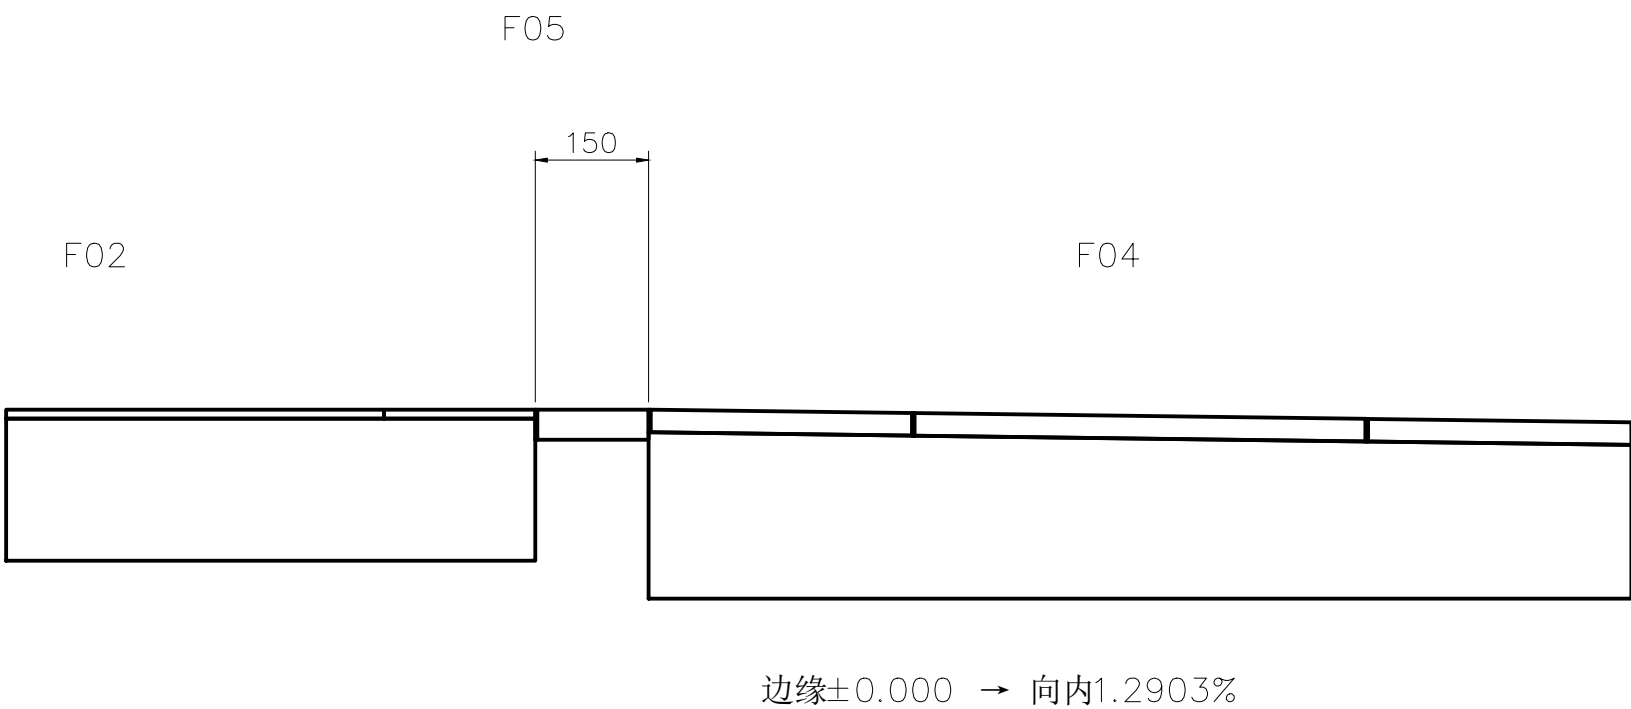

150宽边条保留；庭院面层30，基底至 -0.250 。

JF04 入口接口 / 详D07—J04

D01名义开口3000，位置沿用D03。

室内完成面 ± 0.000 ；外部场地标高暂无。

除尘垫齐平；门槛80长，外端下降3。

不把概念场地推定为已满足无障碍的实际地坪。

截水沟宽100；支管接续、门底和防水待核定。

D04C 铺装分格坐标 / 模数含接缝

每行X/Y的中间控制线即缝中心，首尾为场界。表内均为mm。

区域 / 材料	X：首界 / 首缝 / 递进 / 尾界	Y：首界 / 首缝 / 递进 / 尾界
序厅 F01	10000 / 10800 / 1200 / 20000	0 / 200 / 600 / 7000
寻香 F01	0 / 800 / 1200 / 10000	7000 / 7200 / 600 / 17000
识香·样本 F01	0 / 800 / 1200 / 10000	17000 / 17300 / 600 / 29000
识香·核心 F01	10000 / 10400 / 1200 / 30000	21000 / 21400 / 600 / 29000
品香 F01	30000 / 30800 / 1200 / 40000	7000 / 7400 / 600 / 21000
传香·工坊 F01	20000 / 20400 / 1200 / 40000	0 / 200 / 600 / 7000
公共服务 F03	0 / 200 / 600 / 10000	0 / 200 / 600 / 7000
后勤管理 F03	30000 / 30200 / 600 / 40000	21000 / 21400 / 600 / 29000
院廊S F02	10000 / 10400 / 1200 / 30000	7000 / 7400 / 600 / 9000
院廊N F02	10000 / 10400 / 1200 / 30000	19000 / 19400 / 600 / 21000
院廊W F02	10000 / 10400 / 600 / 12000	9000 / 9800 / 1200 / 19000
院廊E F02	28000 / 28400 / 600 / 30000	9000 / 9800 / 1200 / 19000
庭院 F04	12150 / 12500 / 600 / 27850	9150 / 9500 / 600 / 18850
庭院收边S F05	12000 / 12800 / 1200 / 28000	9000 / 无内缝 / - / 9150
庭院收边N F05	12000 / 12800 / 1200 / 28000	18850 / 无内缝 / - / 19000
庭院收边W F05	12000 / 无内缝 / - / 12150	9150 / 9800 / 1200 / 18850
庭院收边E F05	27850 / 无内缝 / - / 28000	9150 / 9800 / 1200 / 18850

F01/F02：1200×600；F02长边随廊向转90°。F03/F04：600×600；F05长向1200控制。

F01—F03内缝2；F04/F05内缝3；场界两侧各2.5，墙/柱边5。首尾裁切按实测墙边复核。


区域表列至首缝后按递进排布，末端回到尾界。

树池、柱边、收水口及找坡折线均有裁切；裁切数量不作为订货数量。

室内与边界±0.000；庭院四向找坡至-0.060，控制线为平面坐标，不代表面层共面。

D04D 庭院四向找坡与收水定位

1:50 / 坐标mm，标高m。四边齐平，中央低点；仅庭院局部排水方案。

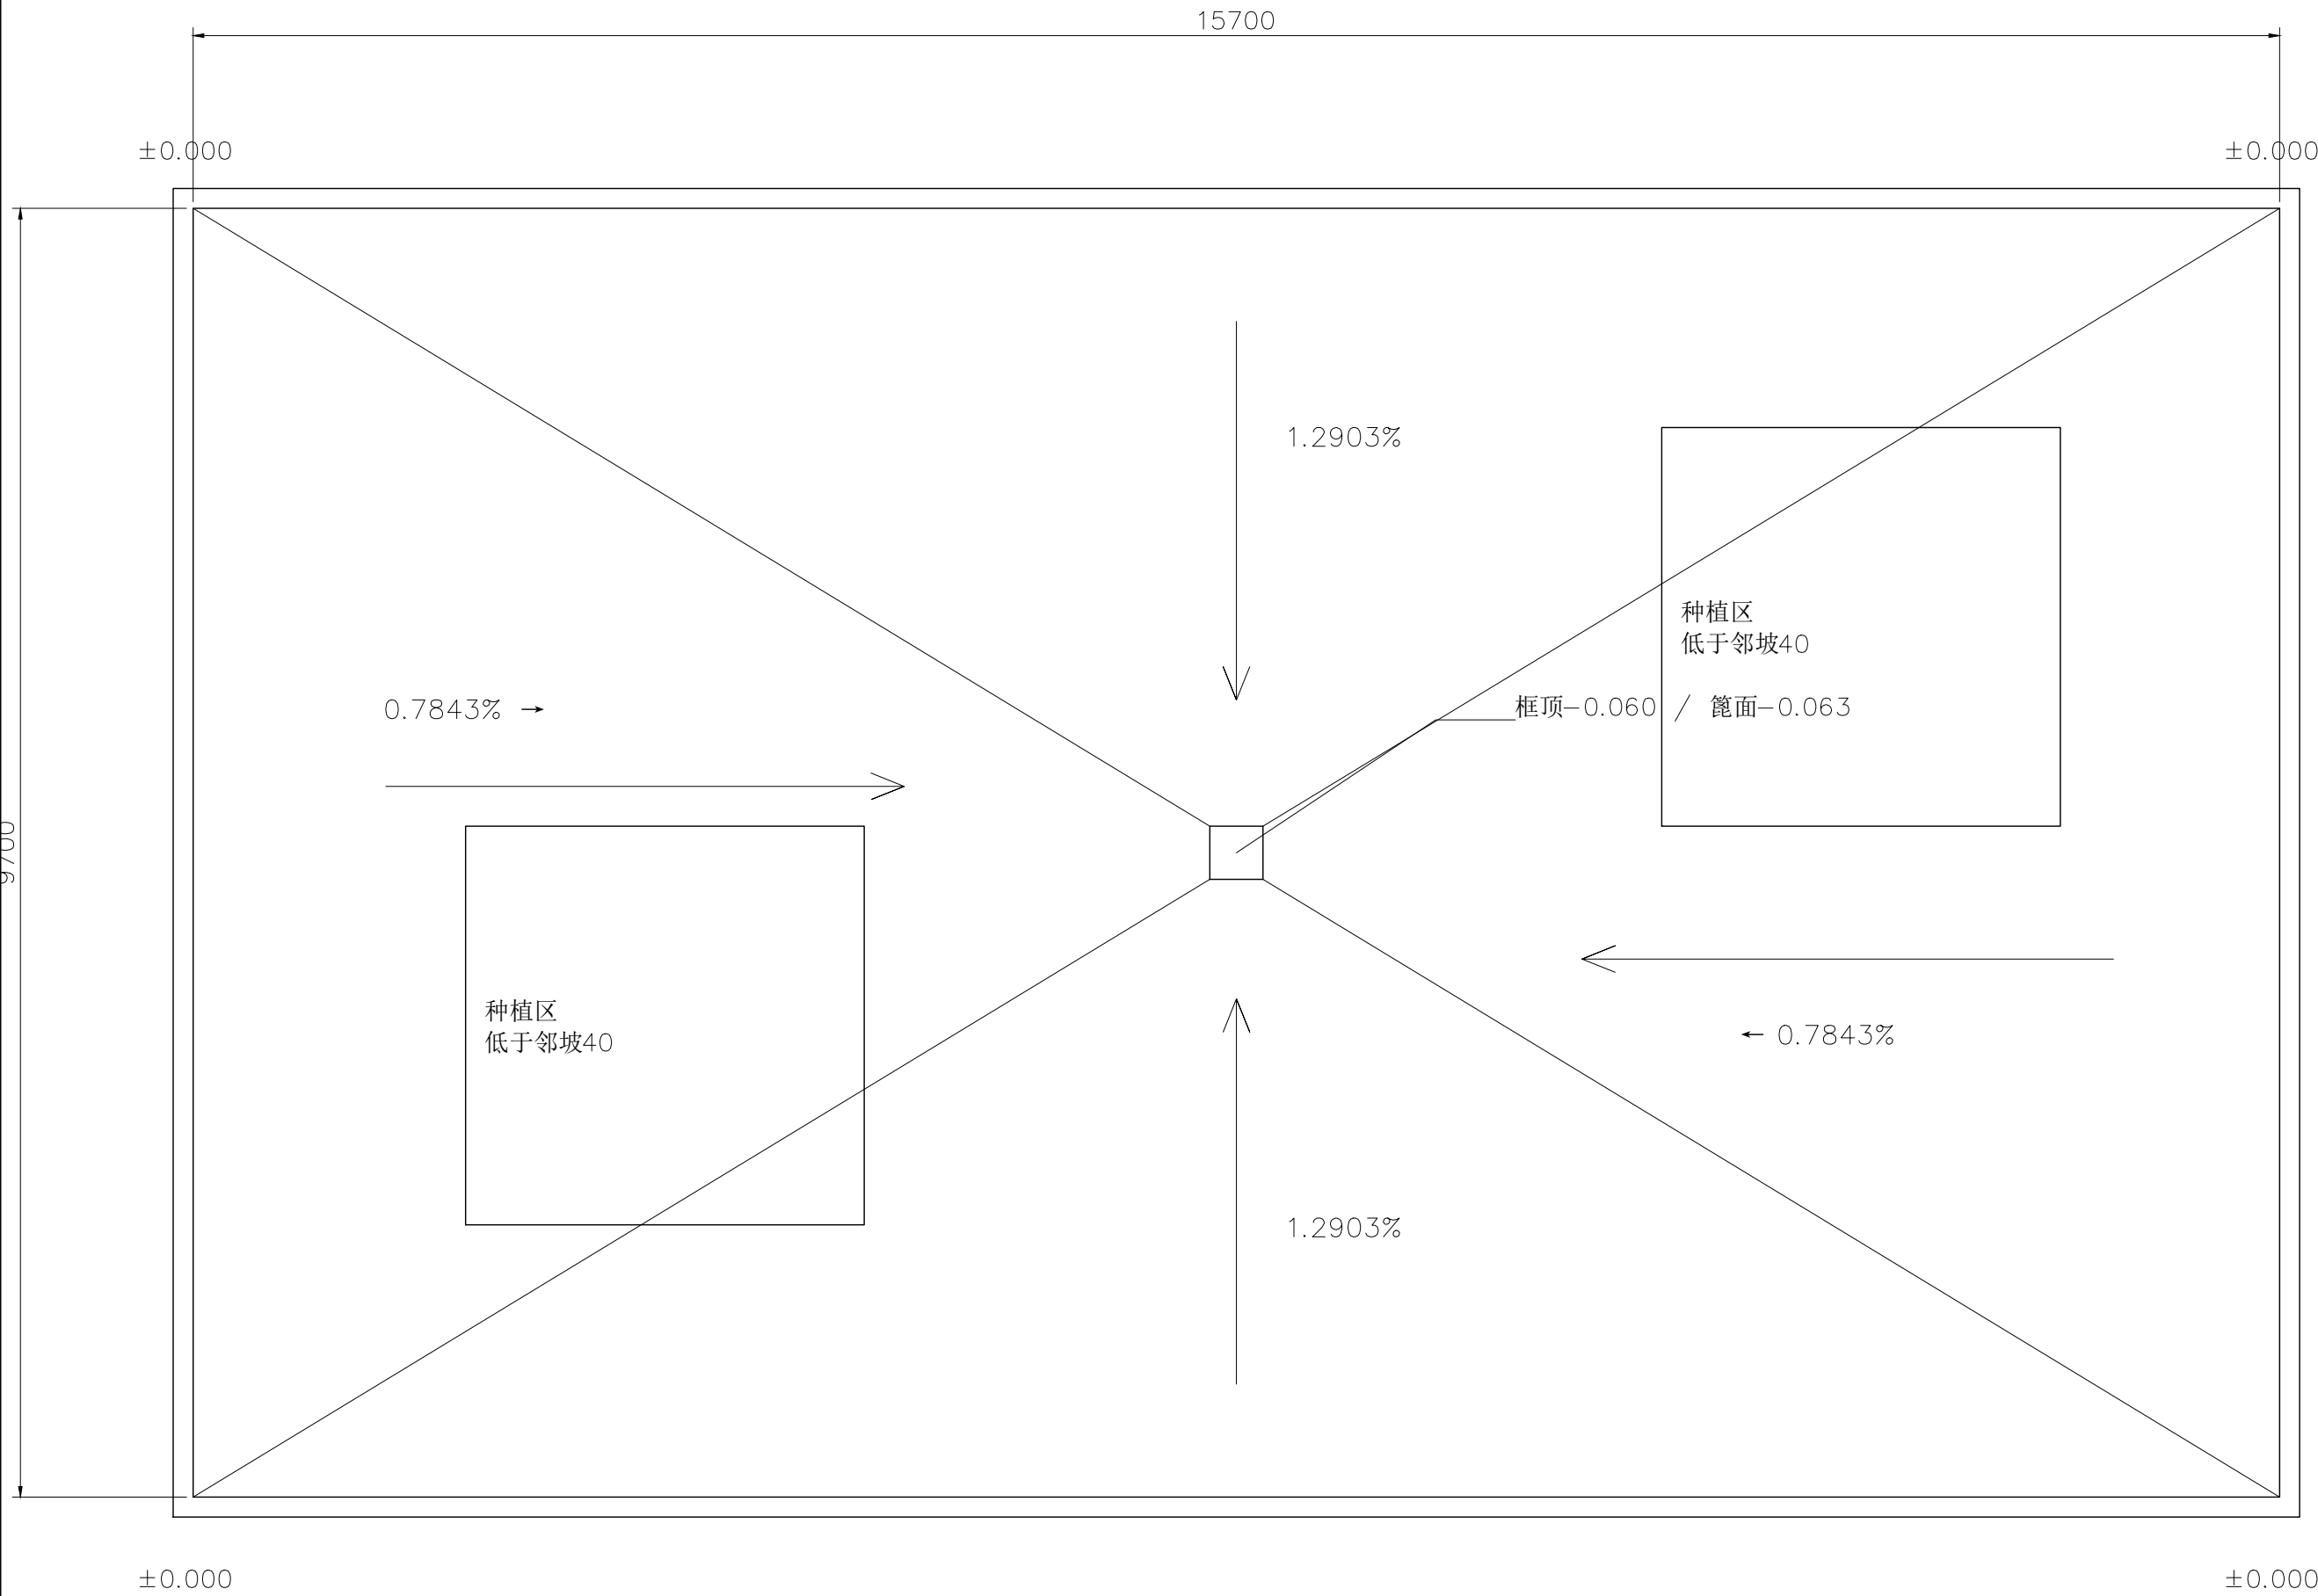

本图坡向表示几何高低关系；未包含暴雨量、汇水流量或土壤渗透计算。收水坑纵剖详D07/J03。

定位与维护

收水口中心X=20000 / Y=14000。

外包400×400；四周铺装连续降至框边。

四角至收水口角点为坡面交线，非伸缩缝。

平面板缝保持D04A/C控制；实体按坡面裁切。

篦条及开缝各约5，可拆篦体供清理。

主线沿X=20000向南，按1%落坡。

Y=-1500预留端内底-0.6532；

净100×100包络仅作空间协调，未选管。


种植区位置保留；种植土排水另行深化。

排水量、溢流、真实接驳与防水待专项核定。

D05A 天花与50组灯位 / 安装高度

吊顶下表面投影：坐标与朝向同建筑平面。灯位精确坐标见D05B。

吊顶边界已合并同标高补片；保留162处10×10安装穿孔；灯体及扩散板按实际包络绘制。

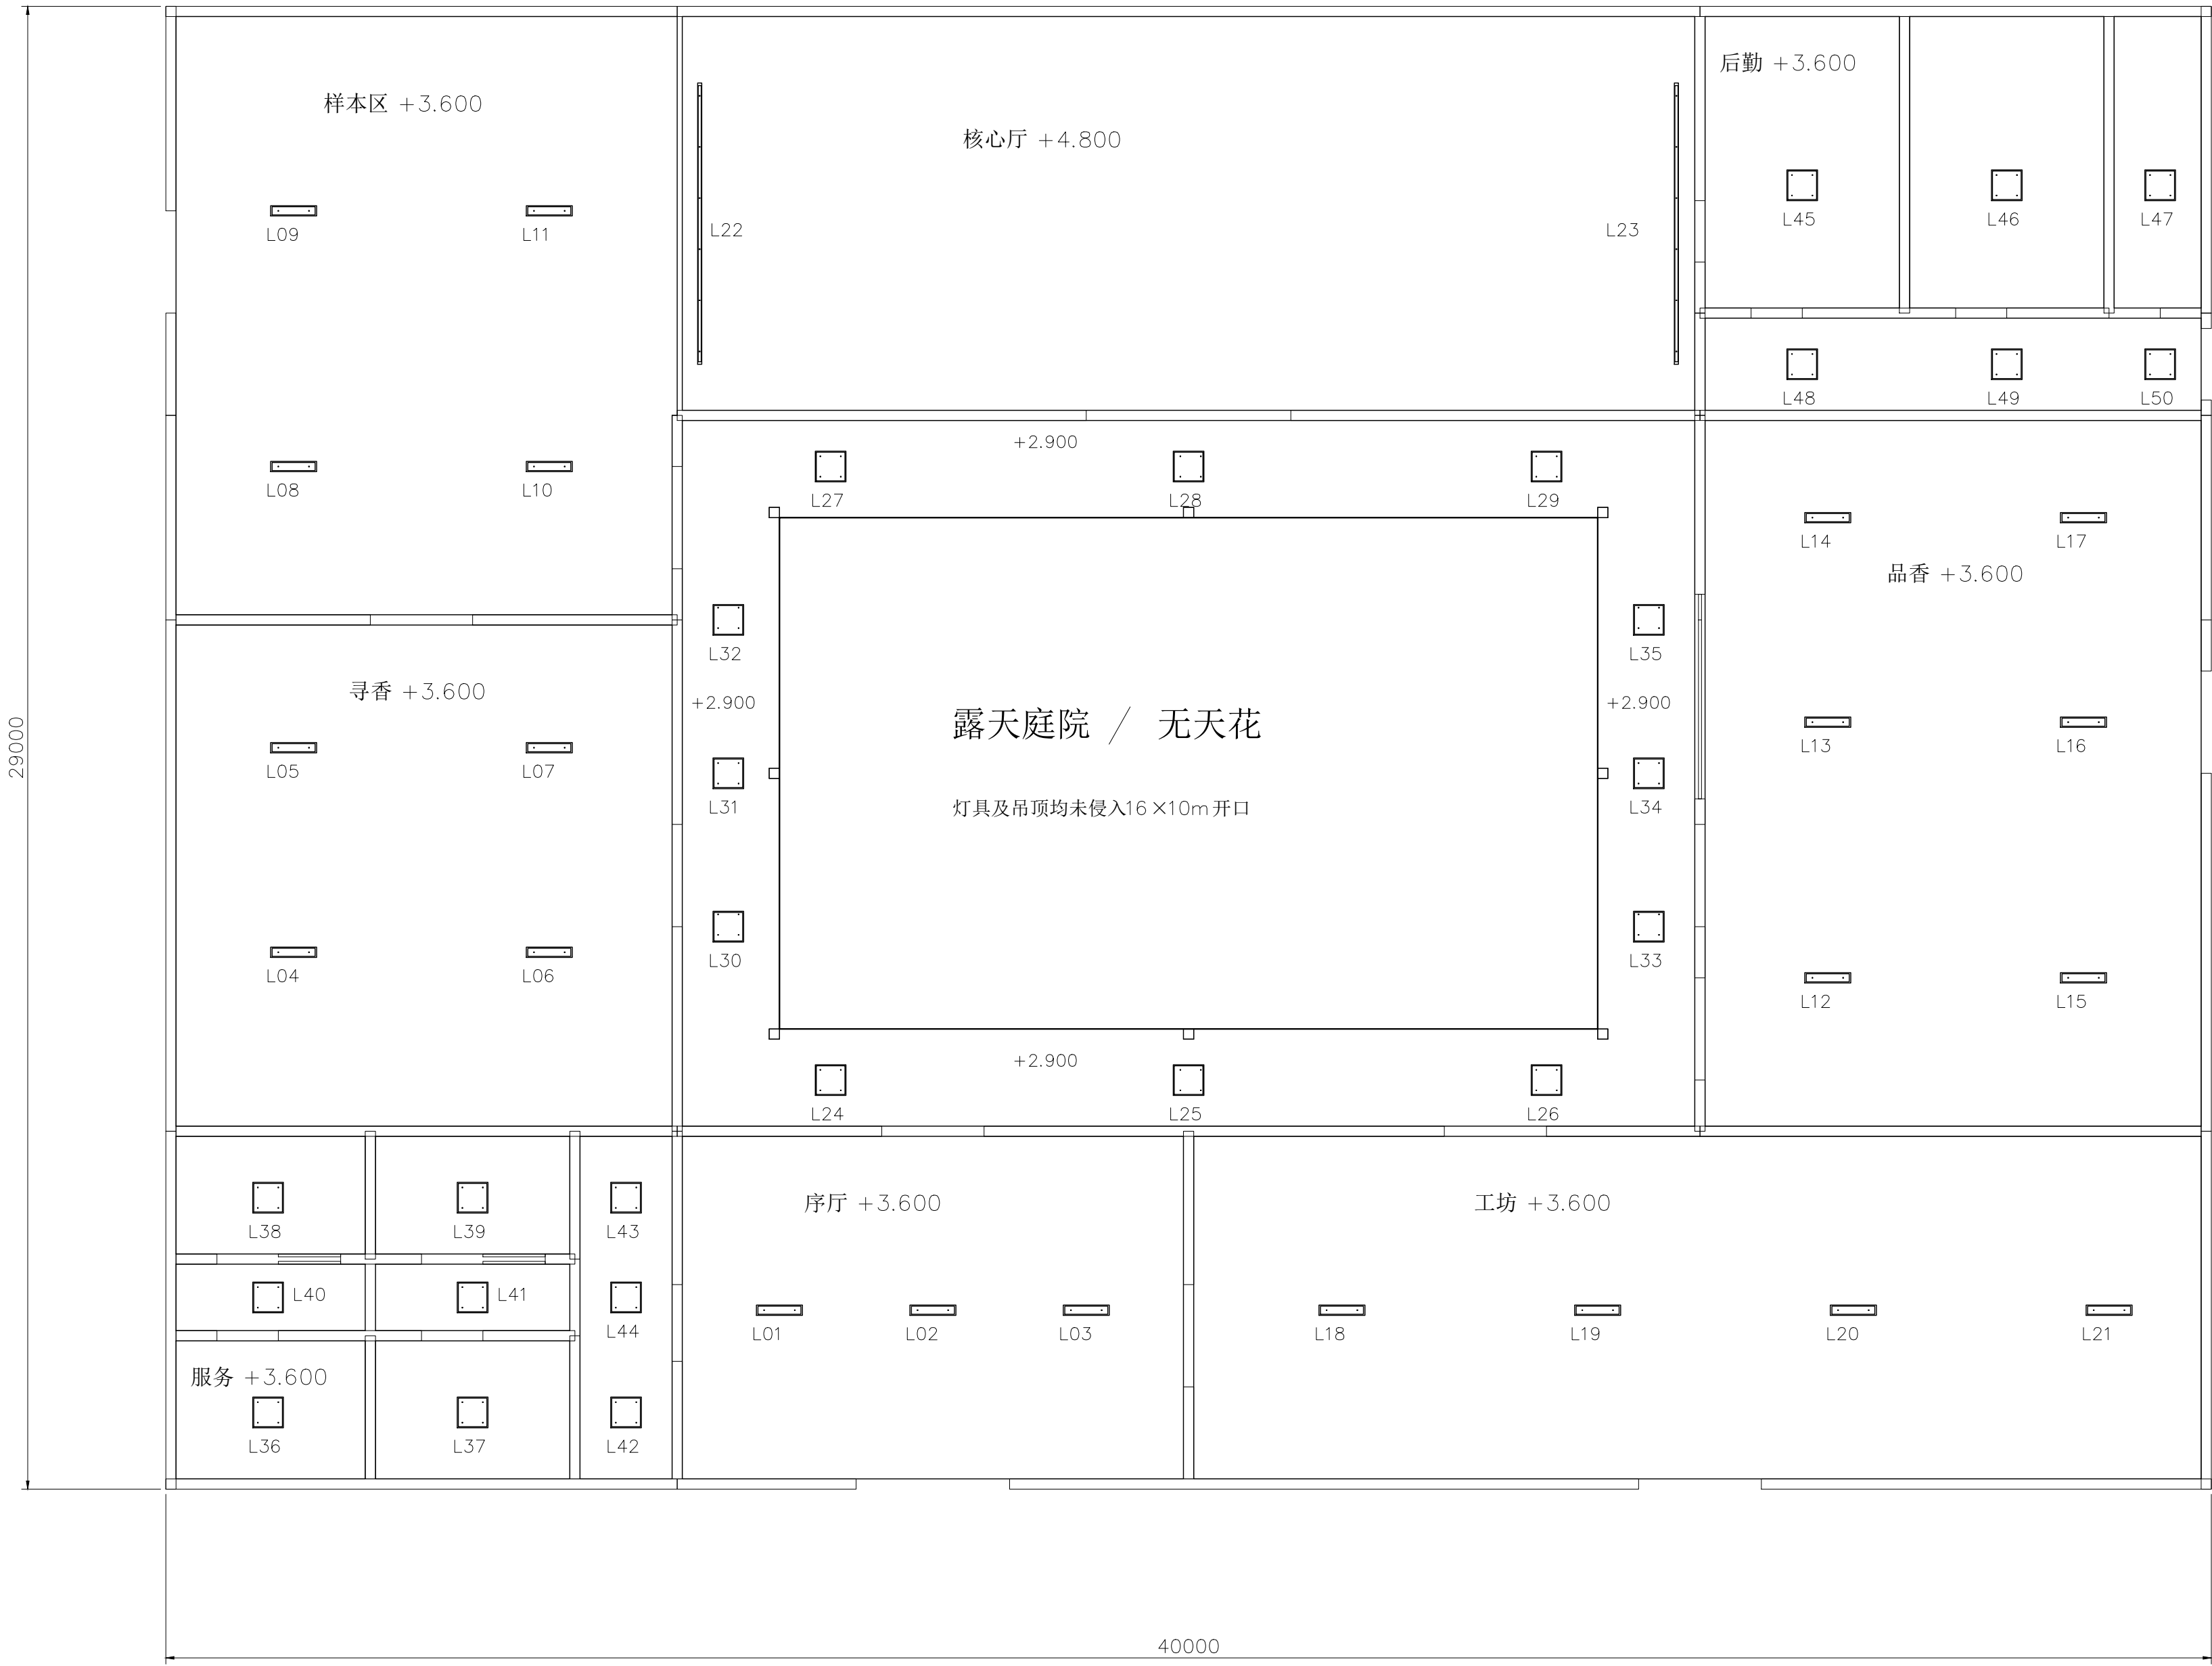

C01 普通区下皮+3.600；C02 环廊+2.900；C03 核心+4.800；吊顶厚度预留50mm。

风口、喷淋、检修口与应急照明待专项协调；图中发光面不代表产品采购或照明性能达标。

灯具图例 / 几何尺寸

T01 条形灯体

900×200×50 mm

序厅3组；展区18组

T02 核心侧向长条

80×5500×60 mm

核心厅2组；发光面长5400

T03 方形灯体

600×600×30 mm

环廊12组；服务后勤15组

吊项下皮 / 扩散板最低点（m）

序厅：+3.600 / +3.442

寻香、样本、品香、工坊：+3.600 / +3.492

环廊：+2.900 / +2.852

公共服务及后勤：+3.600 / +3.552

核心厅：+4.800 / +4.712

灯体上方安装间隙10—100mm；
50组、162处连接至屋面体块，
穿孔10×10，局部剖面见D05C。

50组为空间灯，不含10处柜内灯。
柜内灯见D12B；照度、眩光、配光、
功率、色温及电气回路尚未核定。

D05B 50组灯位与安装高度表

X/Y为灯体中心；Z均为相对室内地坪的绝对标高。数值单位mm。型号、功率与配光尚未指定。

编号	空间	中心X	中心Y	灯体W×D	灯体底	扩散板底	吊顶底	上方间隙
L01	序厅	12000	3500	900×200	3450	3442	3600	100
L02	序厅	15000	3500	900×200	3450	3442	3600	100
L03	序厅	18000	3500	900×200	3450	3442	3600	100
L04	寻香	2500	10500	900×200	3500	3492	3600	50
L05	寻香	2500	14500	900×200	3500	3492	3600	50
L06	寻香	7500	10500	900×200	3500	3492	3600	50
L07	寻香	7500	14500	900×200	3500	3492	3600	50
L08	样本	2500	20000	900×200	3500	3492	3600	50
L09	样本	2500	25000	900×200	3500	3492	3600	50
L10	样本	7500	20000	900×200	3500	3492	3600	50
L11	样本	7500	25000	900×200	3500	3492	3600	50
L12	品香	32500	10000	900×200	3500	3492	3600	50
L13	品香	32500	15000	900×200	3500	3492	3600	50
L14	品香	32500	19000	900×200	3500	3492	3600	50
L15	品香	37500	10000	900×200	3500	3492	3600	50
L16	品香	37500	15000	900×200	3500	3492	3600	50
L17	品香	37500	19000	900×200	3500	3492	3600	50
L18	工坊	23000	3500	900×200	3500	3492	3600	50
L19	工坊	28000	3500	900×200	3500	3492	3600	50
L20	工坊	33000	3500	900×200	3500	3492	3600	50
L21	工坊	38000	3500	900×200	3500	3492	3600	50
L22	核心	10440	24750	80×5500	4720	4712	4800	20
L23	核心	29540	24750	80×5500	4720	4712	4800	20
L24	环廊	13000	8000	600×600	2860	2852	2900	10
L25	环廊	20000	8000	600×600	2860	2852	2900	10

编号	空间	中心X	中心Y	灯体W×D	灯体底	扩散板底	吊顶底	上方间隙
L26	环廊	27000	8000	600×600	2860	2852	2900	10
L27	环廊	13000	20000	600×600	2860	2852	2900	10
L28	环廊	20000	20000	600×600	2860	2852	2900	10
L29	环廊	27000	20000	600×600	2860	2852	2900	10
L30	环廊	11000	11000	600×600	2860	2852	2900	10
L31	环廊	11000	14000	600×600	2860	2852	2900	10
L32	环廊	11000	17000	600×600	2860	2852	2900	10
L33	环廊	29000	11000	600×600	2860	2852	2900	10
L34	环廊	29000	14000	600×600	2860	2852	2900	10
L35	环廊	29000	17000	600×600	2860	2852	2900	10
L36	服务	2000	1500	600×600	3560	3552	3600	10
L37	服务	6000	1500	600×600	3560	3552	3600	10
L38	服务	2000	5700	600×600	3560	3552	3600	10
L39	服务	6000	5700	600×600	3560	3552	3600	10
L40	服务	2000	3750	600×600	3560	3552	3600	10
L41	服务	6000	3750	600×600	3560	3552	3600	10
L42	服务	9000	1500	600×600	3560	3552	3600	10
L43	服务	9000	5700	600×600	3560	3552	3600	10
L44	服务	9000	3750	600×600	3560	3552	3600	10
L45	后勤	32000	25500	600×600	3560	3552	3600	10
L46	后勤	36000	25500	600×600	3560	3552	3600	10
L47	后勤	39000	25500	600×600	3560	3552	3600	10
L48	后勤	32000	22000	600×600	3560	3552	3600	10
L49	后勤	36000	22000	600×600	3560	3552	3600	10
L50	后勤	39000	22000	600×600	3560	3552	3600	10

灯体上方间隙 = 吊顶下皮 - 灯体底 - 灯体厚度。灯体与扩散板标高分别列示。

灯位编号L01—L50：灯体、扩散板和吊顶按本表对应。

数量校核：序厅3 + 寻香4 + 样本4 + 品香6 + 工坊4 + 核心2 + 环廊12 + 服务9 + 后勤6 = 50组。

吊顶分三种标高，预留162处安装穿孔；50灯体及50扩散板。

灯具电功率、配光与电气回路须按实际产品核定。

另有五柜10处局部照明，随柜体安装；位置与几何见D12B，不计入本页50组空间灯。

D05C L28灯具安装路径 / 1:5

截面Y=19800；左图X/Z与全馆坐标一致。

50组灯具，162处连接点。

T01条形：每组2点；核心长条：每组6点；方形：每组4点。

每点为：灯体连接片、下接杆、孔口盖片、上接杆、屋面连接片。


下片30×30×3；盖片30×30×3；上片50×50×4。

接杆以6×6方形包络表达；吊顶10×10孔，每边净余2。

孔位避开格栅；局部侧向移位须与现场安装尺寸协调。

上接杆终止于屋面连接片，连接片顶与屋面体块底相接。


几何连通不证明承载合格；屋面承托、锚固、截面及线缆待专项。

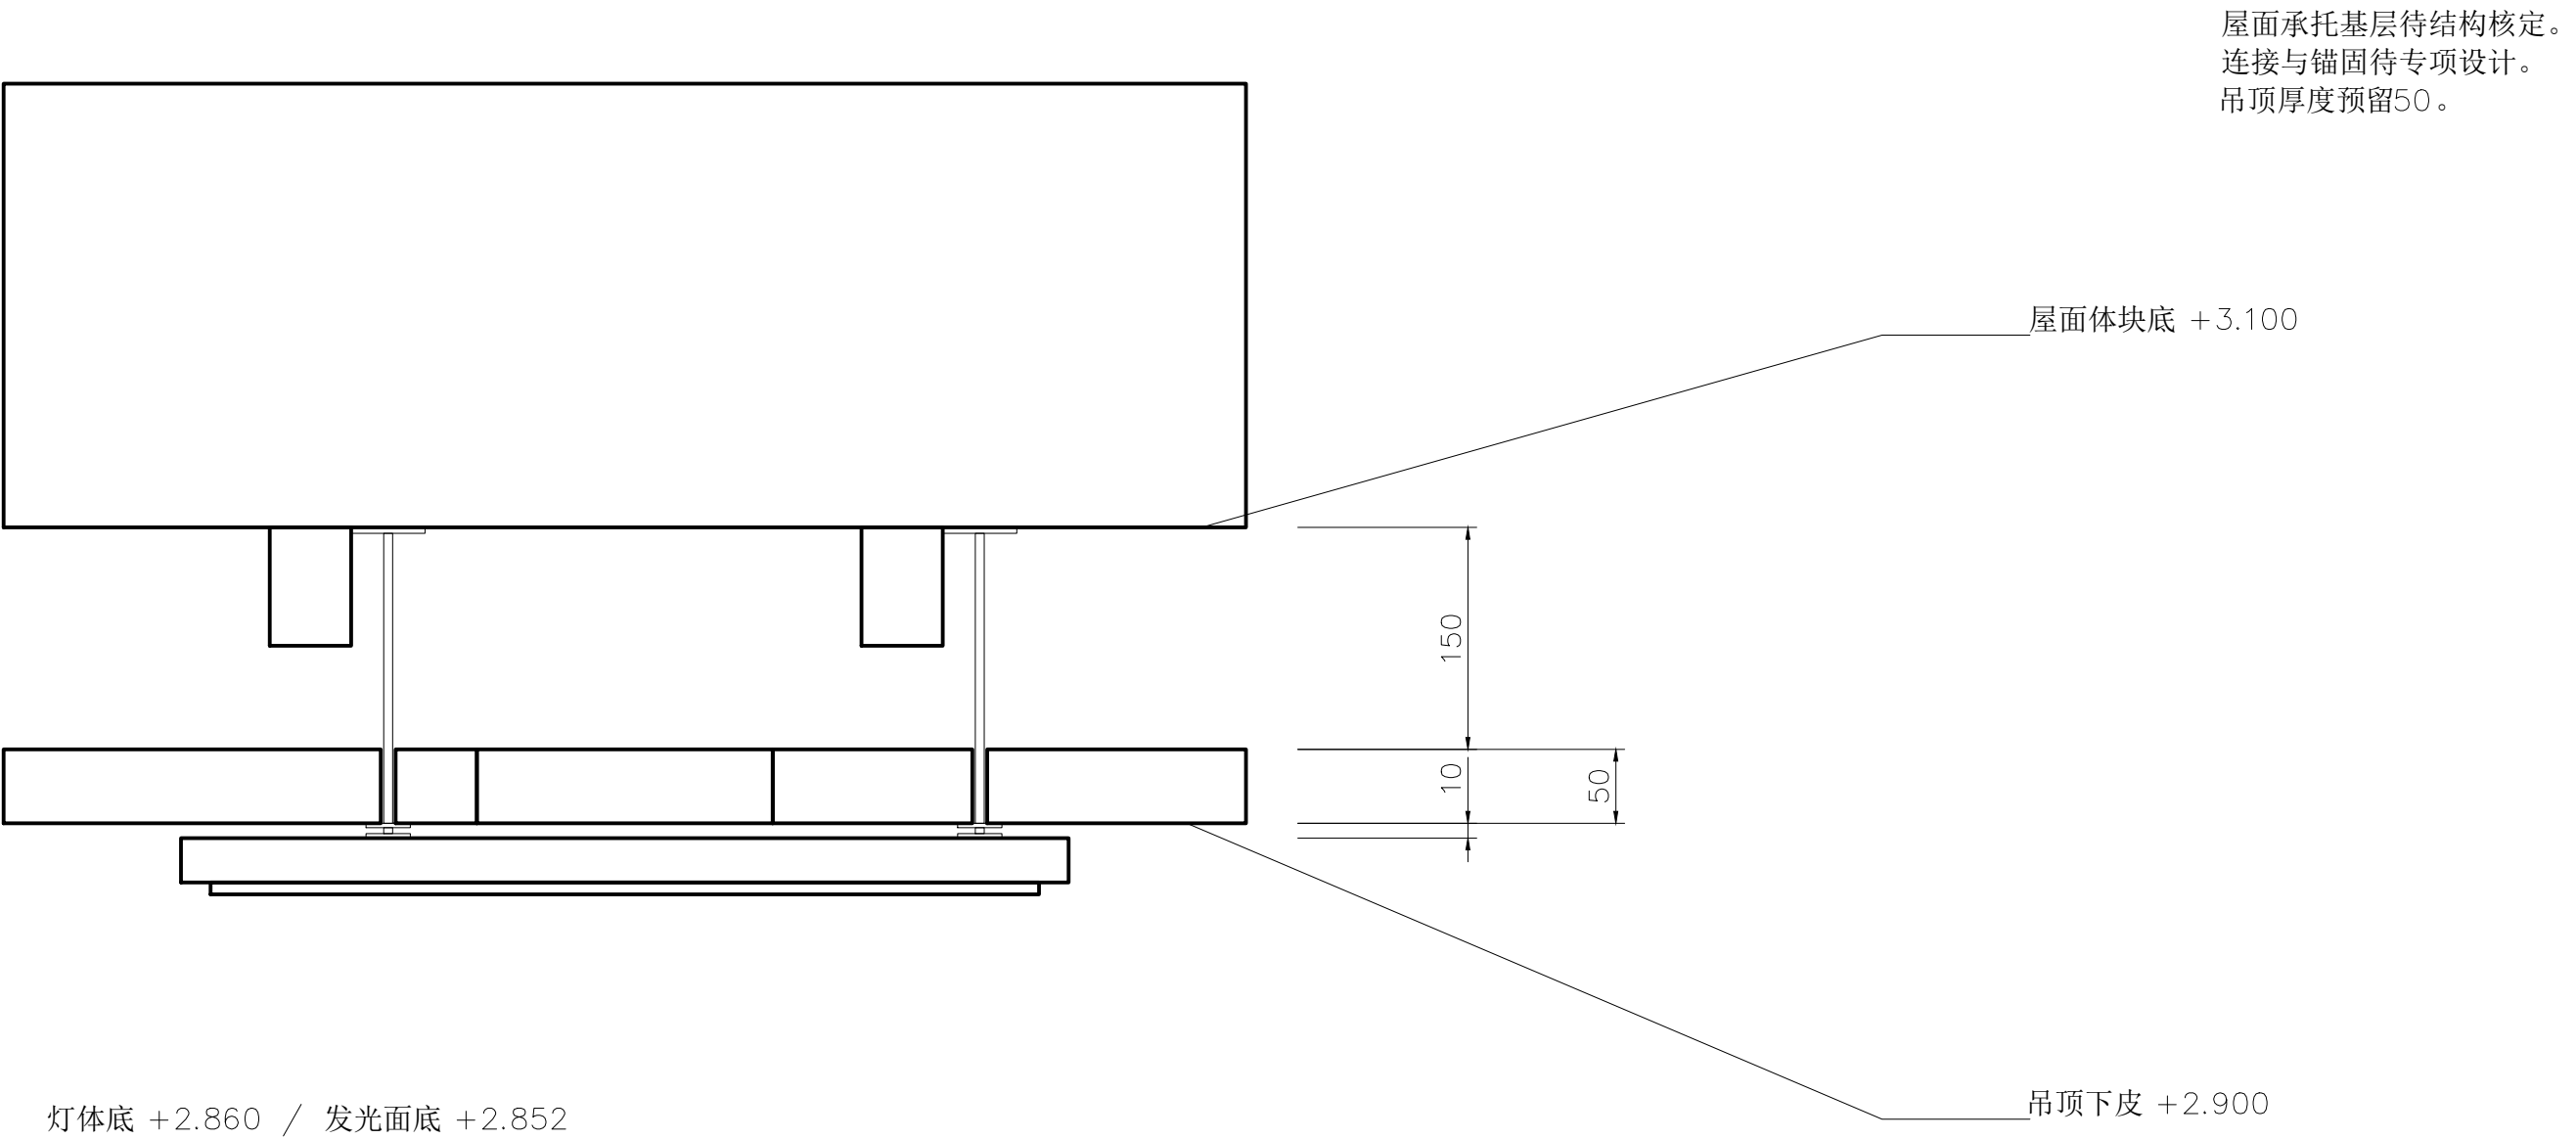

D06 建筑四向立面


建筑外形正交投影：门窗表为名义开口，材质编号与节点统一。

南立面 / 主入口、工坊入口

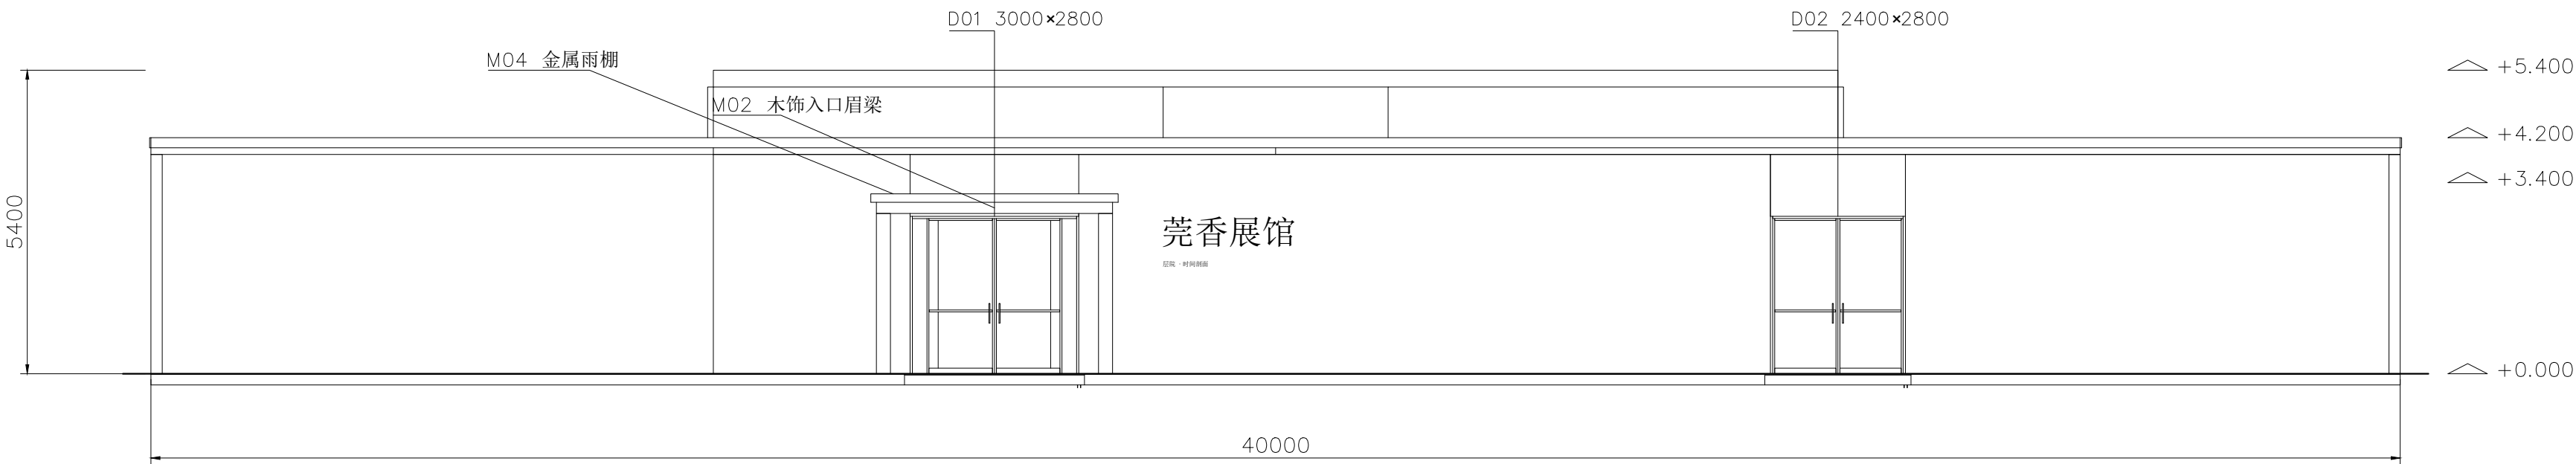


M01 暖灰墙面 M03 灰绿屋面 M04 金属框件 M05 透明玻璃

北立面

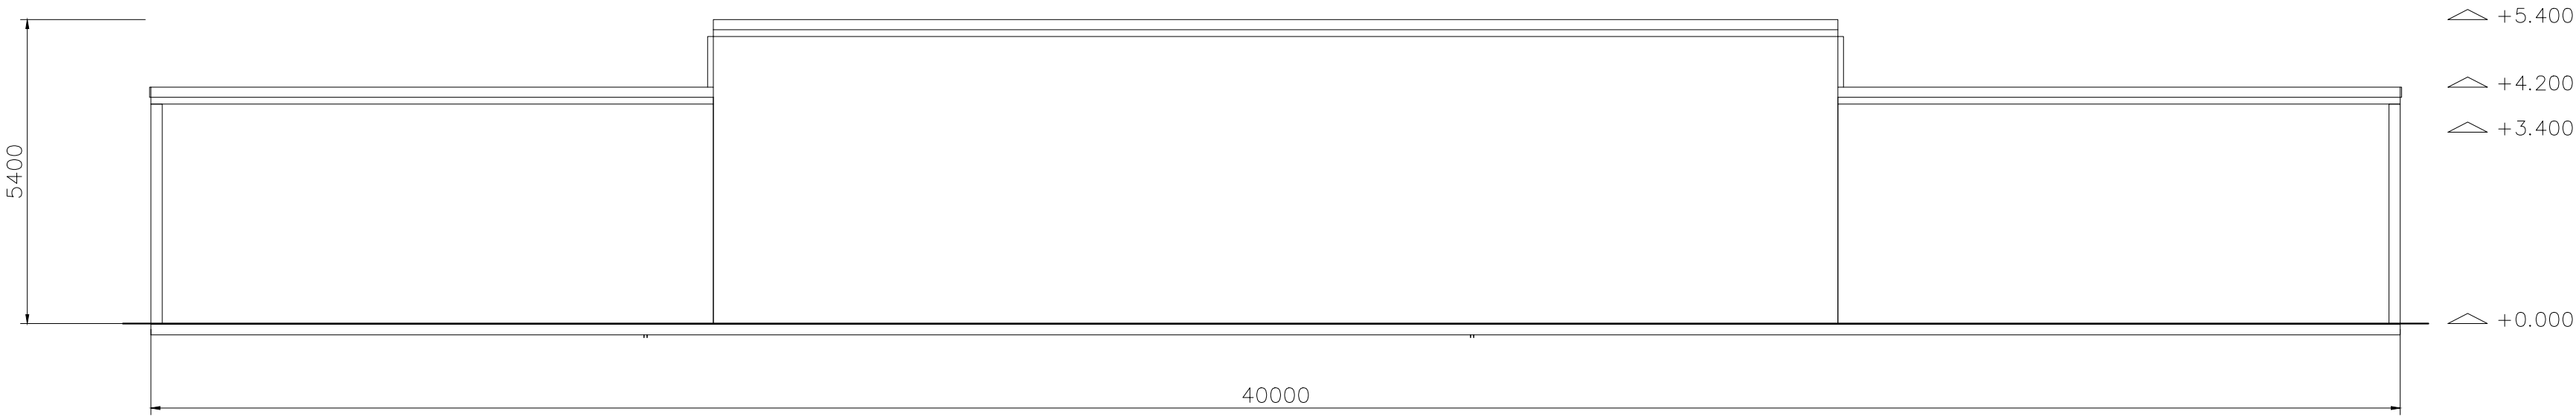


M01 暖灰墙面 M03 灰绿屋面 M04 金属框件 M05 透明玻璃

东立面 / 品香、后勤入口

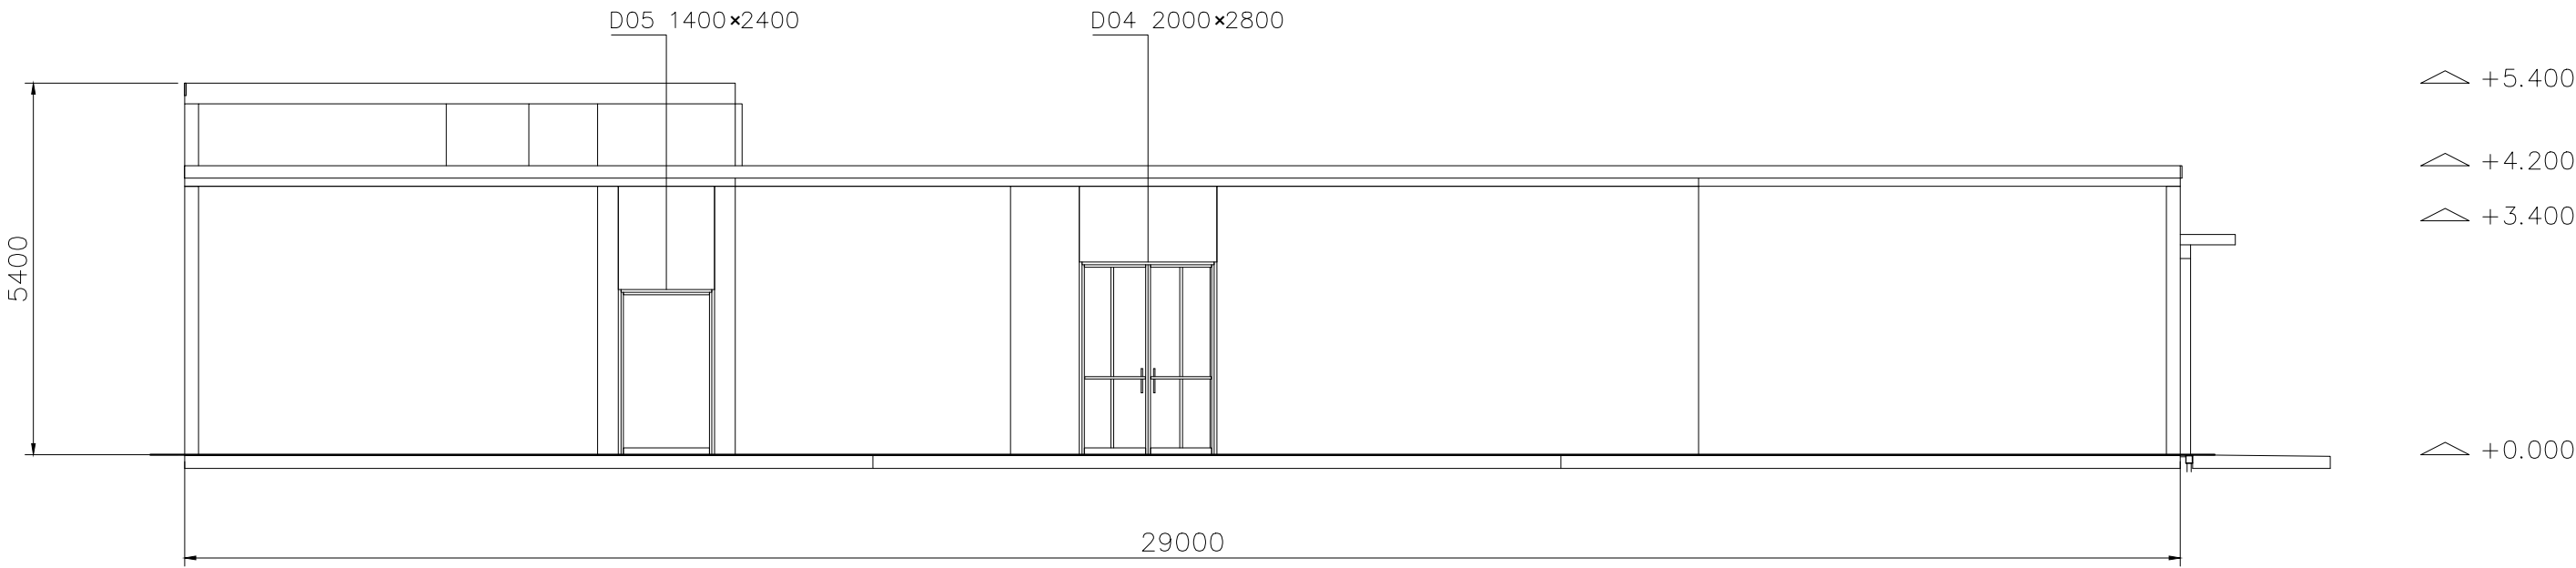

M01 暖灰墙面 M03 灰绿屋面 M04 金属框件 M05 透明玻璃

西立面 / 识香入口

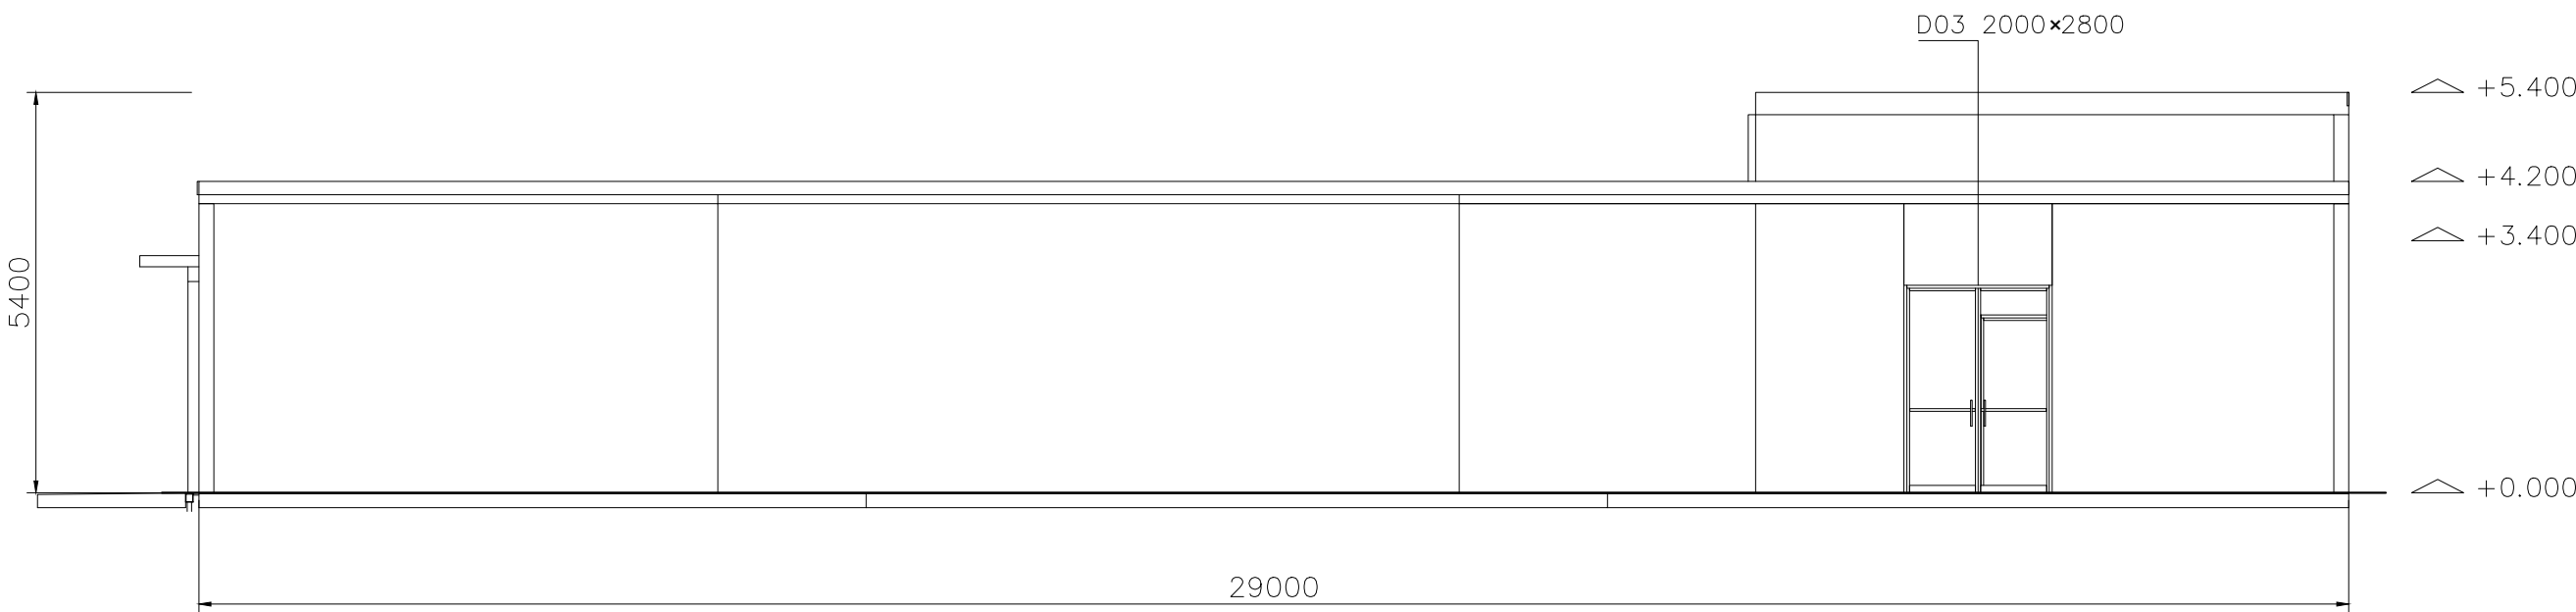

M01 暖灰墙面 M03 灰绿屋面 M04 金属框件 M05 透明玻璃

节点引用：J01屋面/墙顶、J02院落/庭院见D07；D01入口雨棚与招牌位置见南立面。

+3.400 / +4.200 / +5.400为屋面顶控制值；吊顶下皮与灯具下缘分别在D07/D05注明。

方案设计：保温、防水、结构与门窗产品需专项深化。

南入口平台顶-0.003至-0.023，1%找坡；截水与门槛见D07/J04。地坪体块不代表基础。

材料索引

- M01 灰泥 / 暖灰
- M02 木饰 / 暖木
- M03 屋面 / 灰绿
- M04 金属 / 细框
- M05 玻璃 / 透明

外部门洞名义尺寸 / mm


- D01 3000 × 2800
- D02 2400 × 2800
- D03 2000 × 2800
- D04 2000 × 2800
- D05 1400 × 2400

室内门/玻璃界面见D03B。
门框与五金另影响完成净宽。
门扇按闭合状态表达。


D07 建筑剖面 / 后方投影与净空层次

与D03A剖切线对应。粗线为切到构件；细线为视向后方投影。

A-A x=15000 / 向西看

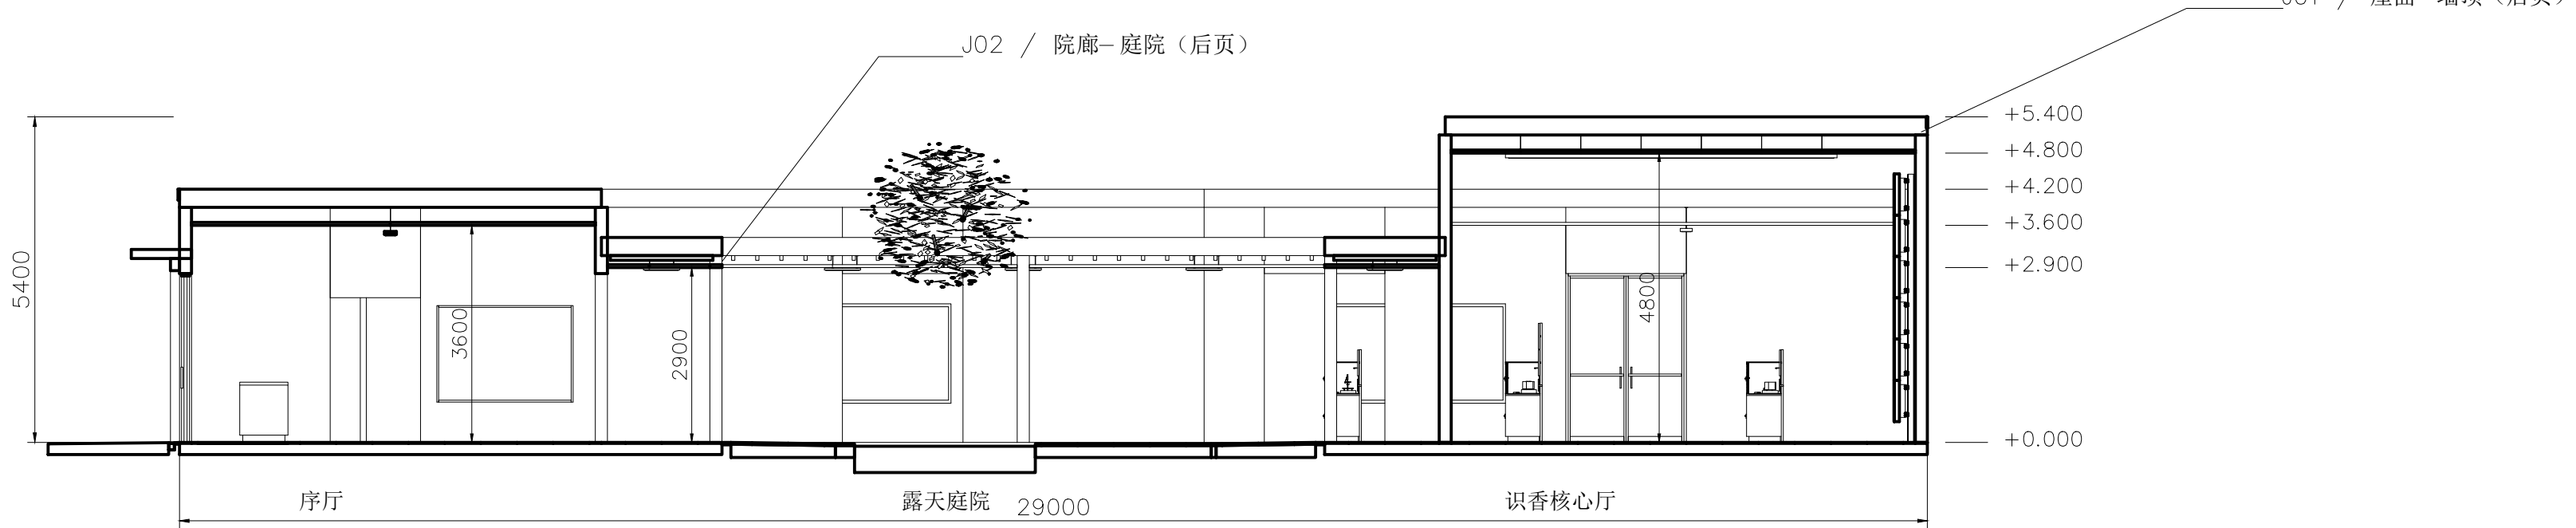

B-B y=14000 / 向北看

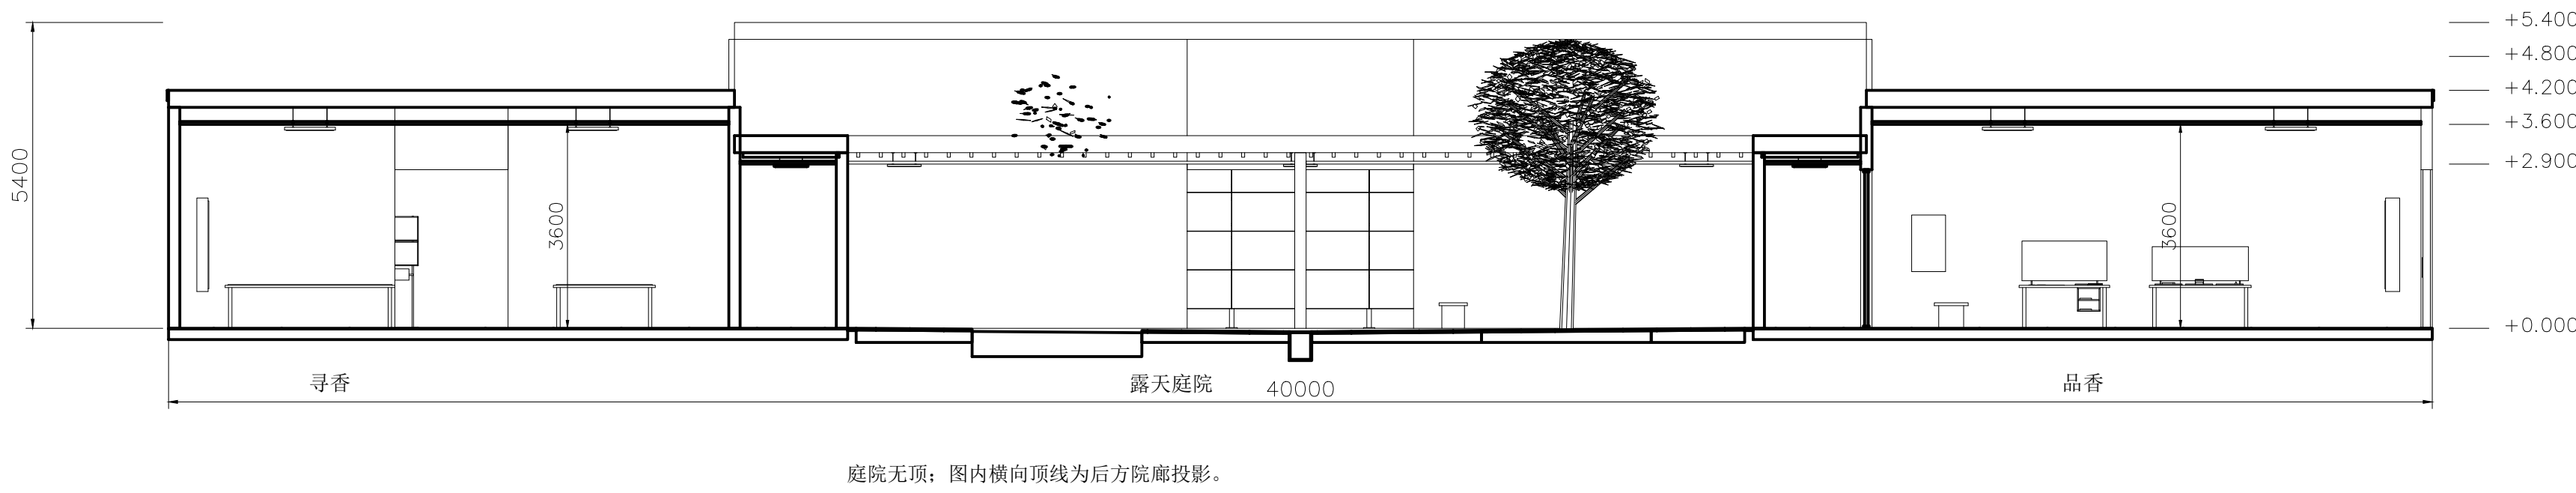

J03庭院中央收水口与J04入口接口详图见后页。

吊顶、屋面及墙体为方案构造；承重、防水、保温、排水和五金需专项深化。

图例：粗线—剖切轮廓；细线—可见投影；标高单位m，尺寸单位mm。

标高与净空口径

±0.000：建筑室内地坪基准。

一般展区：吊顶下皮+3.600。

环廊：吊顶下皮+2.900。

核心厅：吊顶下皮+4.800。

屋面顶：+3.400 / +4.200 / +5.400。

竖向尺寸标至吊顶下皮，灯具另有下挂。

灯具最低点与安装高度见D05深化。

剖面线图的表达范围

粗线表示剖切轮廓，细线表示可见投影。


玻璃保留透明轮廓及后方可见陈设。

地坪以下只绘剖切，不绘隐蔽后投影。

曲面按外轮廓及主要折角表达。


材料与接口为方案关系，非施工做法。

剖切索引 / 1:400

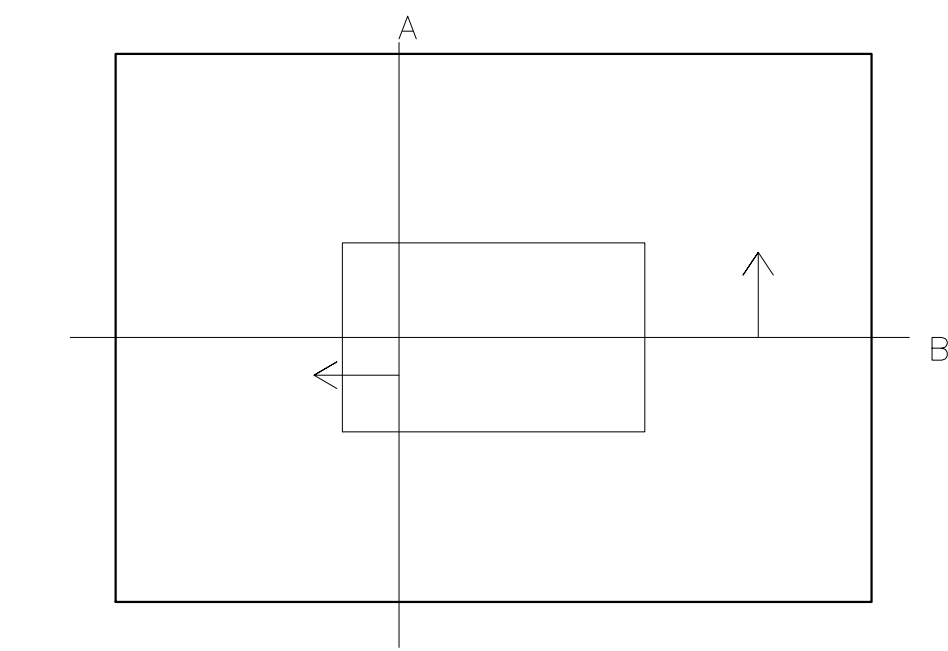


J01 核心厅屋面与墙顶 / 1:10

沿A-A截取；局部省略处不代表构件断开。

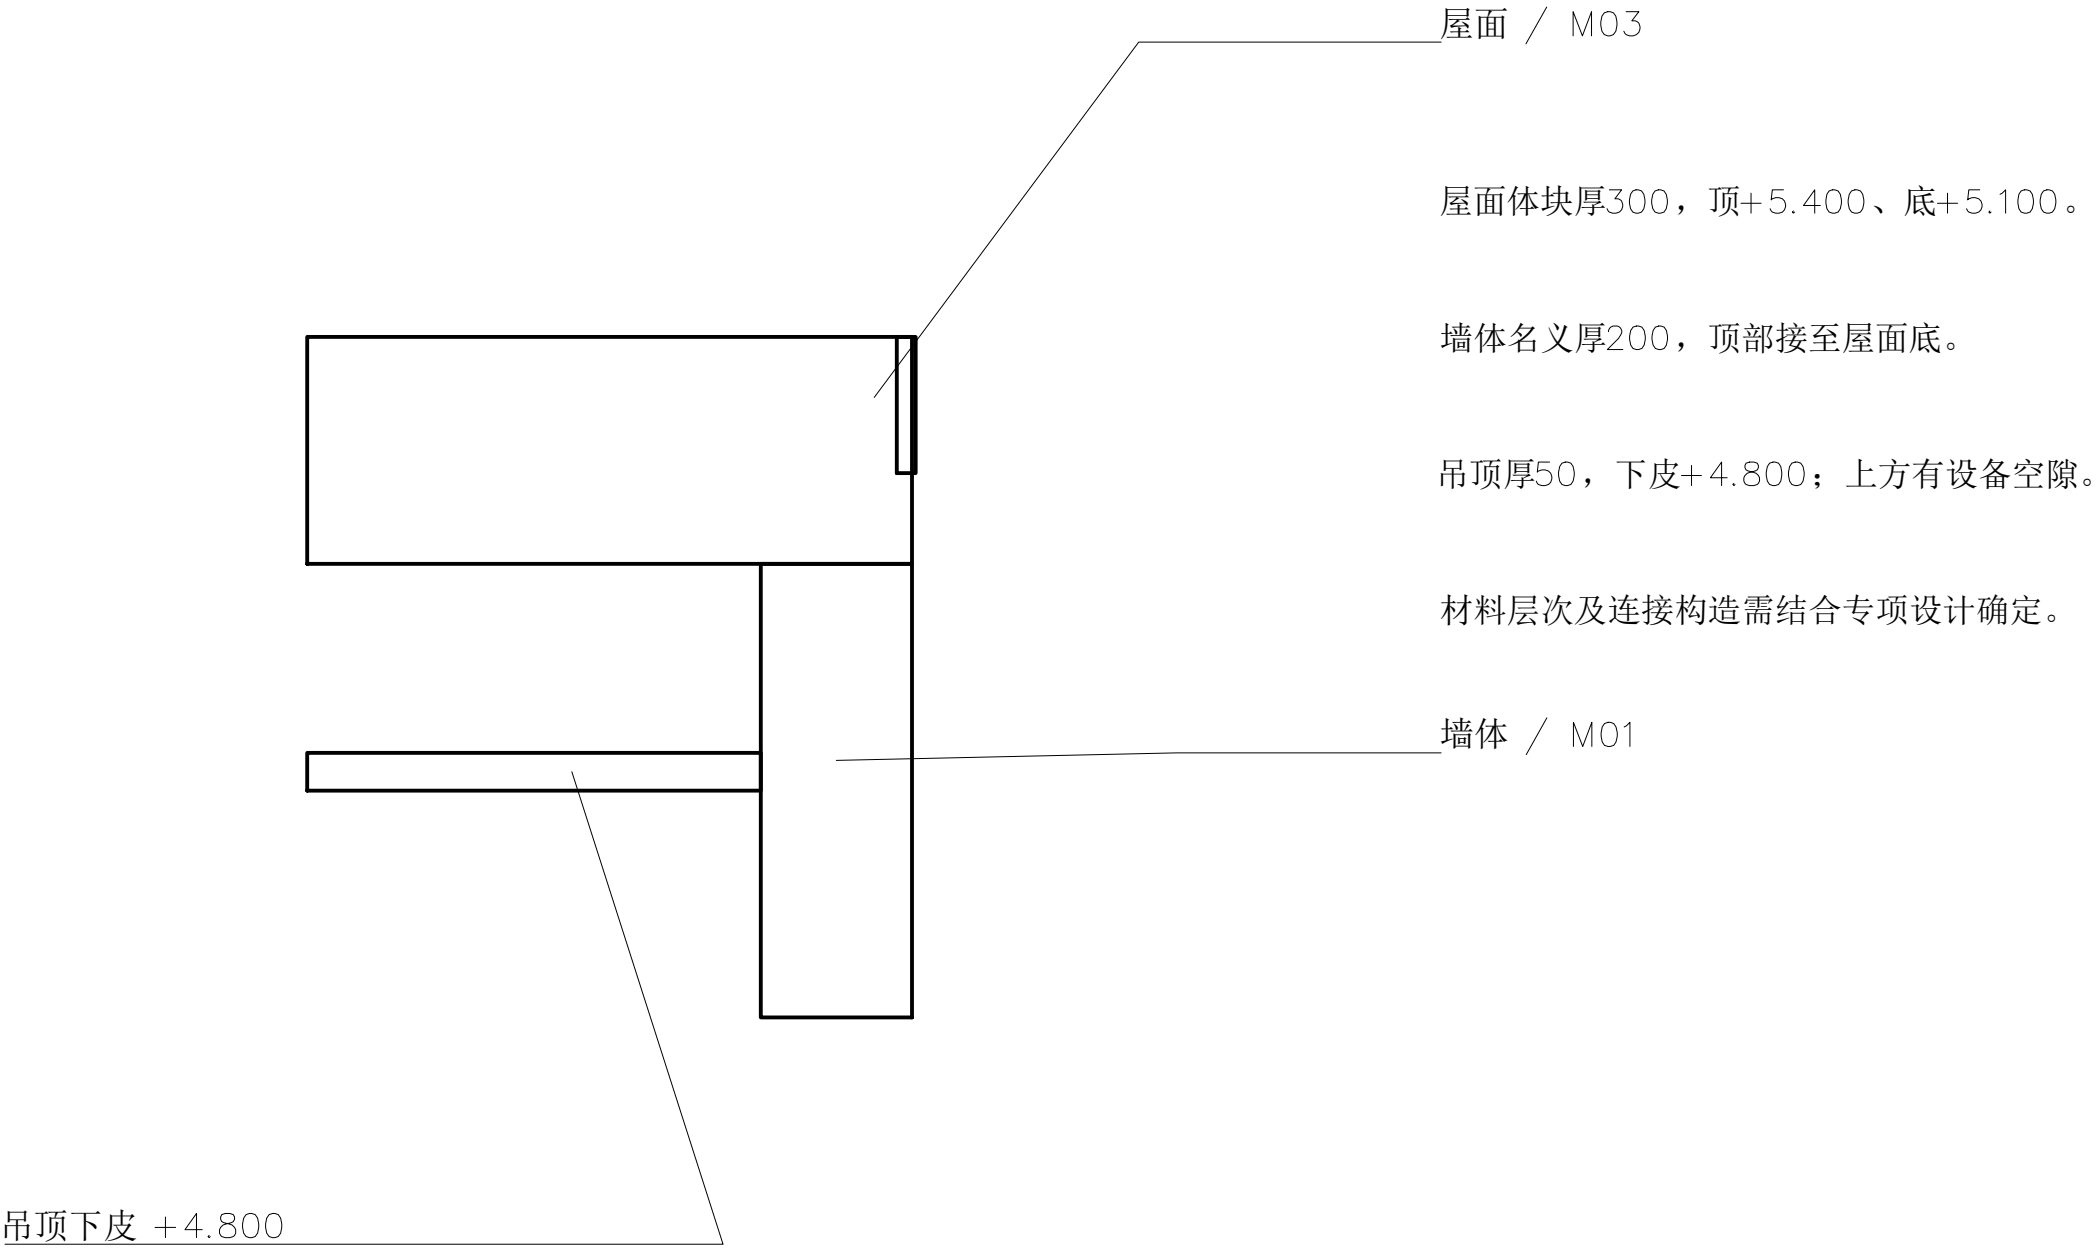

J02 院廊与露天庭院 / 1:20

沿A—A截取；厚度与标高为方案设计尺寸。

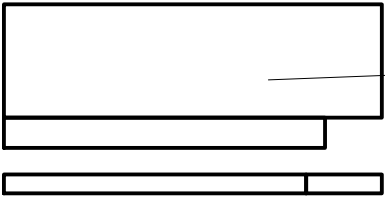

环廊屋面 / M03


环廊屋面顶+3.400，体块厚300。

吊顶下皮+2.900，格栅/灯具另列。

庭院边缘±0.000，内侧铺装向中部找坡。

屋面排水、滴水及防水收边待专项深化。


露天庭院上方不加盖。

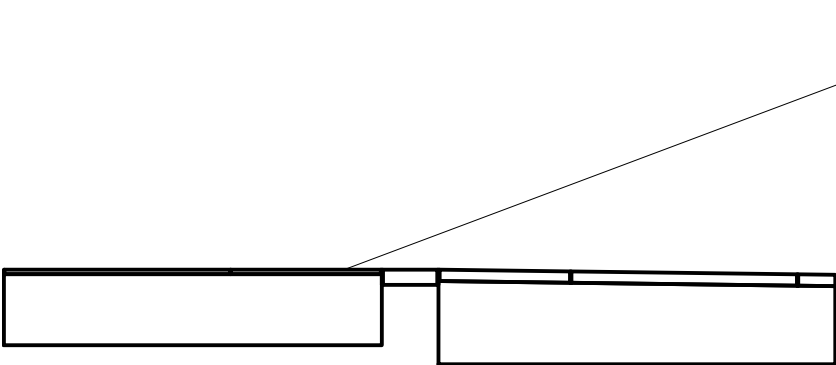

庭院边界与铺地

J03 庭院中央收水口 / 1:5

坐标mm / 标高m：X=20005，Y正向向右。方案壳体与路径，非产品选型。

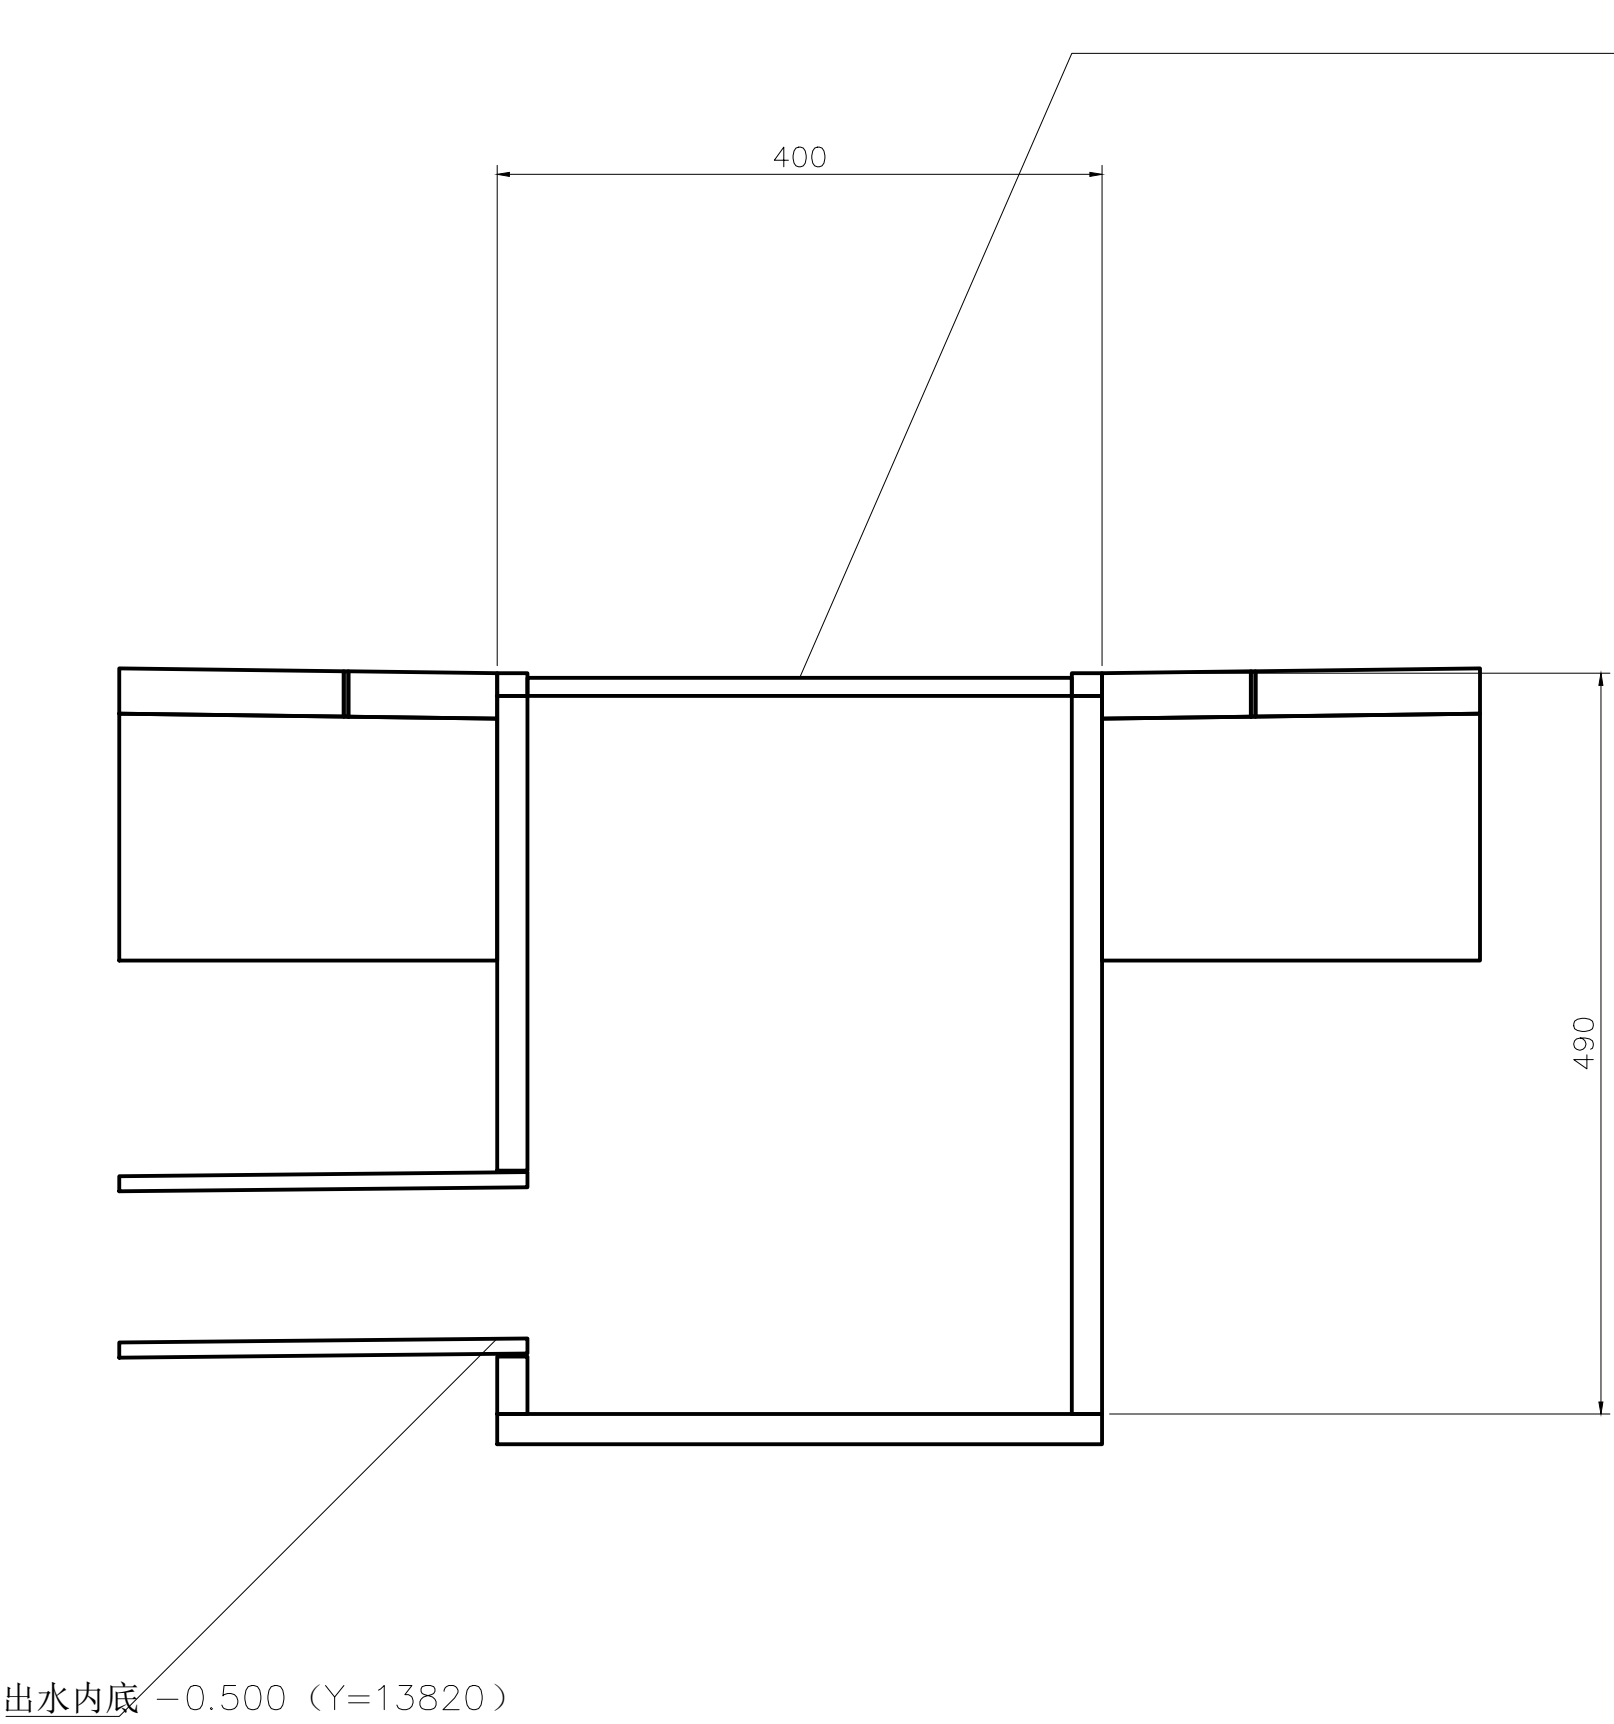

集水口外包400×400；墙厚20为方案占位。

篦条与开缝各约5；可提起维护，承载待选型。

铺装厚30；庭院基底控制至-0.250。

坑底-0.550，低于出水内底50，预留沉积空间。

出水路径净包络100×100，外包120×120。

主线向南按1%下降；并非已定管径或材质。


预留终点Y=-1500，内底-0.6532。

真实场地接驳、水量、溢流和防水待专项核定。

收水口周边与篦面相差3；保持可见、可清理。维护周期结合实际落叶和使用情况。

J04 南侧入口除尘、门槛与截水 / 1:10

D01剖切X=15000；D02采用同类接口，宽度和坐标见下表。

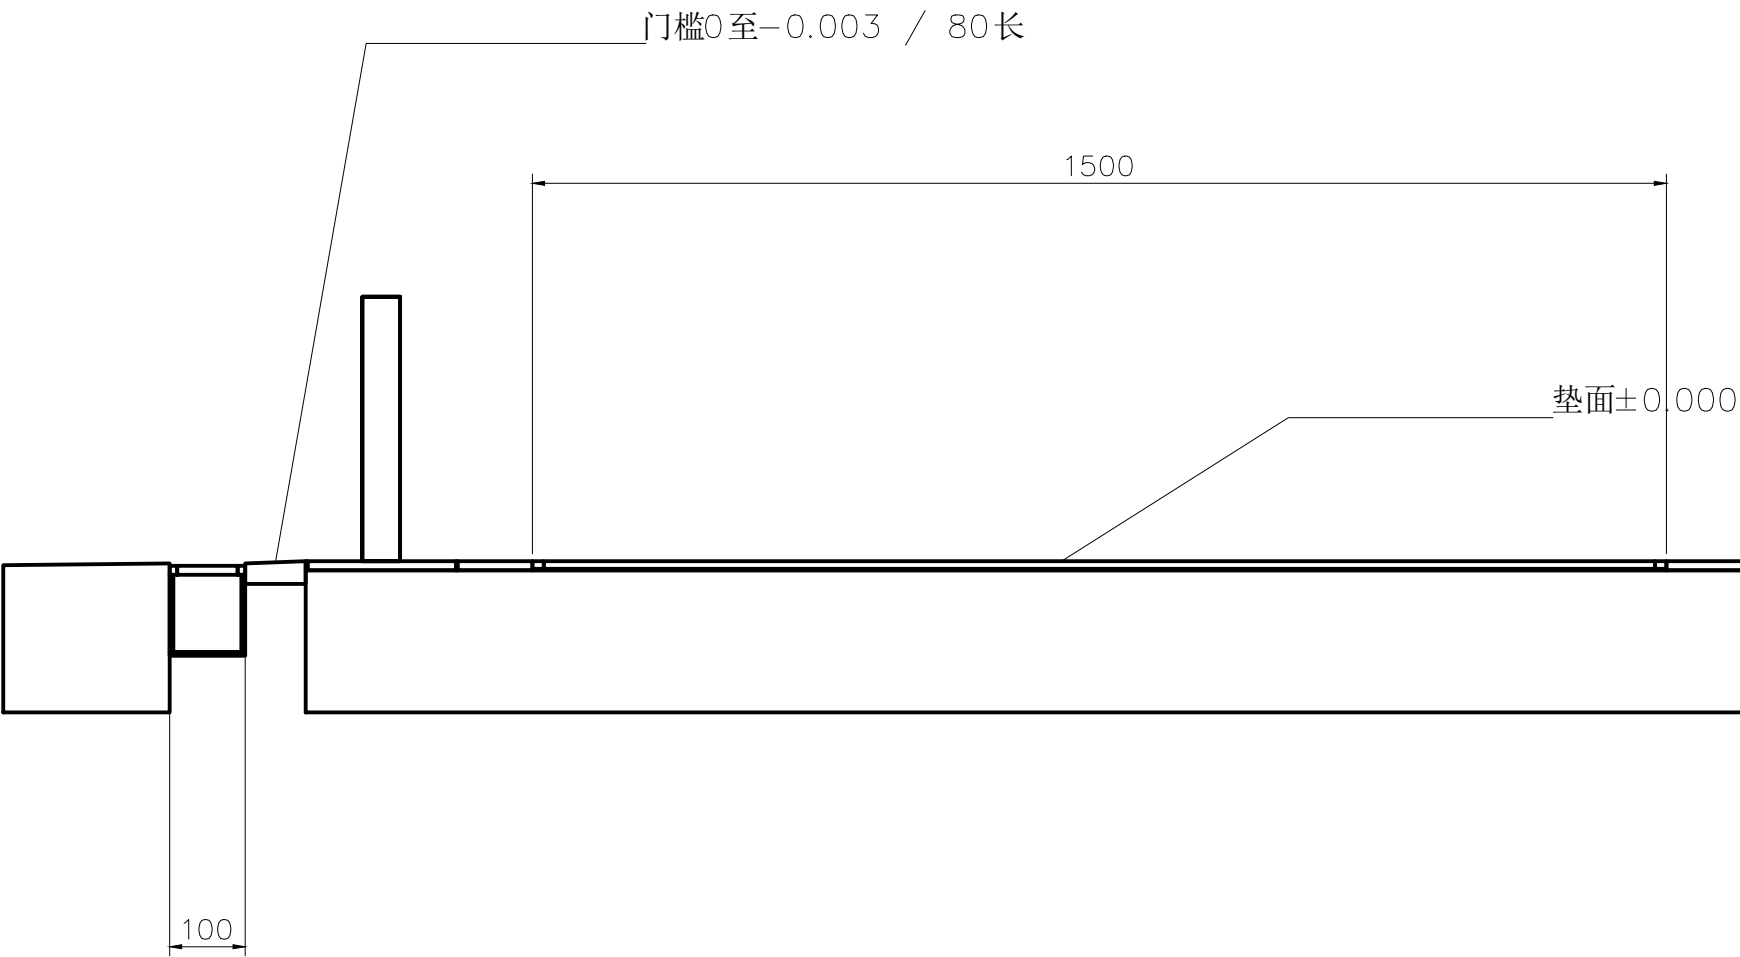

室外（图左） → 截水沟 → 门槛 → 室内除尘区（图右）

D01：垫外框X=13700..16300；Y=300..1800。

D02：垫外框X=28940..31060；Y=300..1800。

D01 / D02截水沟长3200 / 2600；Y=-180..-80。

室外平台、雨水接口和门槛均属方案条件，不代表真实场地及性能验收。

室内托盘与除尘垫总预留12，顶面齐平。

门槛外端-0.003，内端±0.000。

截水沟宽100，篦面-0.006，沟底-0.120。

外侧局部平台向外1%坡，远边标高-0.023。


沟右端50×50竖向出口是接口预留。

支管继续接往何处，需结合实际场地确定。

现有门扇位置保持；门底净隙和五金待选型。

寻香展区室内立面

沿X=5.000向西看，Y=7.000至17.000。观察坐标单位m；尺寸mm / 1:50

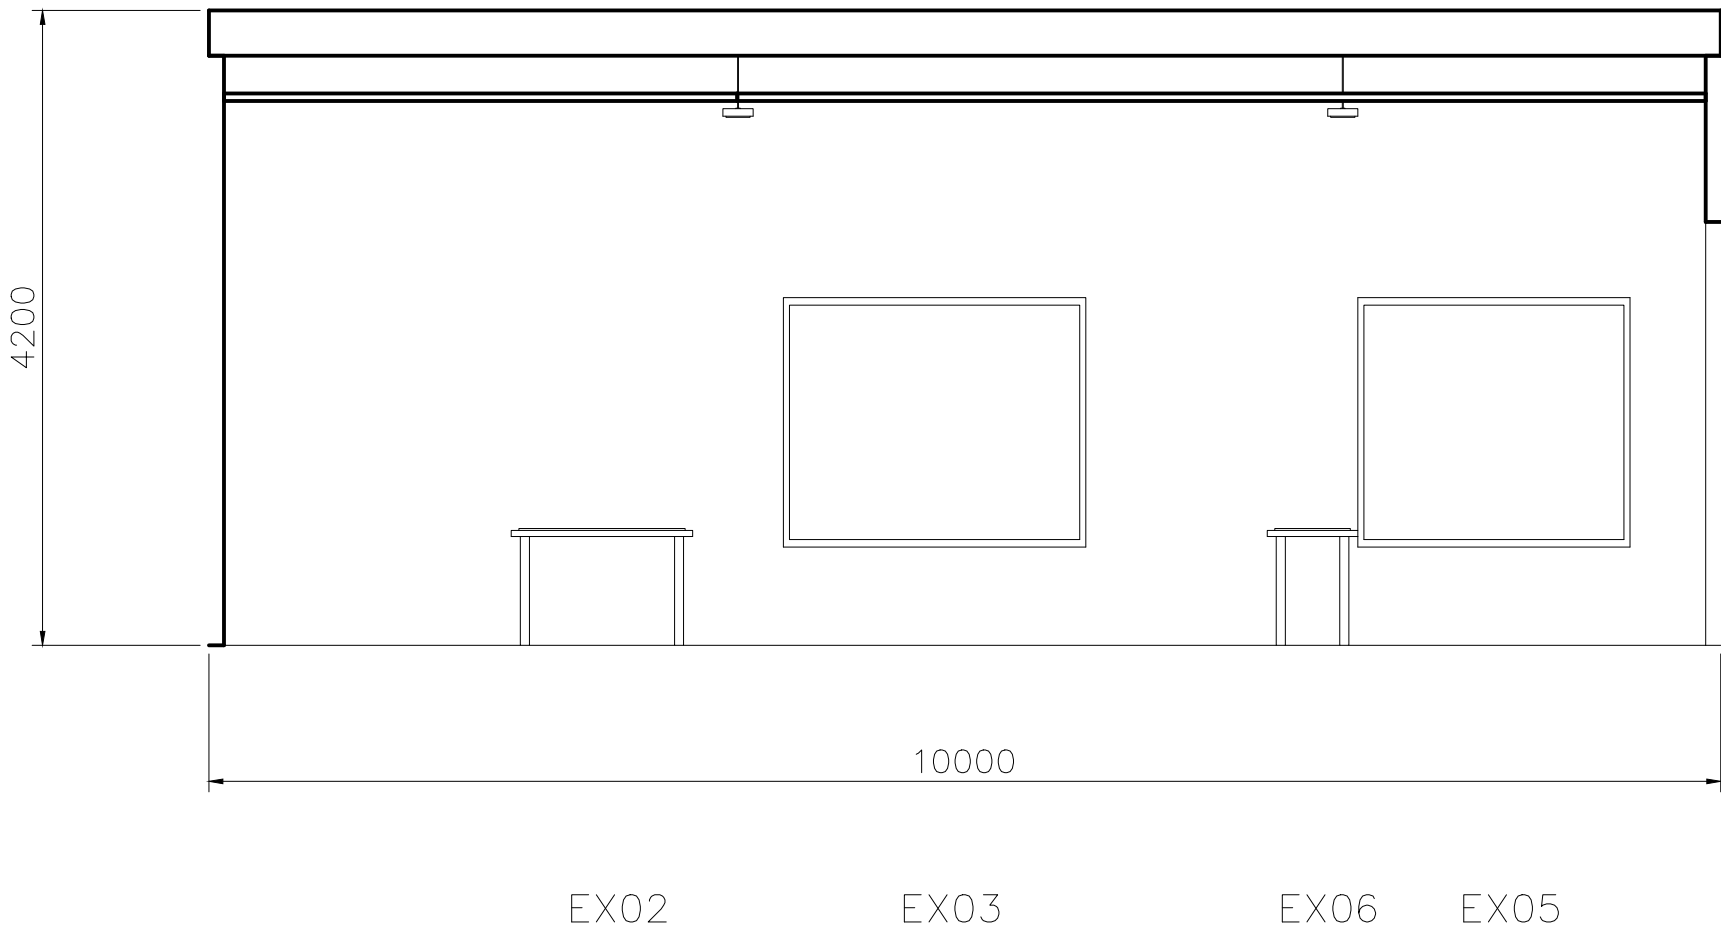

左侧尺寸为视域最高轮廓高度；室内净高见D07。

观察方向与视域范围见图上方。

视域端部裁切不表示墙体断开；安装节点需结合材料与设备选型深化。

立面与内容

EX02 / EX03 / EX05 / EX06沿墙布置。

台体、竖向内容面、墙体与吊灯位置如图。

主题依次为地域、历史、非遗及莞香与东莞。


展项定位见D03；家具平面见D02。

展板图文与尺寸见展陈图文分册。

粗线为切到的构件，细线为视域内可见投影。
玻璃不遮挡其后轮廓；图像贴图不转为几何线。

识香核心厅室内立面

沿Y=25.000向北看，X=10.000至30.000。观察坐标单位m；尺寸mm / 1:50

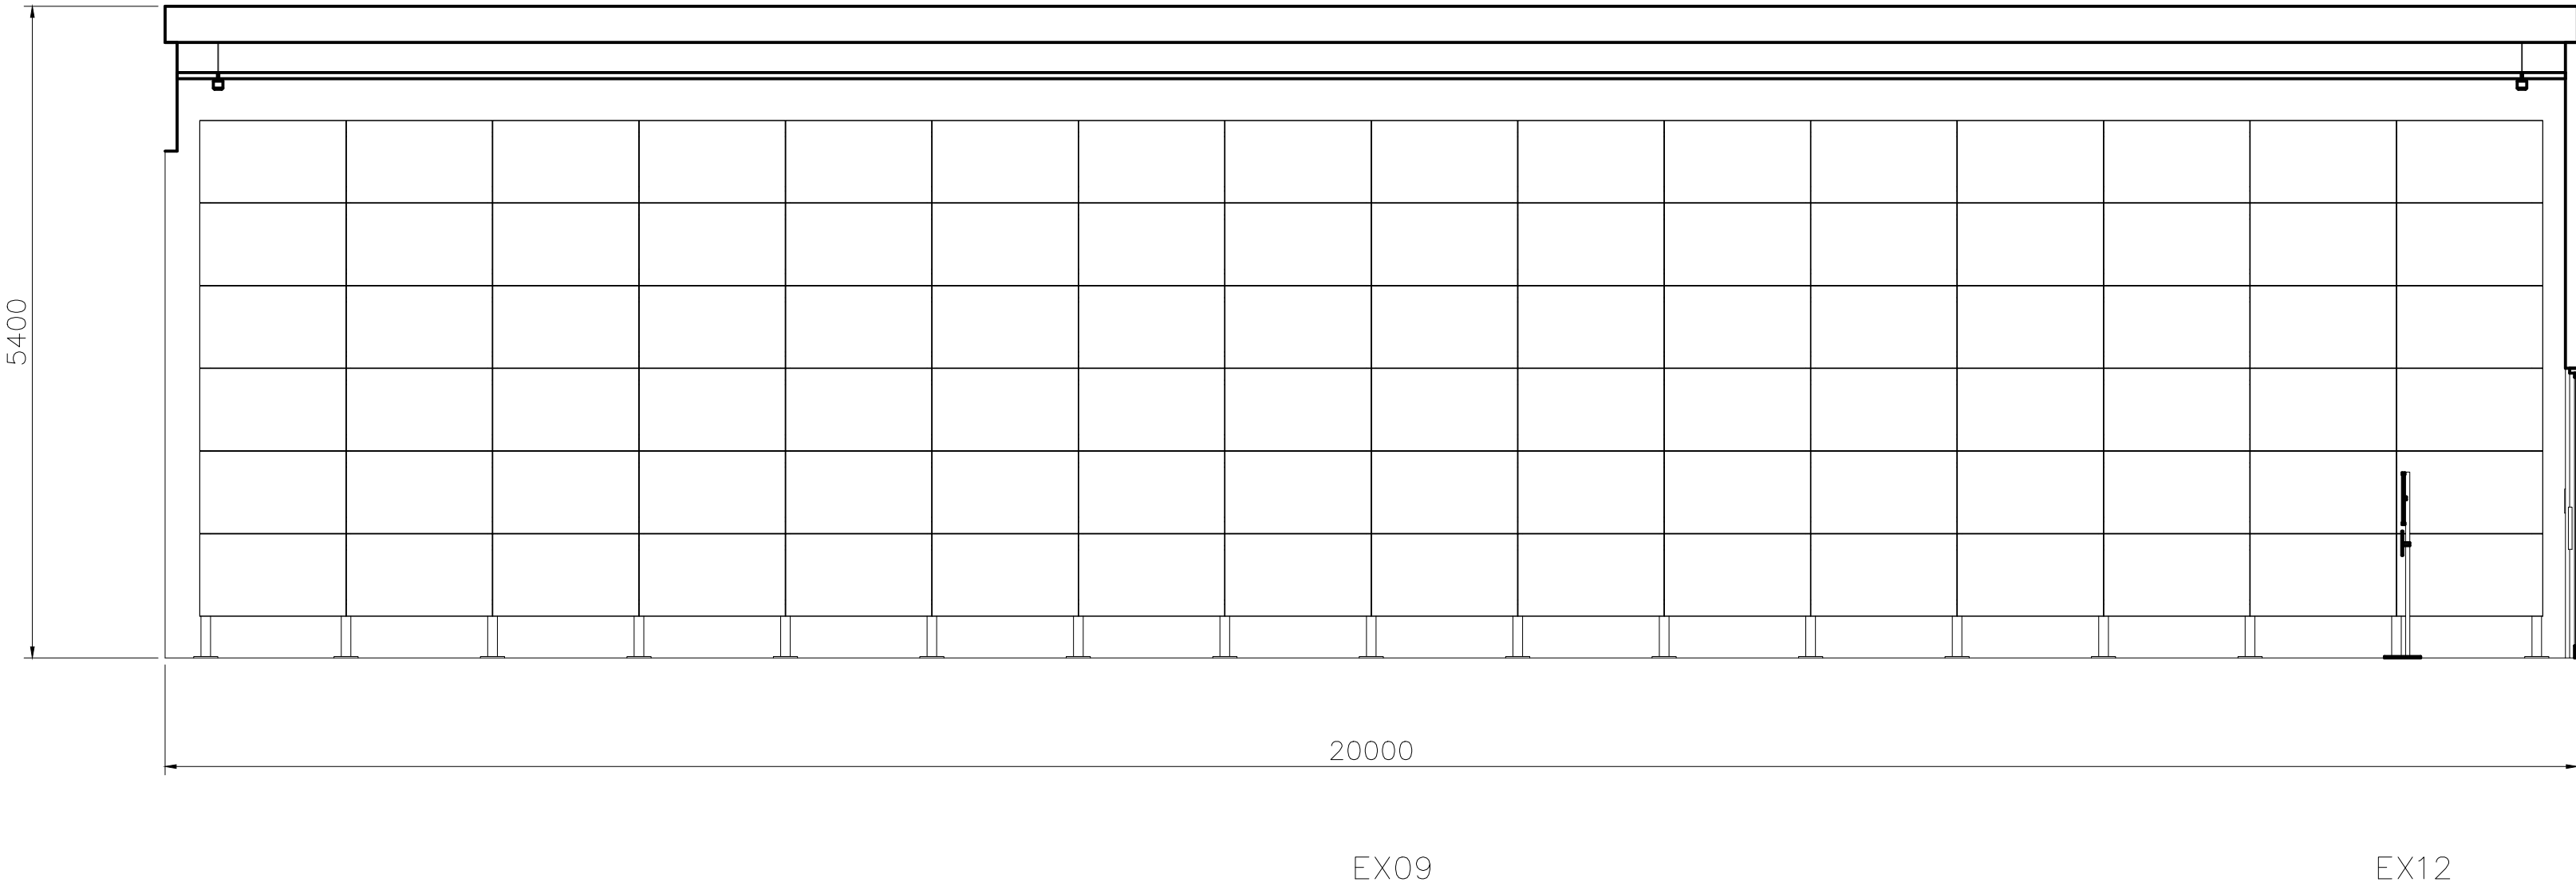

左侧尺寸为视域最高轮廓高度；室内净高见D07。

观察方向与视域范围见图上方。

视域端部裁切不表示墙体断开；安装节点需结合材料与设备选型深化。

立面与内容

北墙整墙液晶保留，中央观看空间留空。

屏面、基座及可见收边位置如图。

屏幕结构与维护接口详见D12A。


《从树到香》：45秒无声循环知识影像。

墙面及屏面后方支架详见结构定位图。


粗线为切到的构件，细线为视域内可见投影。
玻璃不遮挡其后轮廓；图像贴图不转为几何线。

品香 / 六个编号与体验陈设


EX13 闻香、EX14 材料与香品、EX16 气味记录；EX17/18为休息及导向服务。

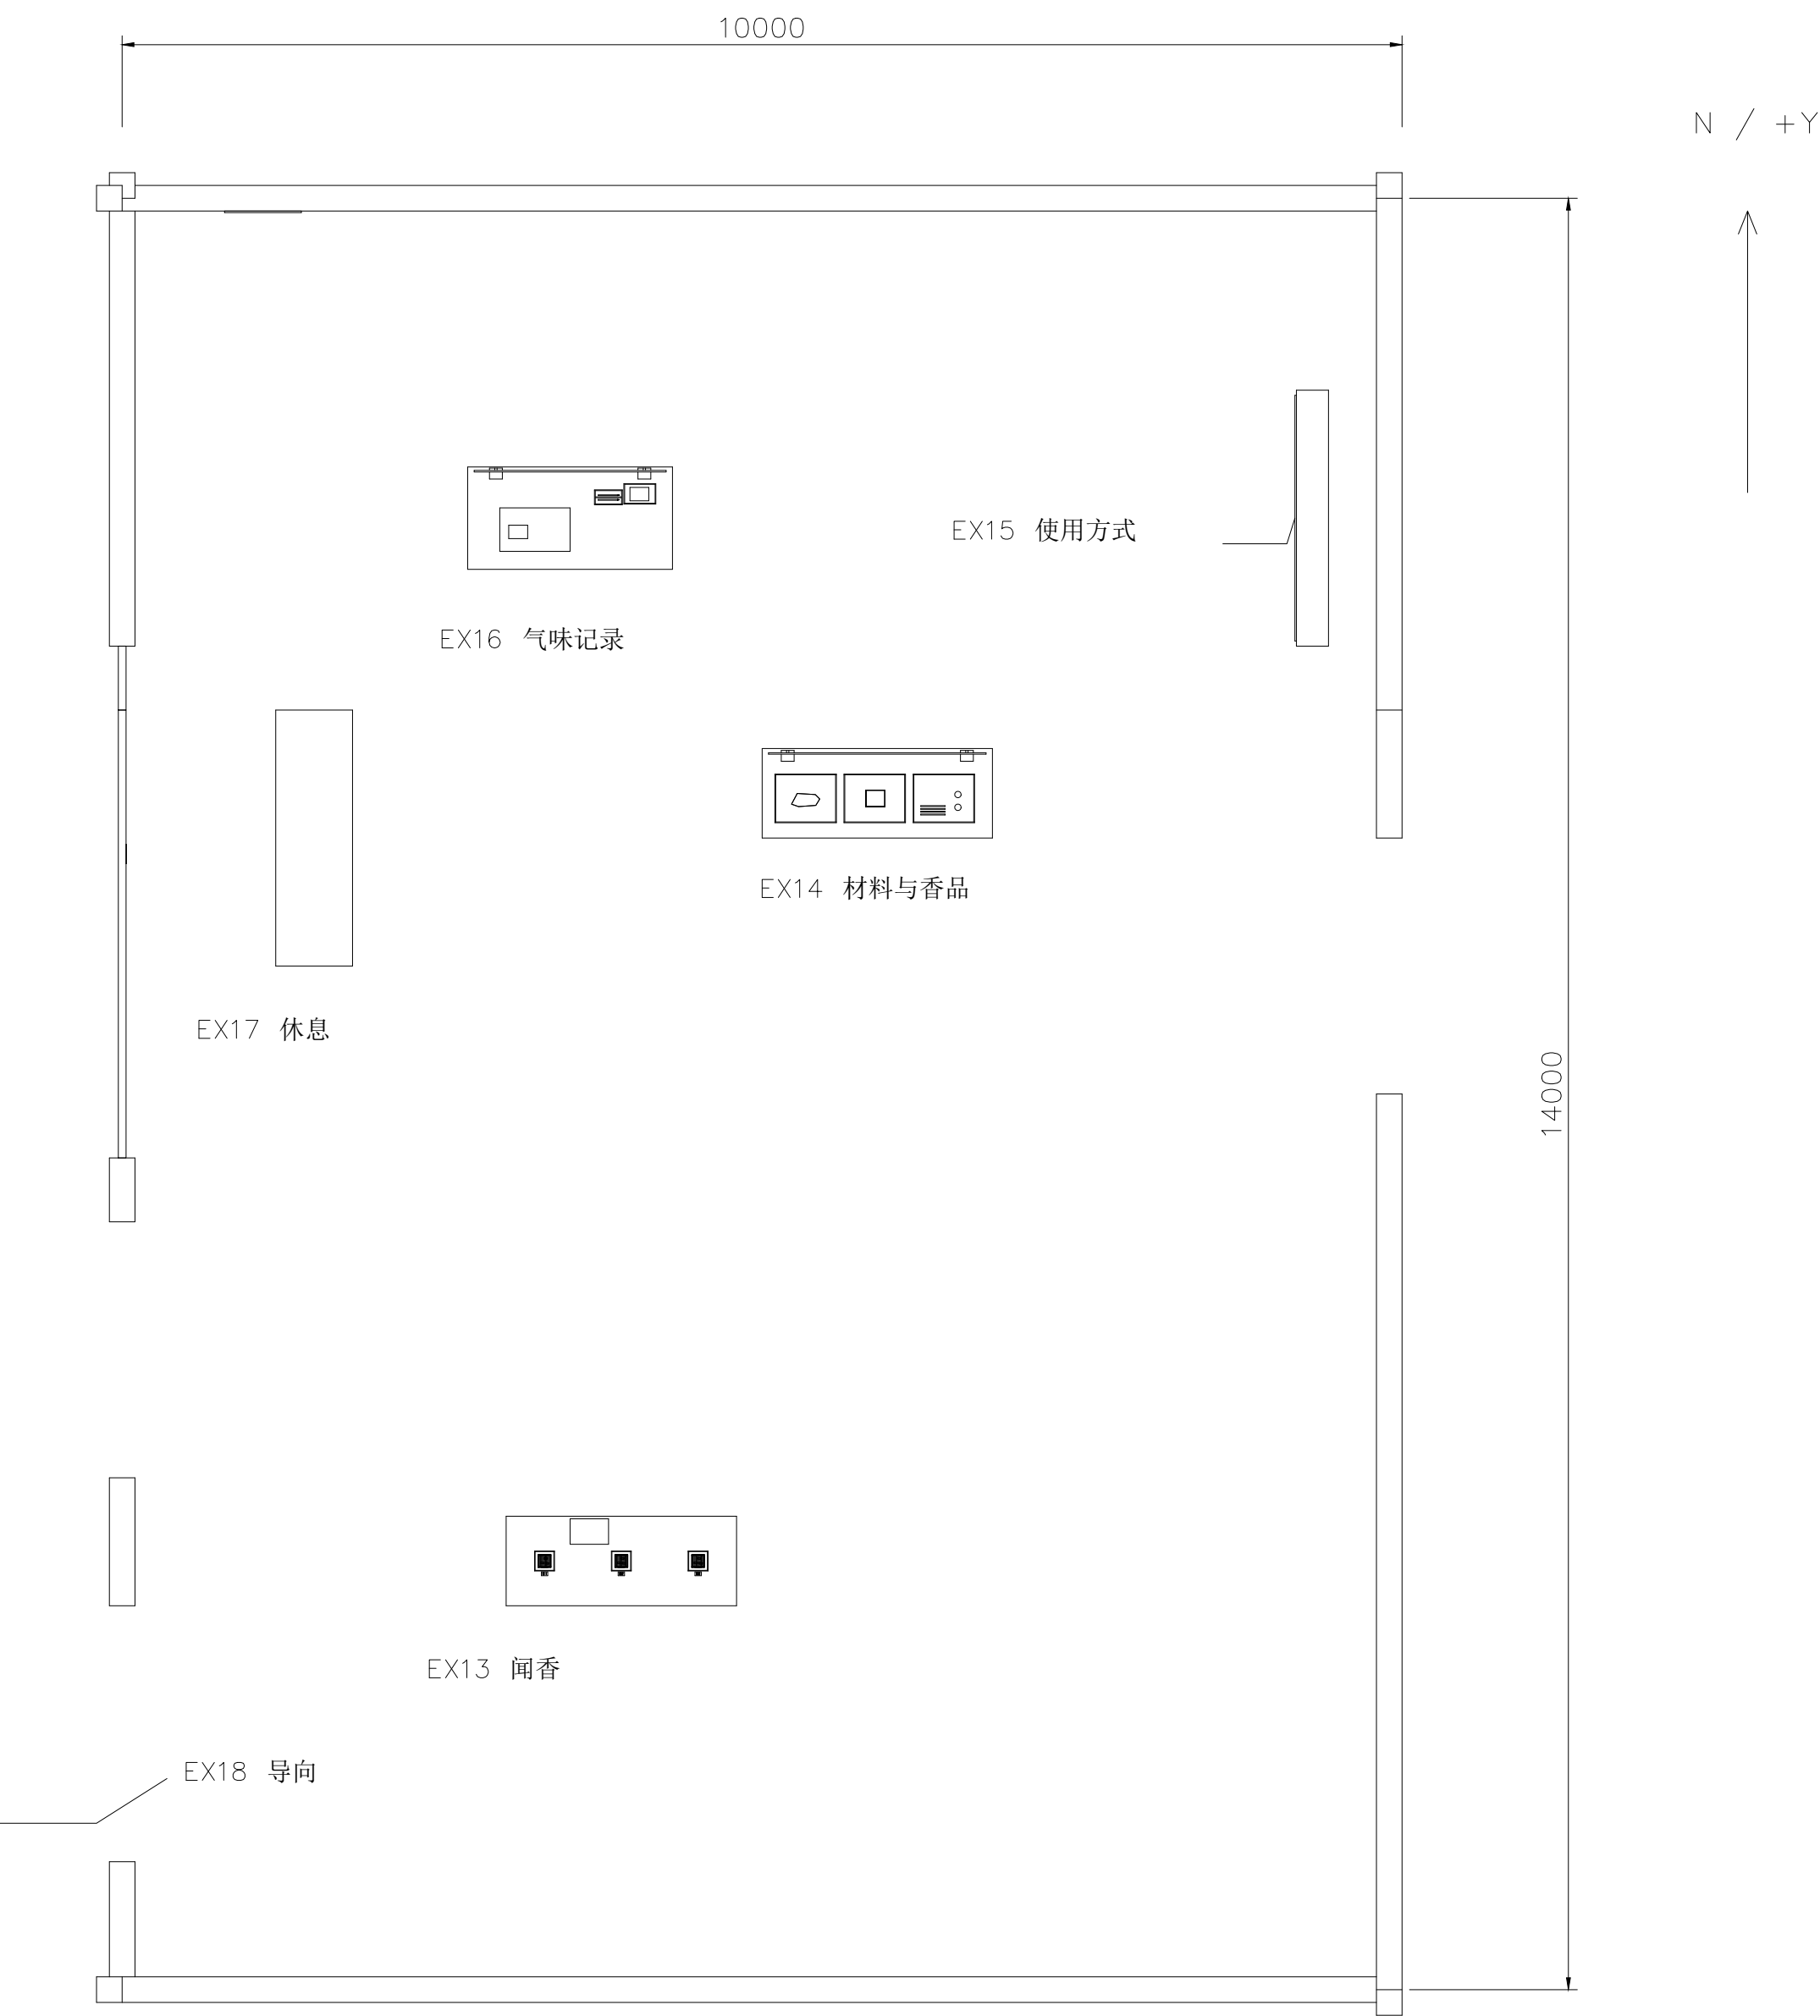


A 东向 / 由西看东 / 1:50

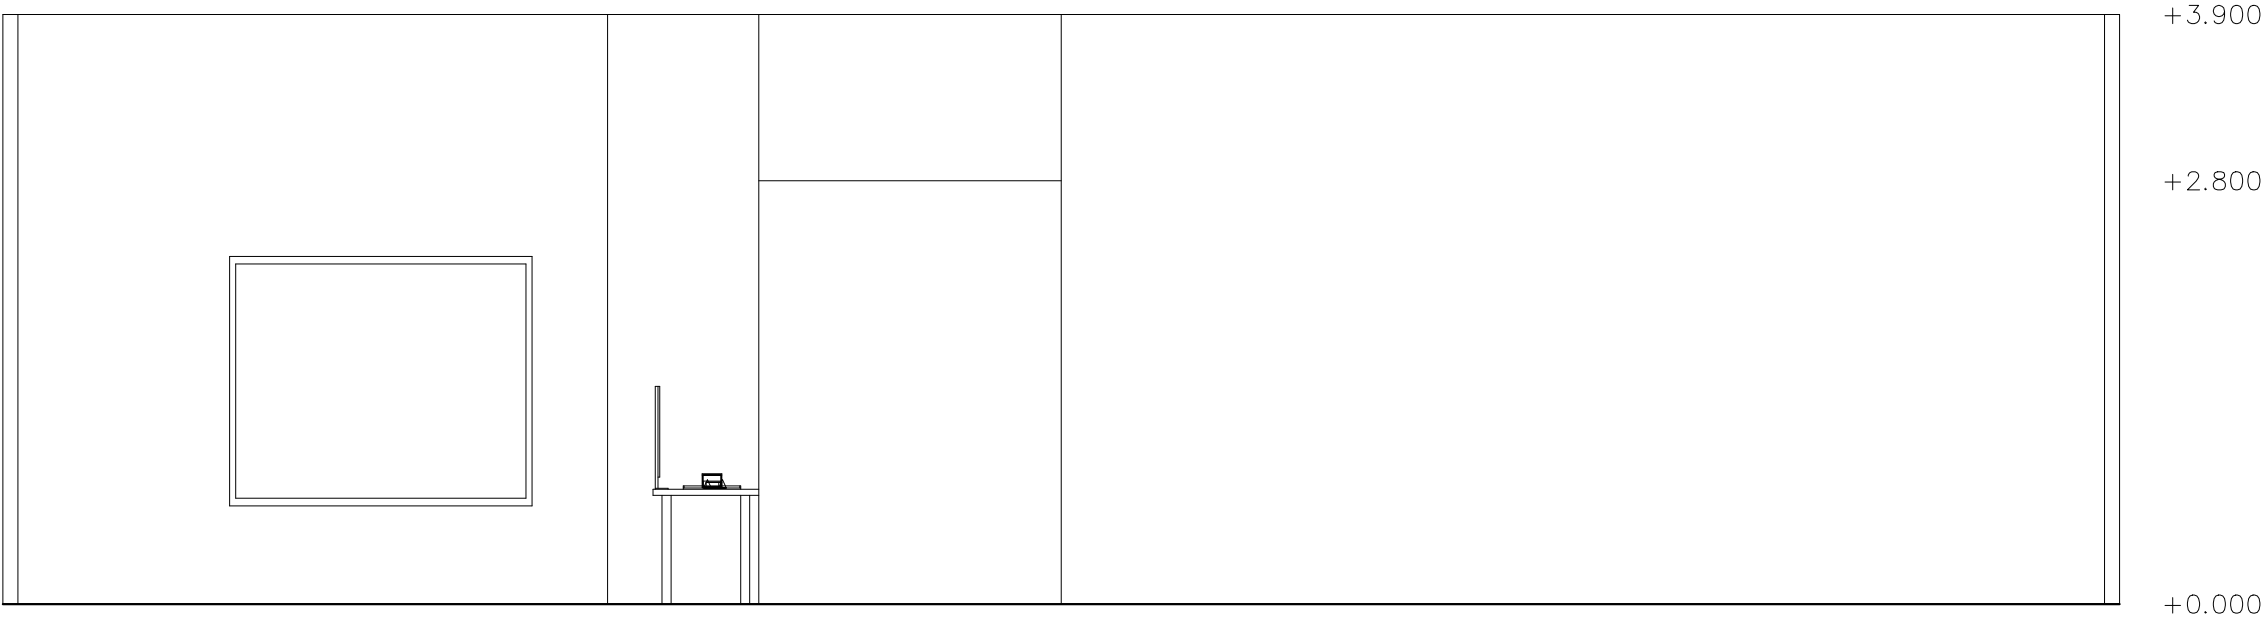

B 西向 / 由东看西 / 1:50

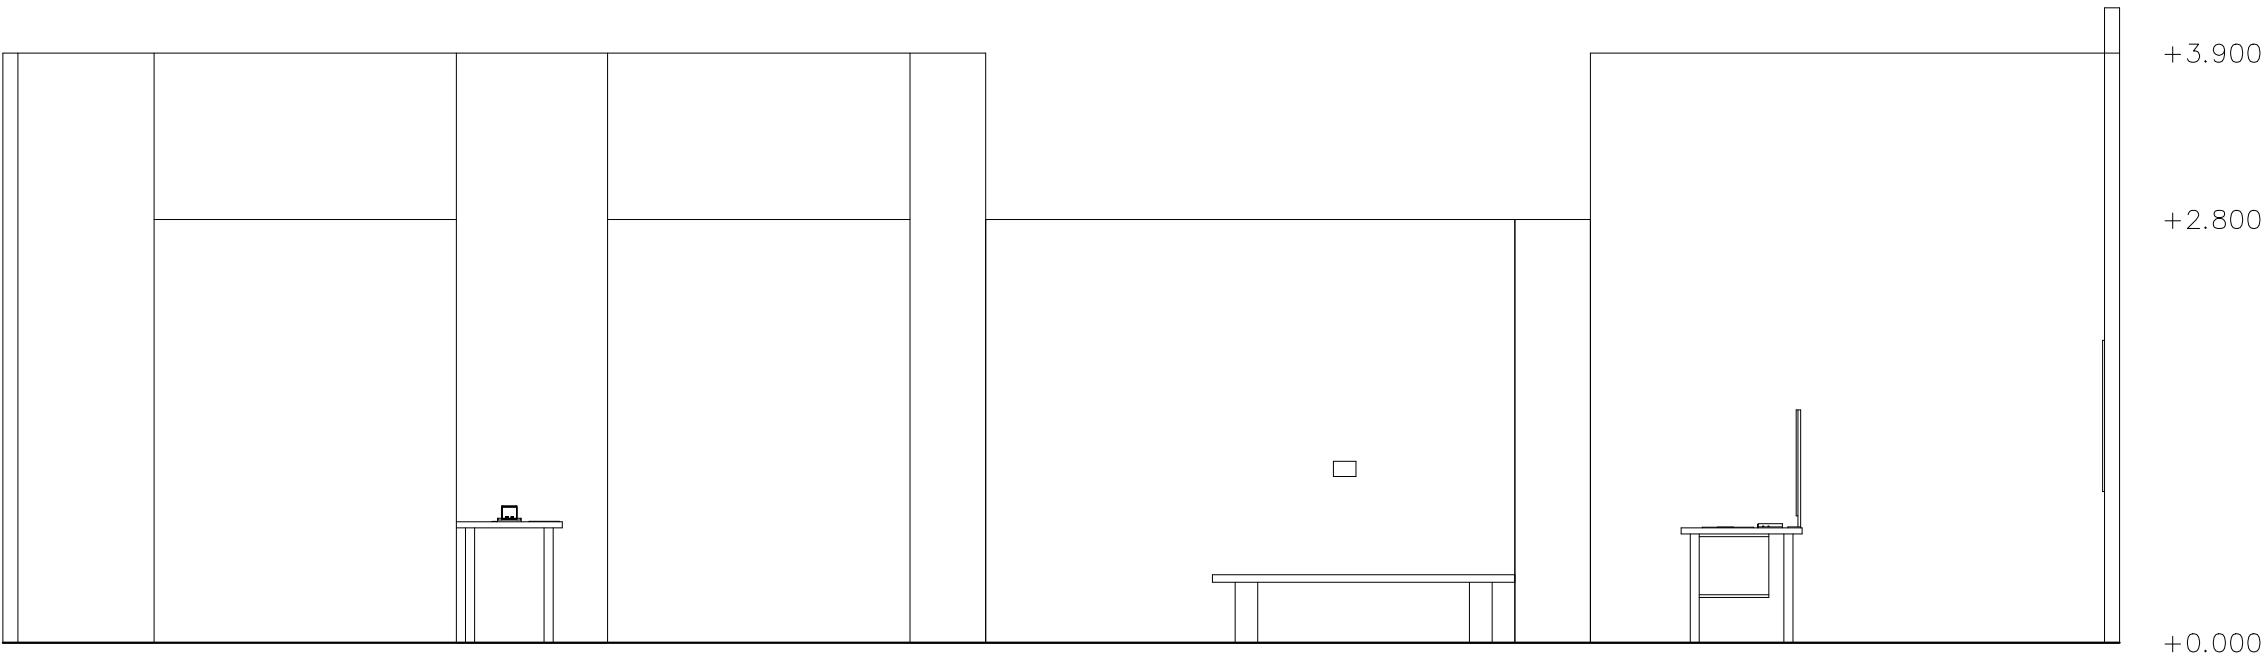

D 南向 / 由北看南 / 1:50

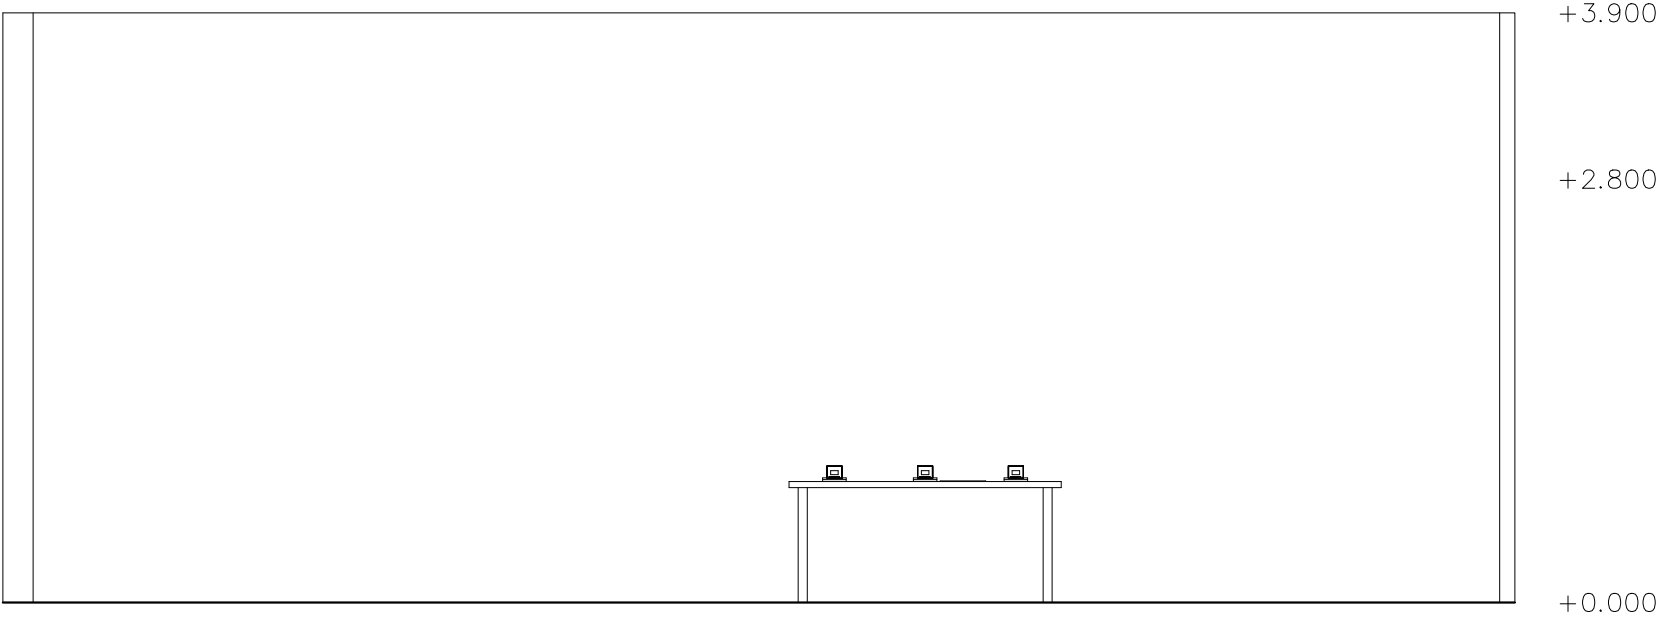

EX13：三只闻香盒，编号01/02/03。

盒与归位座配对，单只提起放回。

EX14：香材、香粉、香品三组示意。

EX16：A6卡、书写垫、分格笔托。

两块信息面转为台后竖向展示。

板面图文与尺寸见展陈图文分册。


各立面取注明深度带，不表示全厅透视。

玻璃与样件可见轮廓使用细线。

台面木、框架金属及透明容器为设计材质。

样本身份、清洁方案和产品连接未定型。


C 北向 / 由南看北 / 1:50

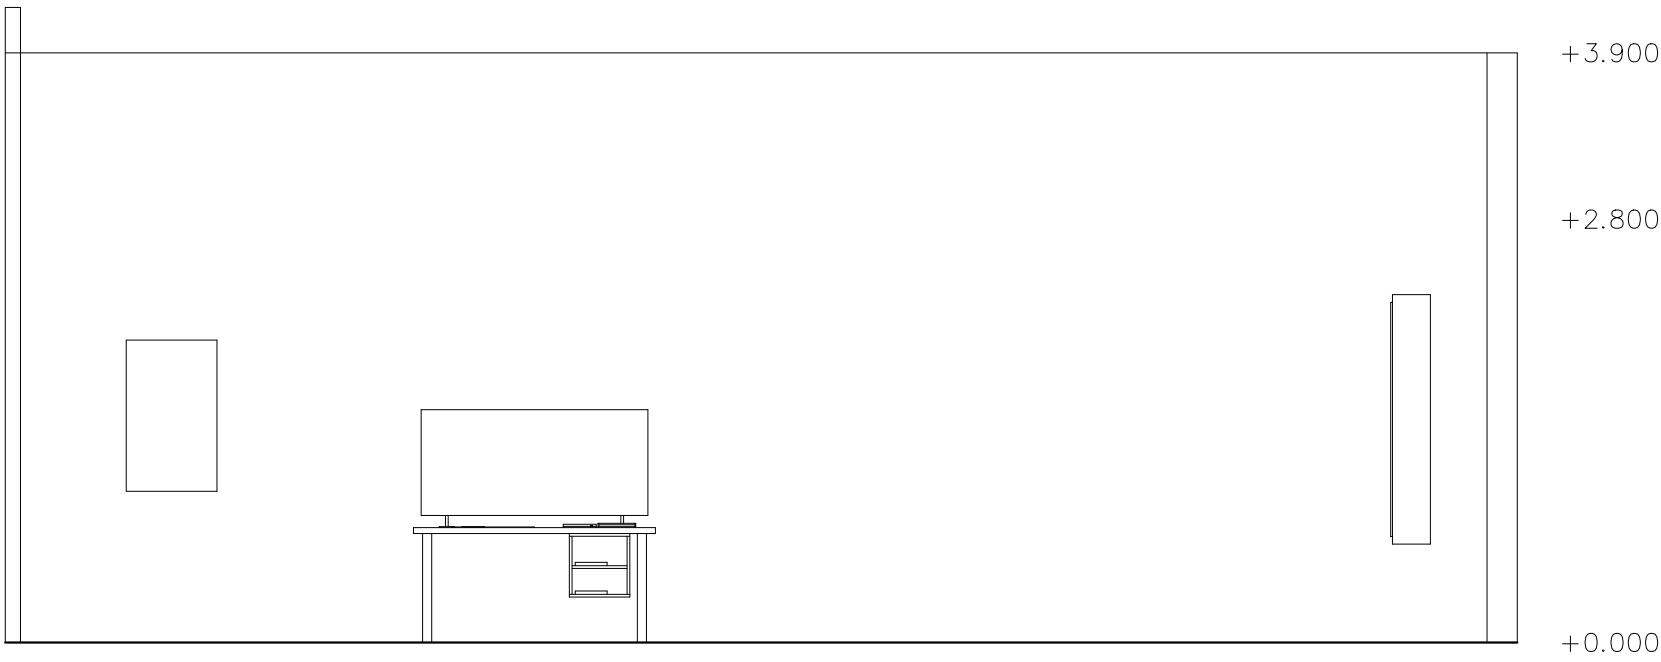

门扇及通行空间见D02/D03，顶面与安装高度见D05/D07；图文详见展陈图文分册。


EX13 / 编号闻香与取放关系

1800×700，台面800高。三盒采用同一容器几何，编号不同，不预设气味、等级或真实样本。

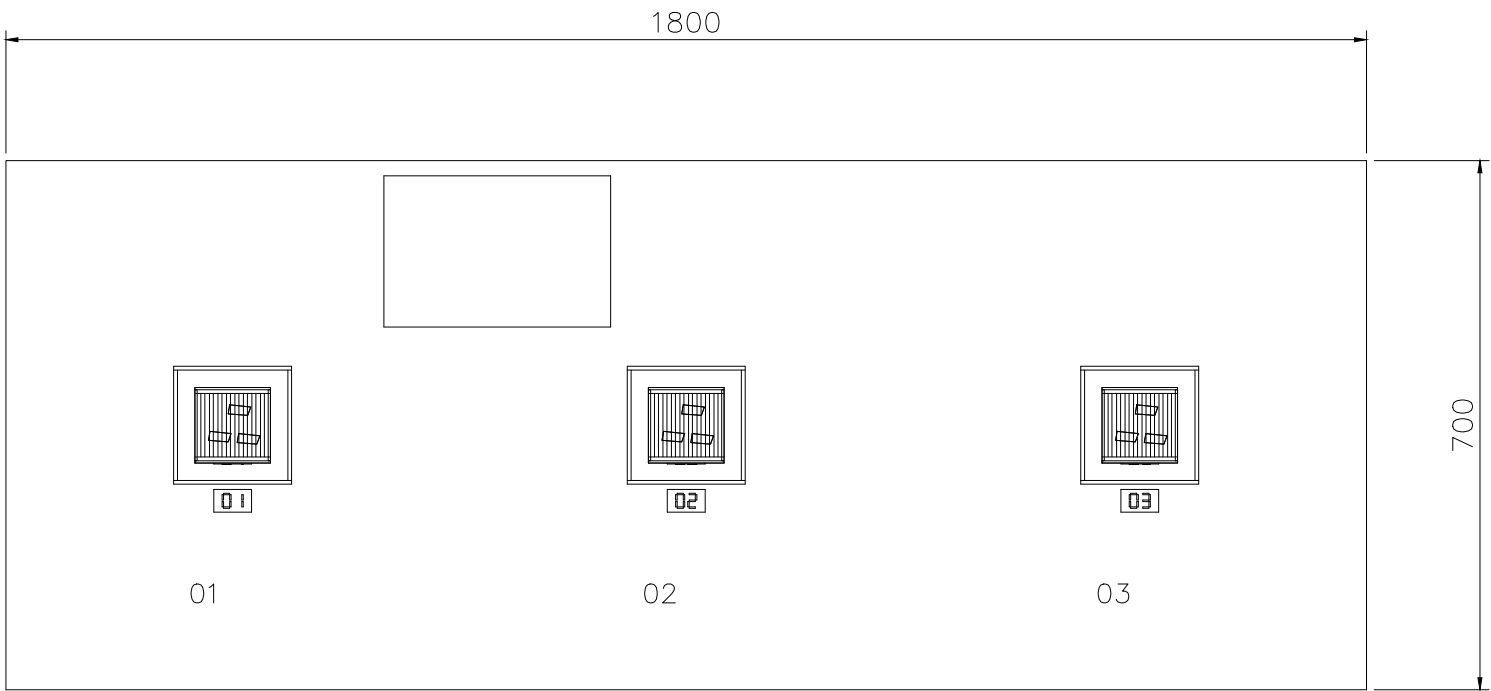


01 台面 / 三盒中心距600

02 观众侧立面 / 闭合归位

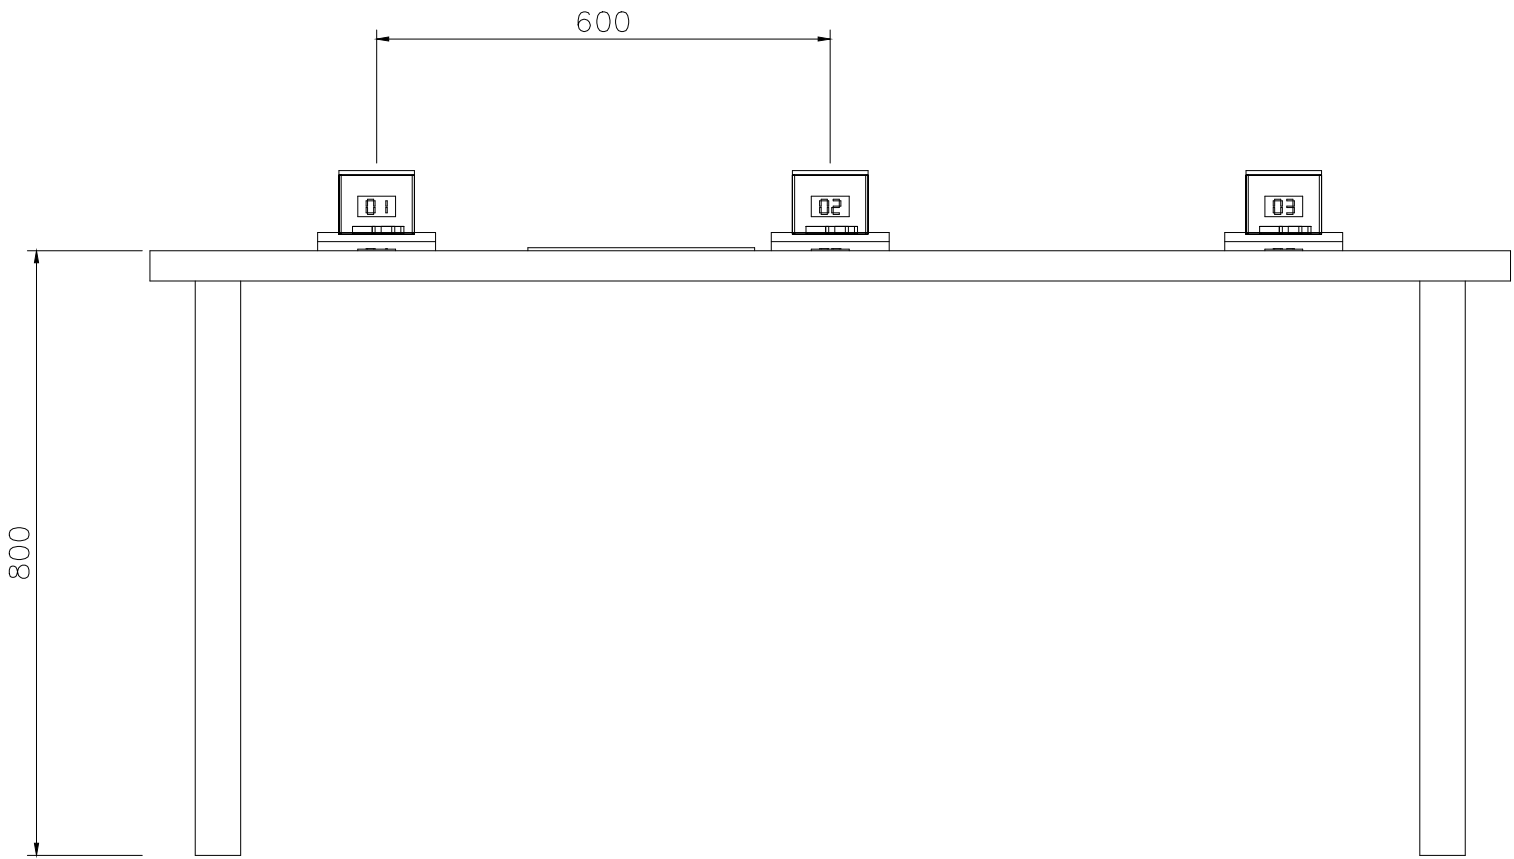

容器用于编号闻香：样品装入前应该对身份、容器相容性与清洁要求。

03 单盒提起180 / 几何检查位置

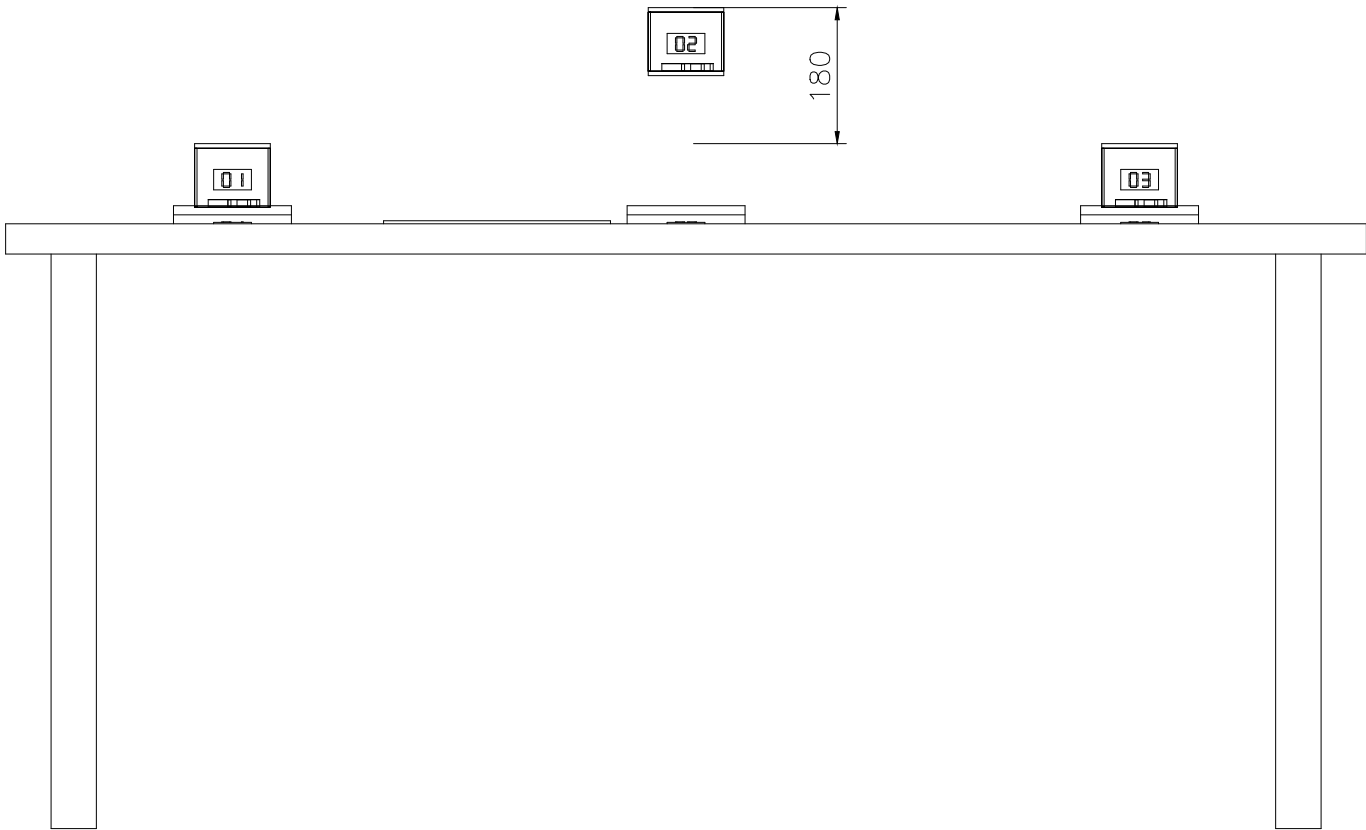

每个归位托座156×156，开口146×146。

箱体100×100，高90；透明侧壁3厚。

盒顶6厚，设7条6宽栅条及8条5.25宽通气缝。

箱体侧边至托座内缘名义间隙23。

盒前编号牌外伸1.8；含牌最小间隙21.2。

取放路径及盖上提路径无模型碰撞。


此行程检查不包含手部握持或跌落模拟。

实际气味释放、材料、圆角、盖保持与清洁待选型。


本方案不配置加热或燃烧。

闻香盒 / 容器、托座与通气盖


02号盒构造与取放示意，尺寸单位mm。

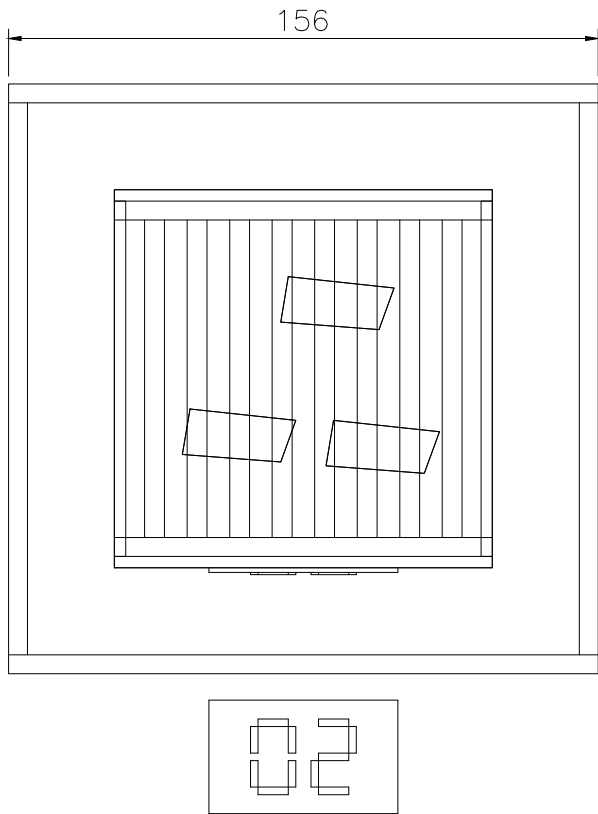


01 俯视 / 托座与盒

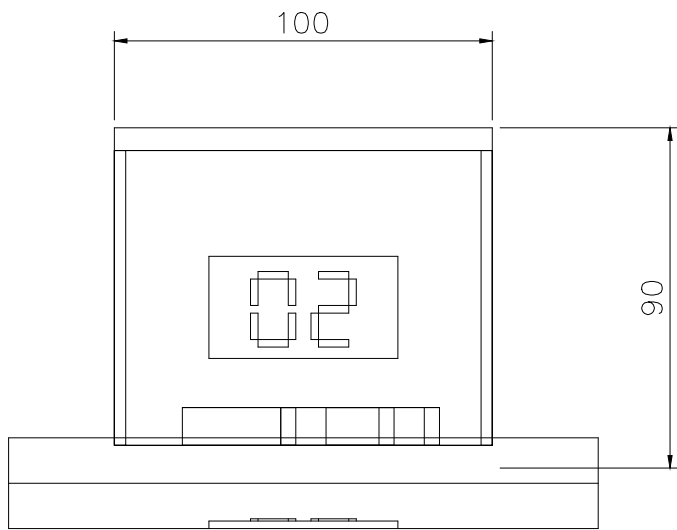

02 正视 / 90高箱体

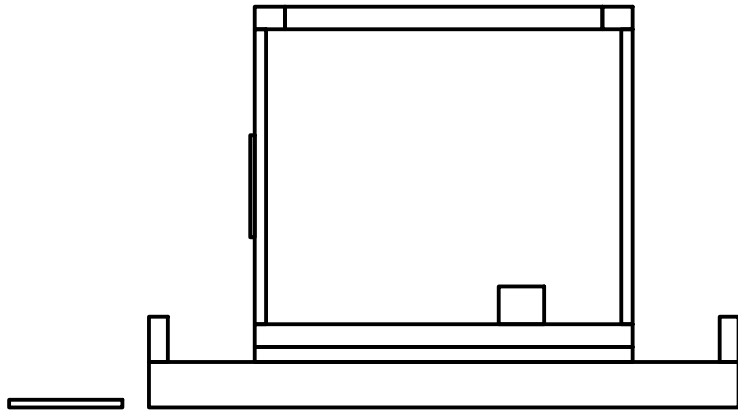

03 纵剖 / X=33900

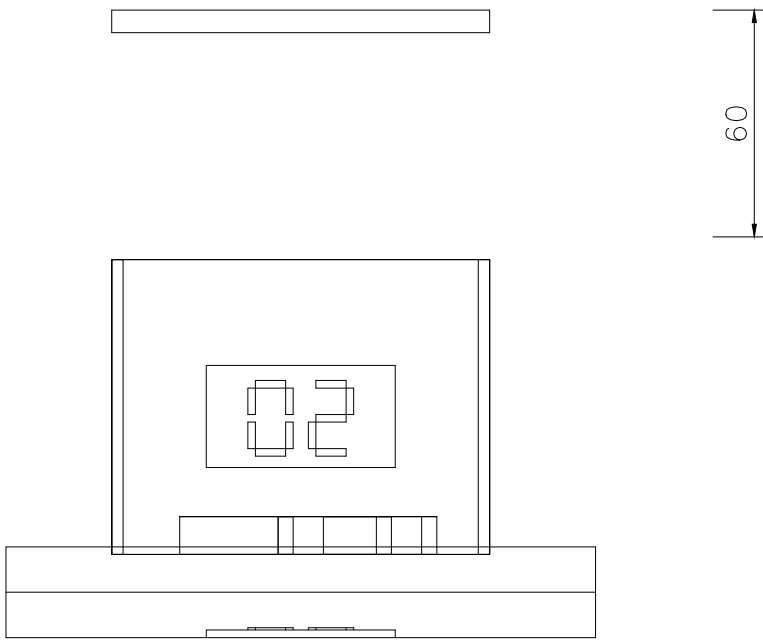

04 工作人员开盖示意 / 上提60

托座底12，内承垫4，边框5宽。

盒底6，透明壁3，净内宽94。

外框8，顶盖总厚6。

图示样材3件，不代表真实样本。

箱体与托座编号一致。

清洁时移出箱体及内垫。


开盖行程是几何示意；

盖固定、限位和材料性能待落实。

本图供方案理解；非制造图、非采购选型。未进行握持、材料强度、气味效率和清洁可行性实测。


EX14 / 材料比较 EX16 / 气味记录

台后信息板为竖向设置，朝向观众；下图示台面器具、板面及操作位置。

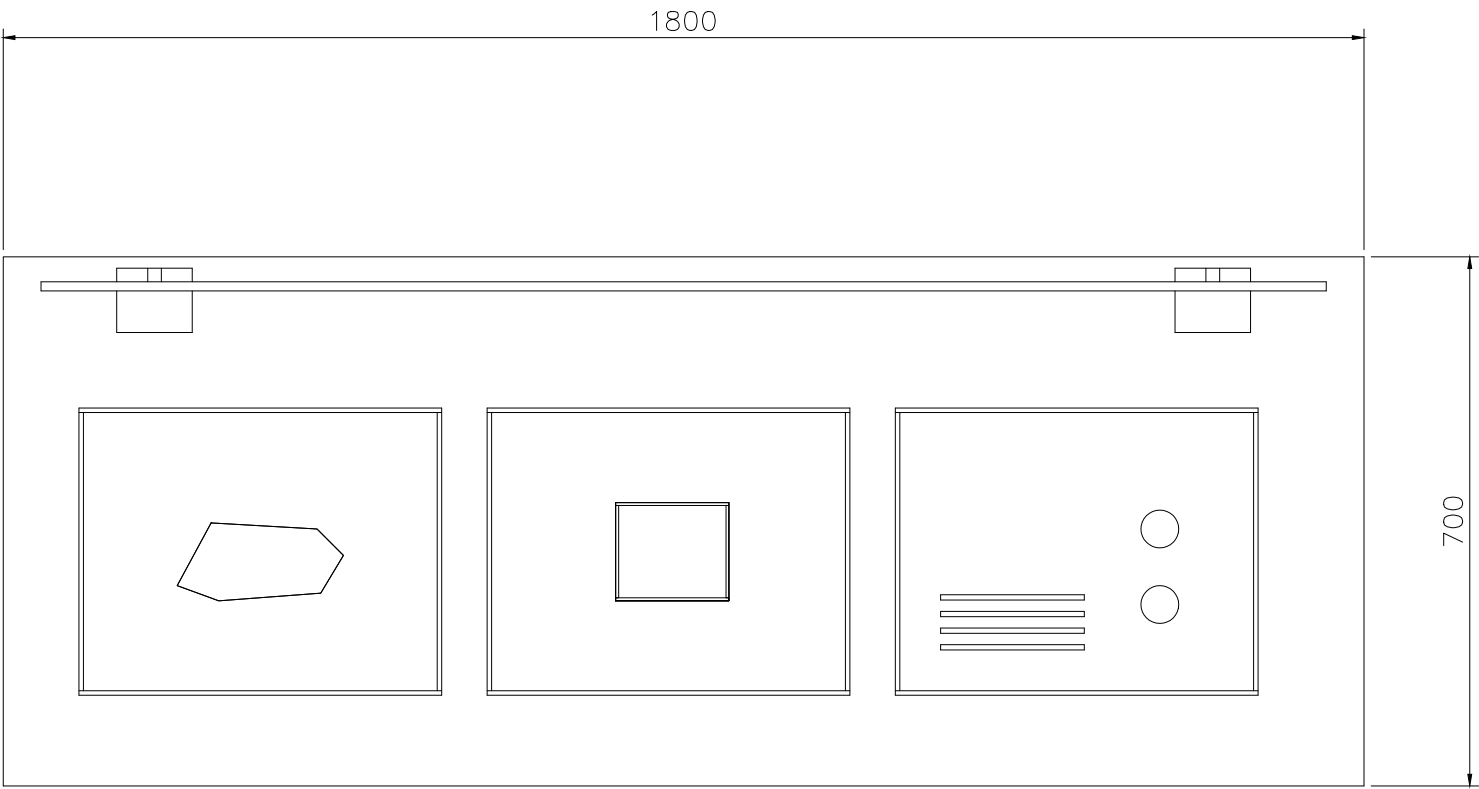


EX14 / 材料与香品台面

观众侧立面 / 总高1440

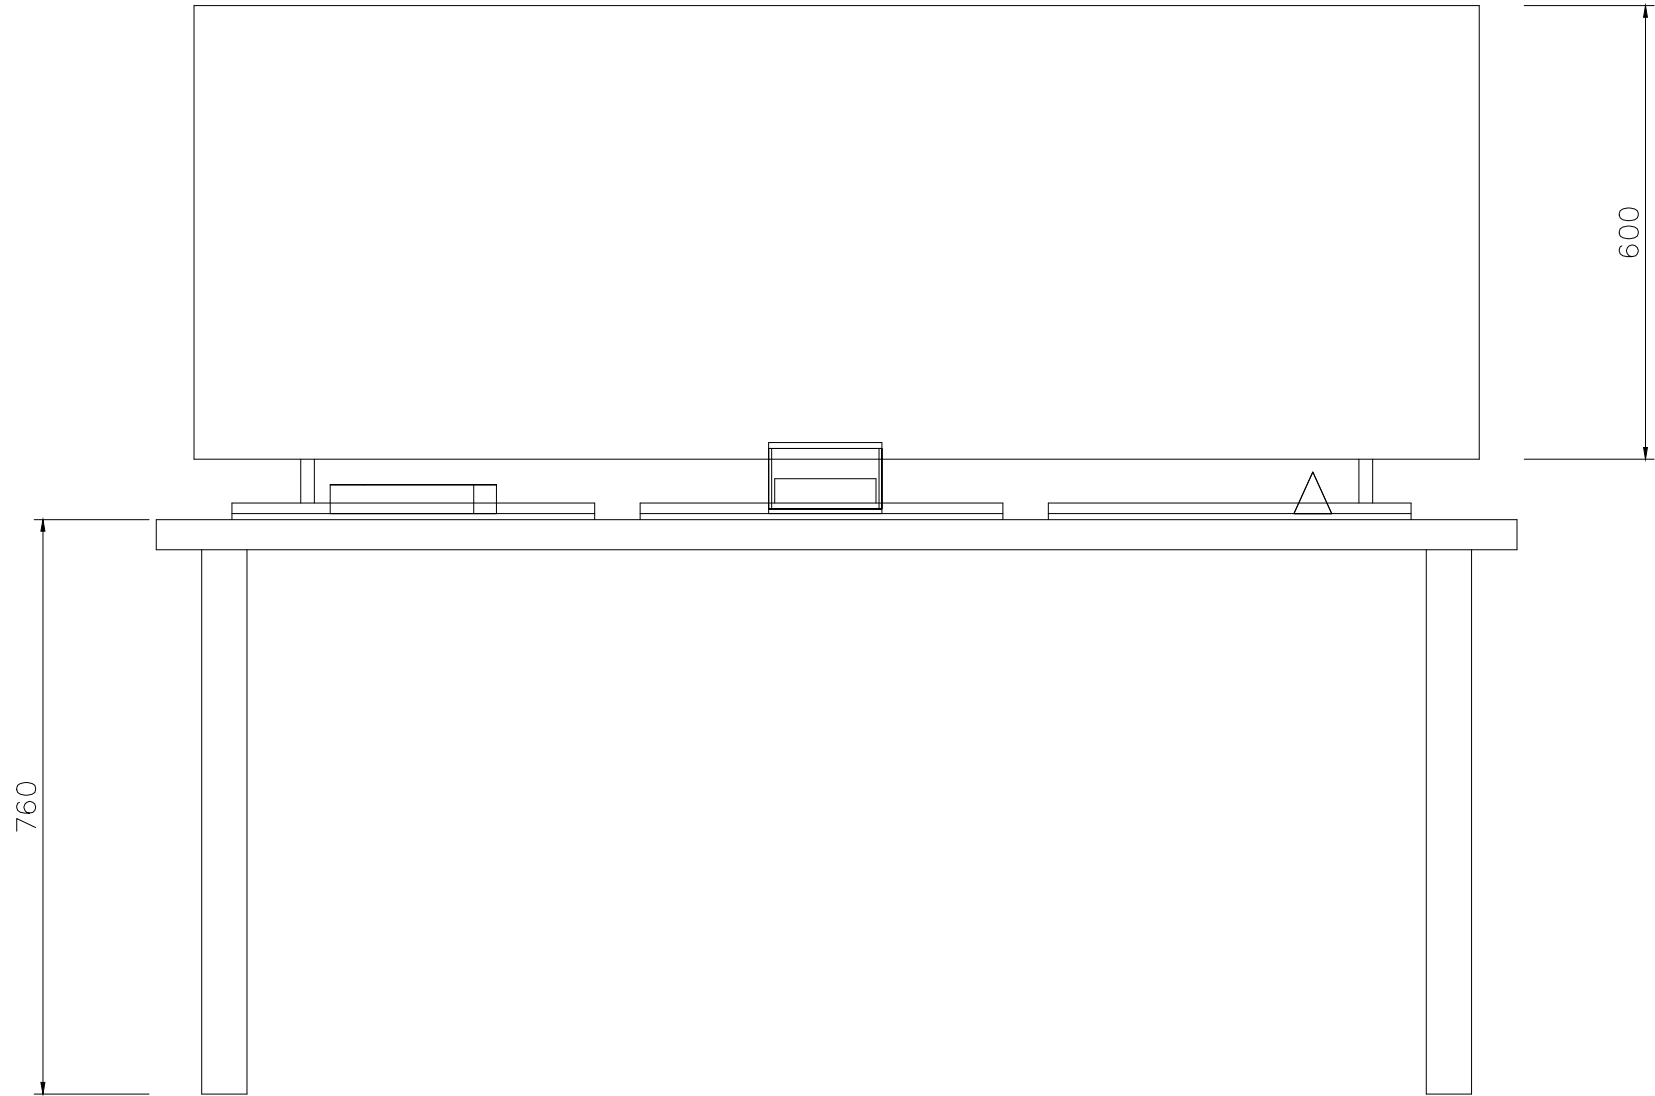


左至右：香材、封闭香粉罐、线香与塔香形态示意。
托盘480×380；无成分、纯度、等级或燃烧声明。

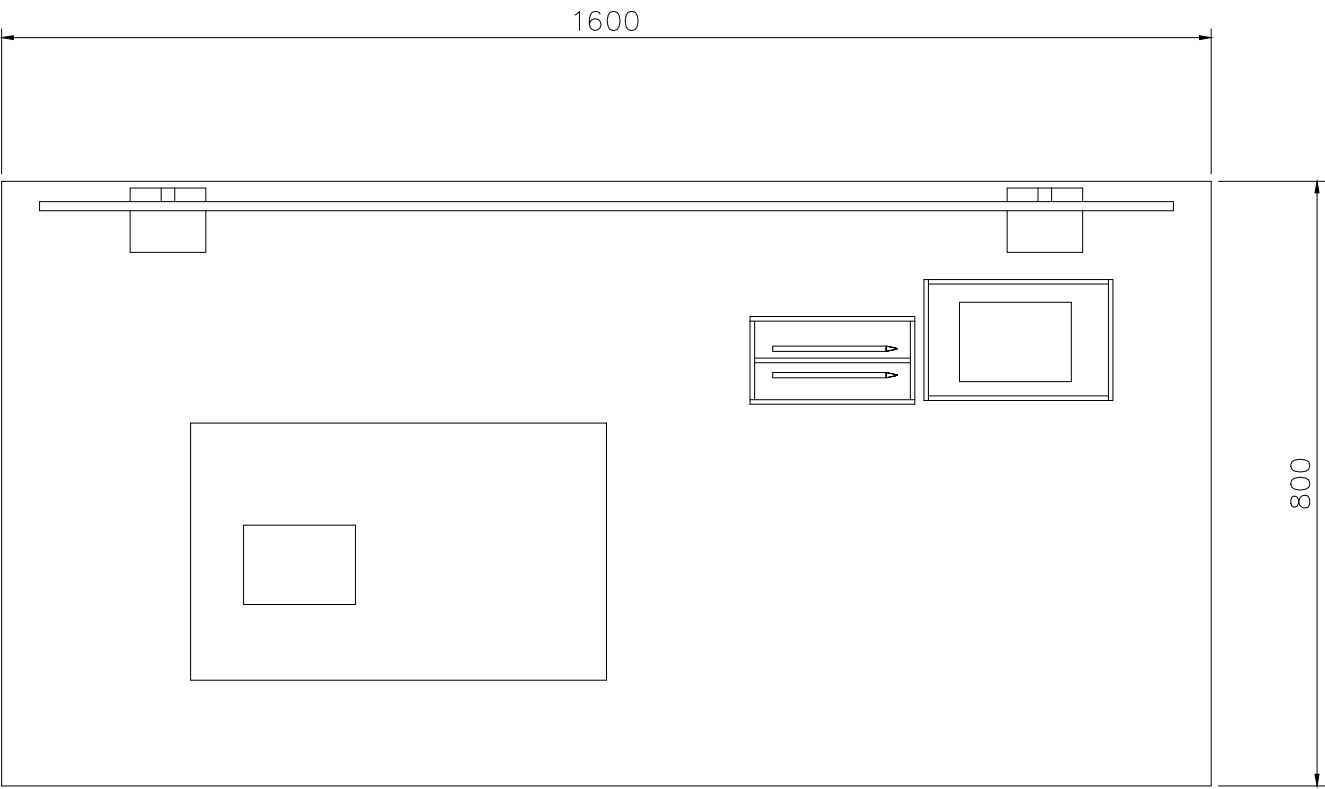

EX16 / 气味记录台面

观众侧立面 / 总高1540

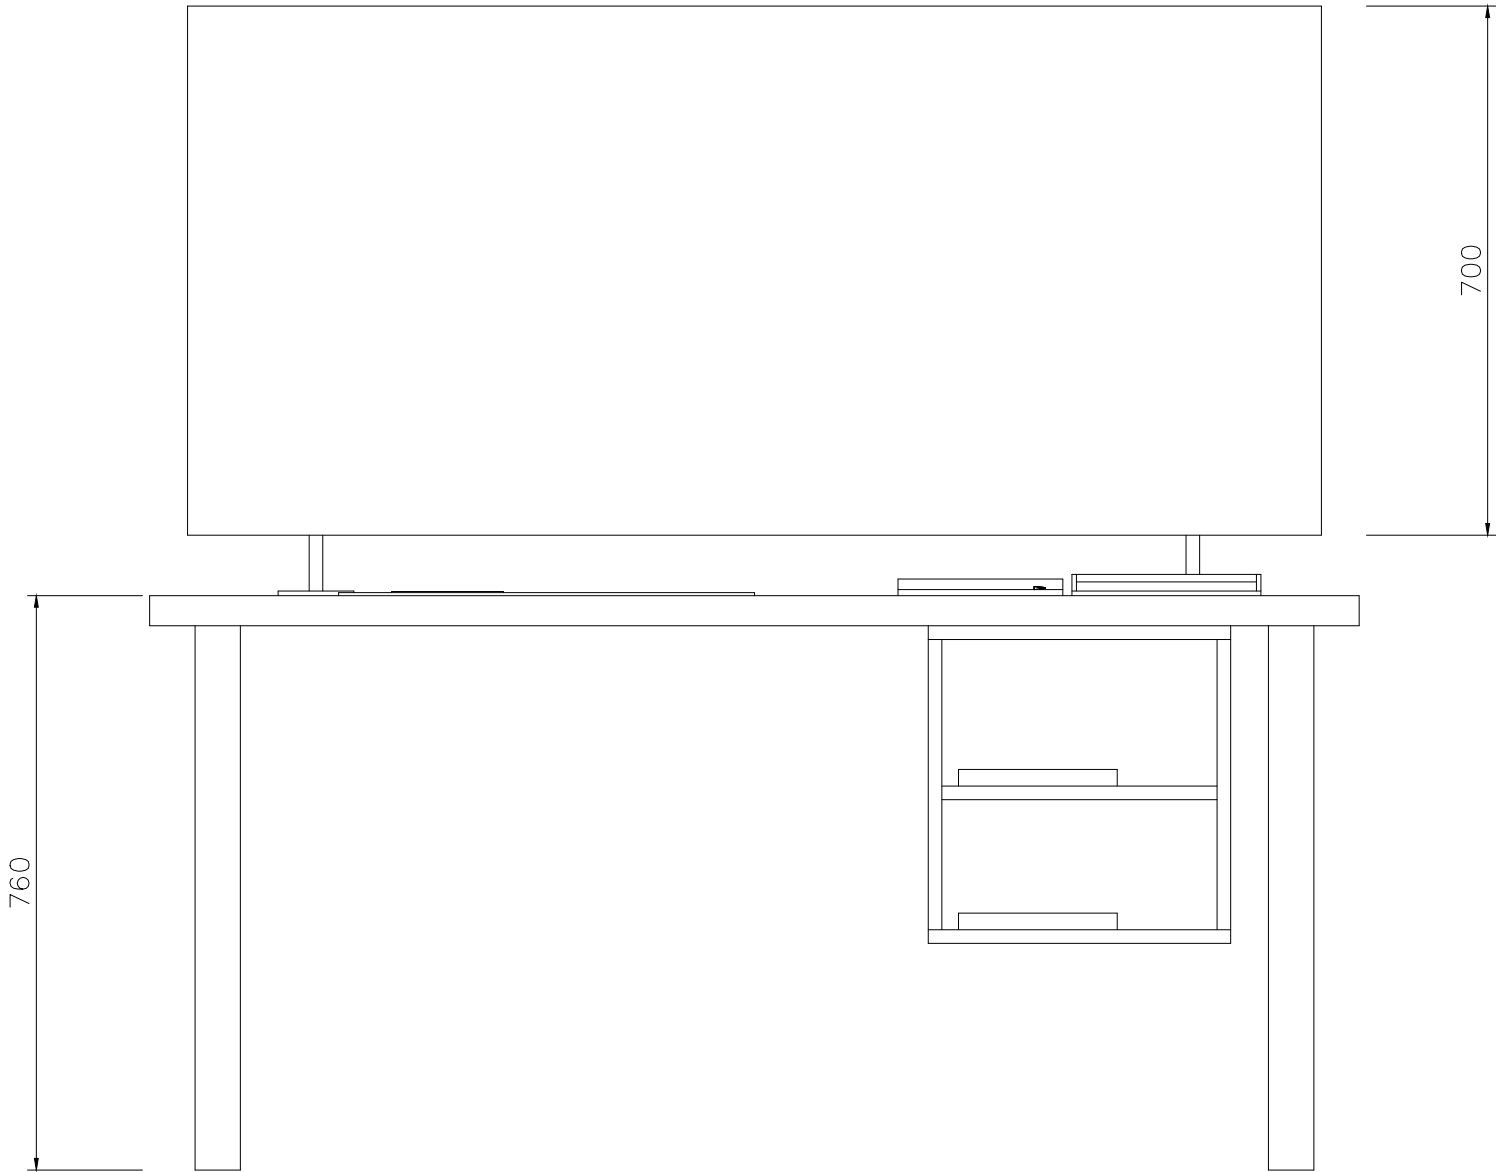

550×340书写垫、148×105空白卡、分格笔托。
保留下层纸张储备；新增记录卡不含虚构观众反馈。

传香 / 工坊与展面协调

站立观看手工艺示范：平面、四向展面与家具使用关系。



N / +Y



EX19 手工艺示范 / 台面900高

EX20 理香前后 / 台面850高

EX21 传承人展面 / 保留现安装位

EX22 学习成果 / 保留现安装位

EX23 培育保护 / 保留现安装位

EX24 知识回顾终端 / 入口侧保留


虚线框：演示者与观看区，不是实体隔断。

抽屉朝北：示范期间关闭，清场后逐个开启。


台面工具、样件是原创教学示意。

展板图文与标识尺寸见展陈图文分册。


A 北向 / 由南看北 / 1:50

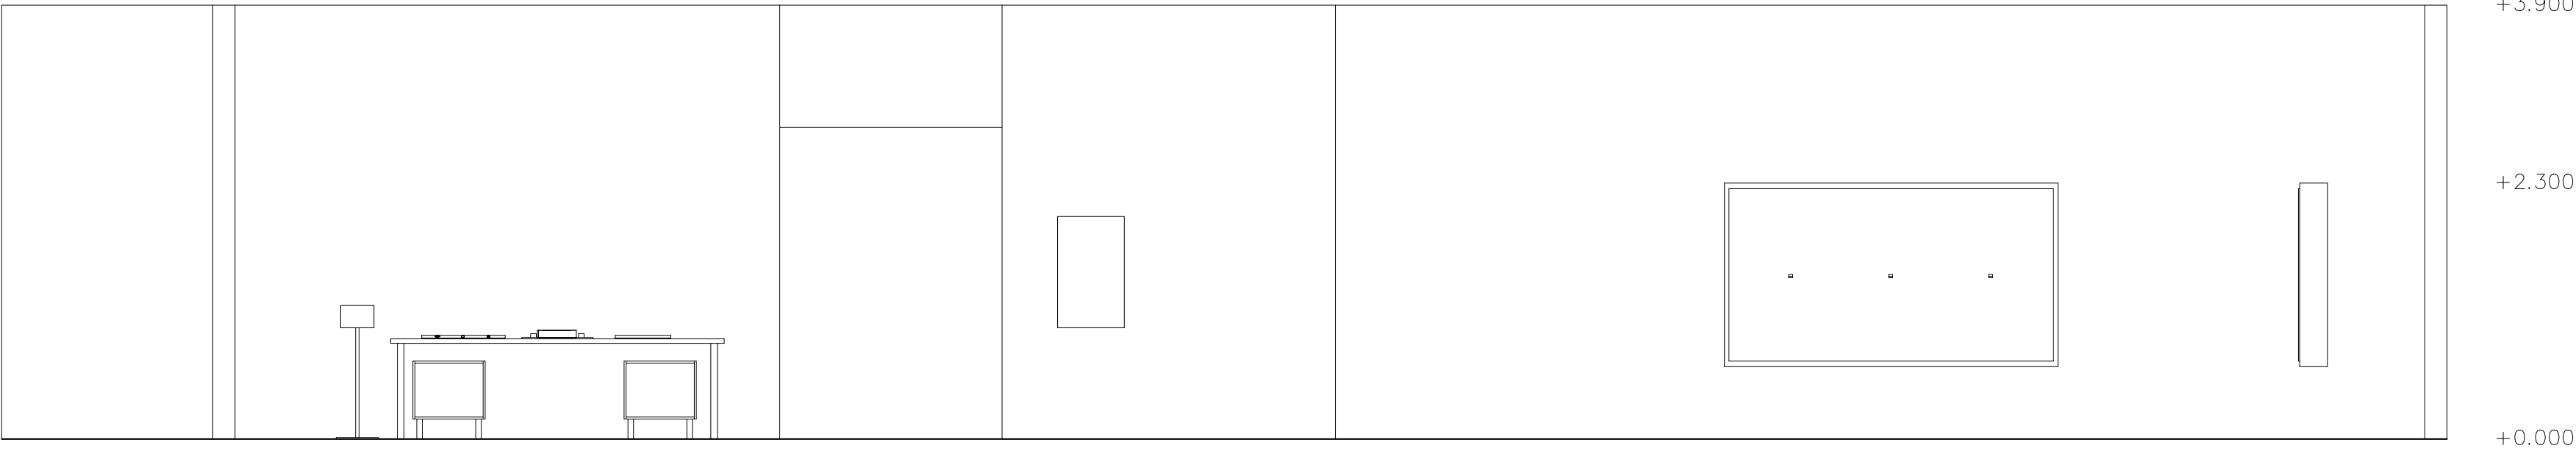


B 南向 / 由北看南 / 1:50

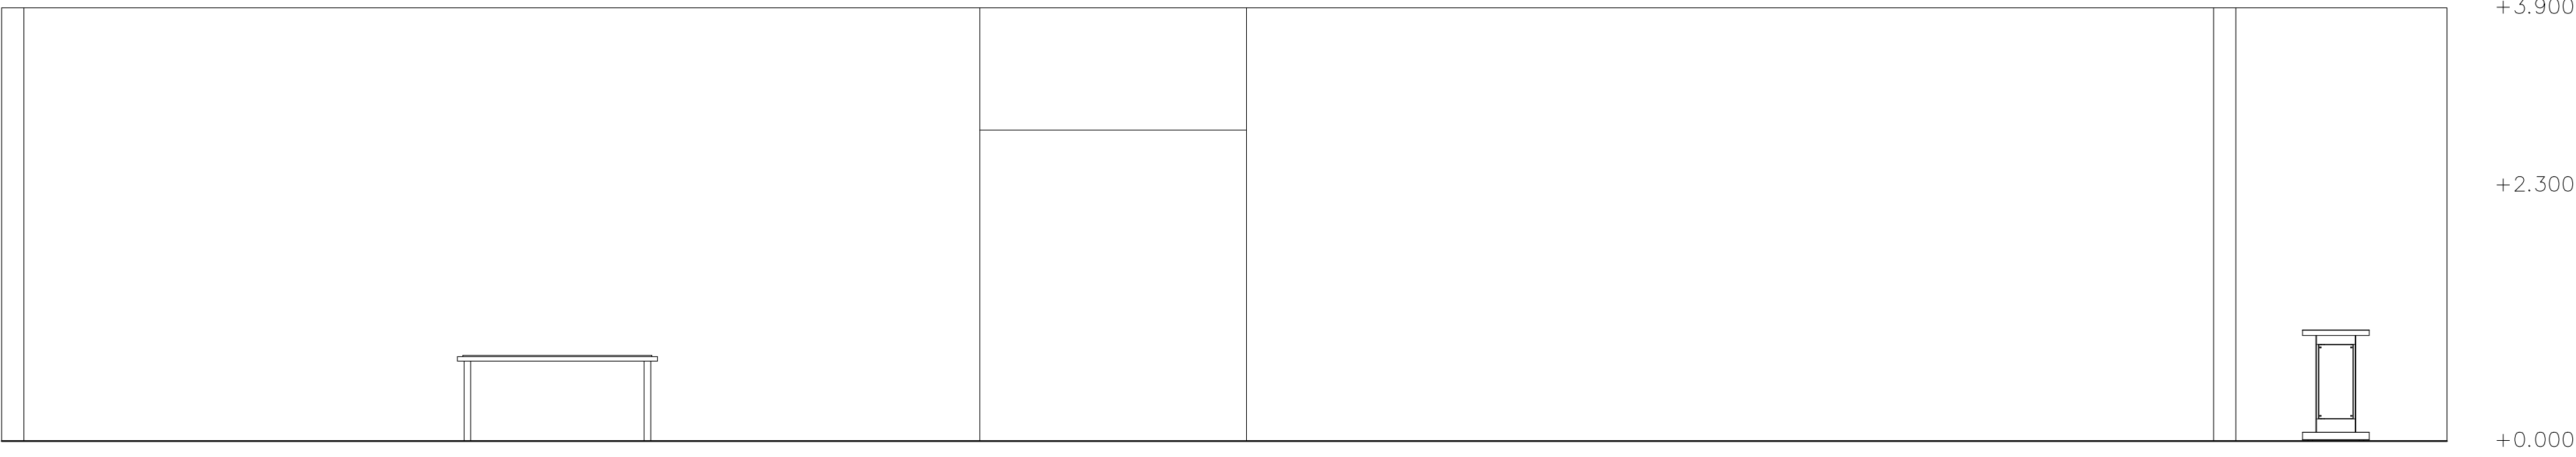

C 东向 / 由西看东 / 1:50

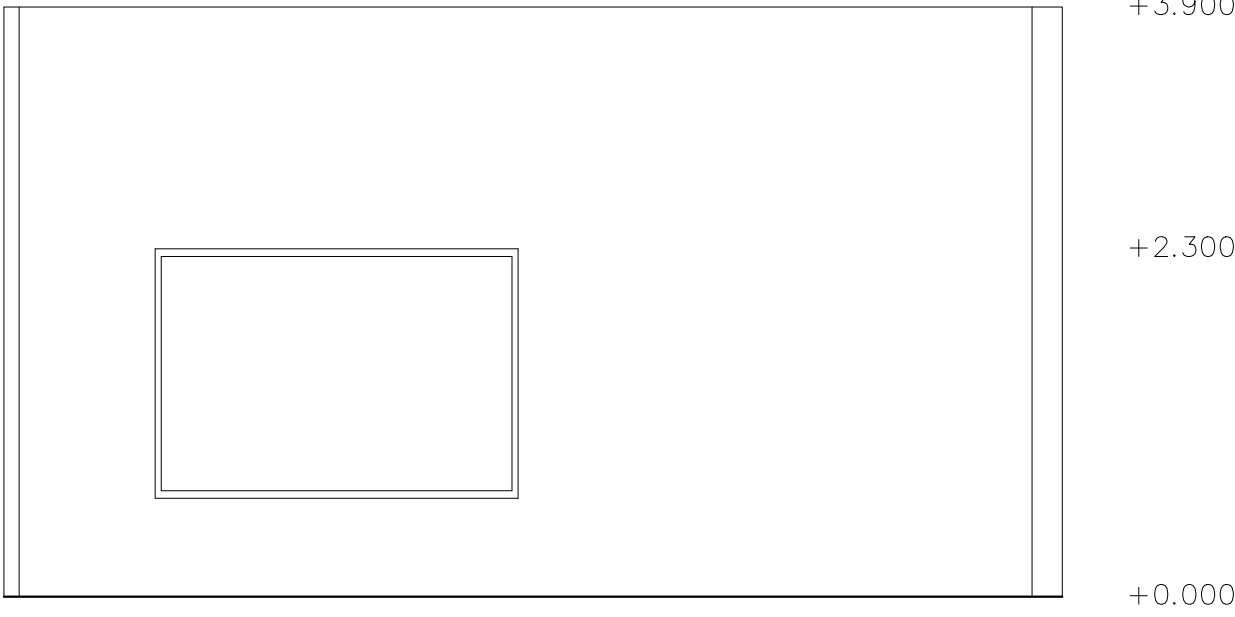


D 西向 / 由东看西 / 1:50

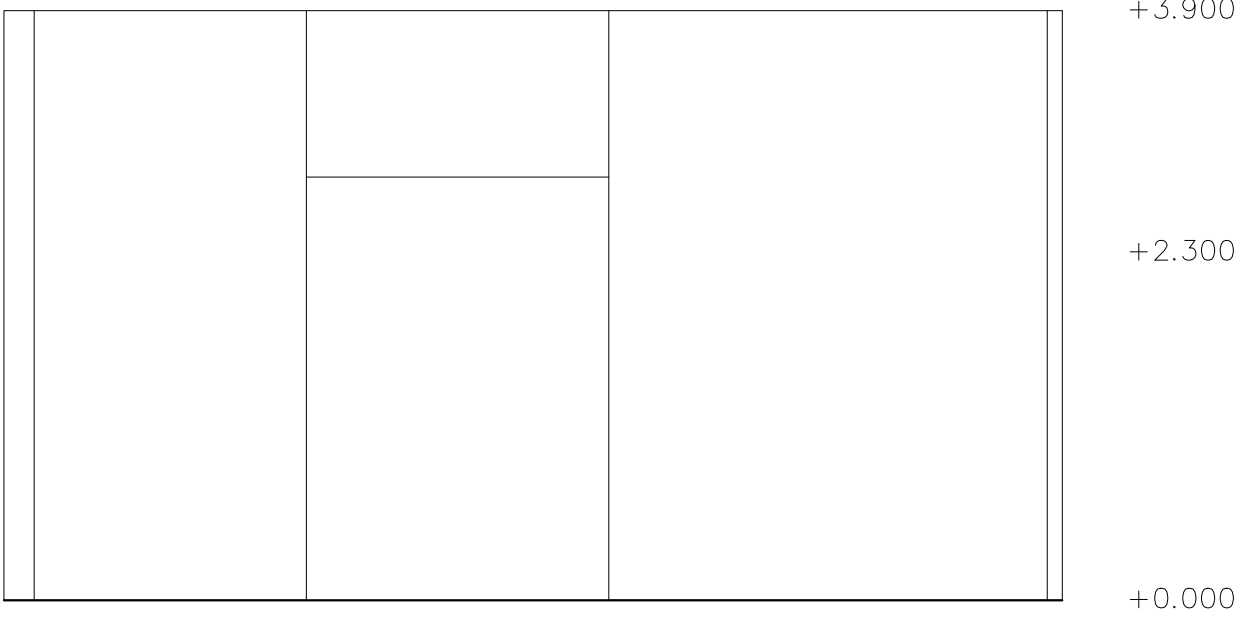

立面按注明深度带绘制；门扇、顶面与安装高度见D02/D05/D07，展项合并外包见D03。


EX19 / 手工艺示范台

示范台本体3000×800，台面900高；图示工具与材料为教学示意。

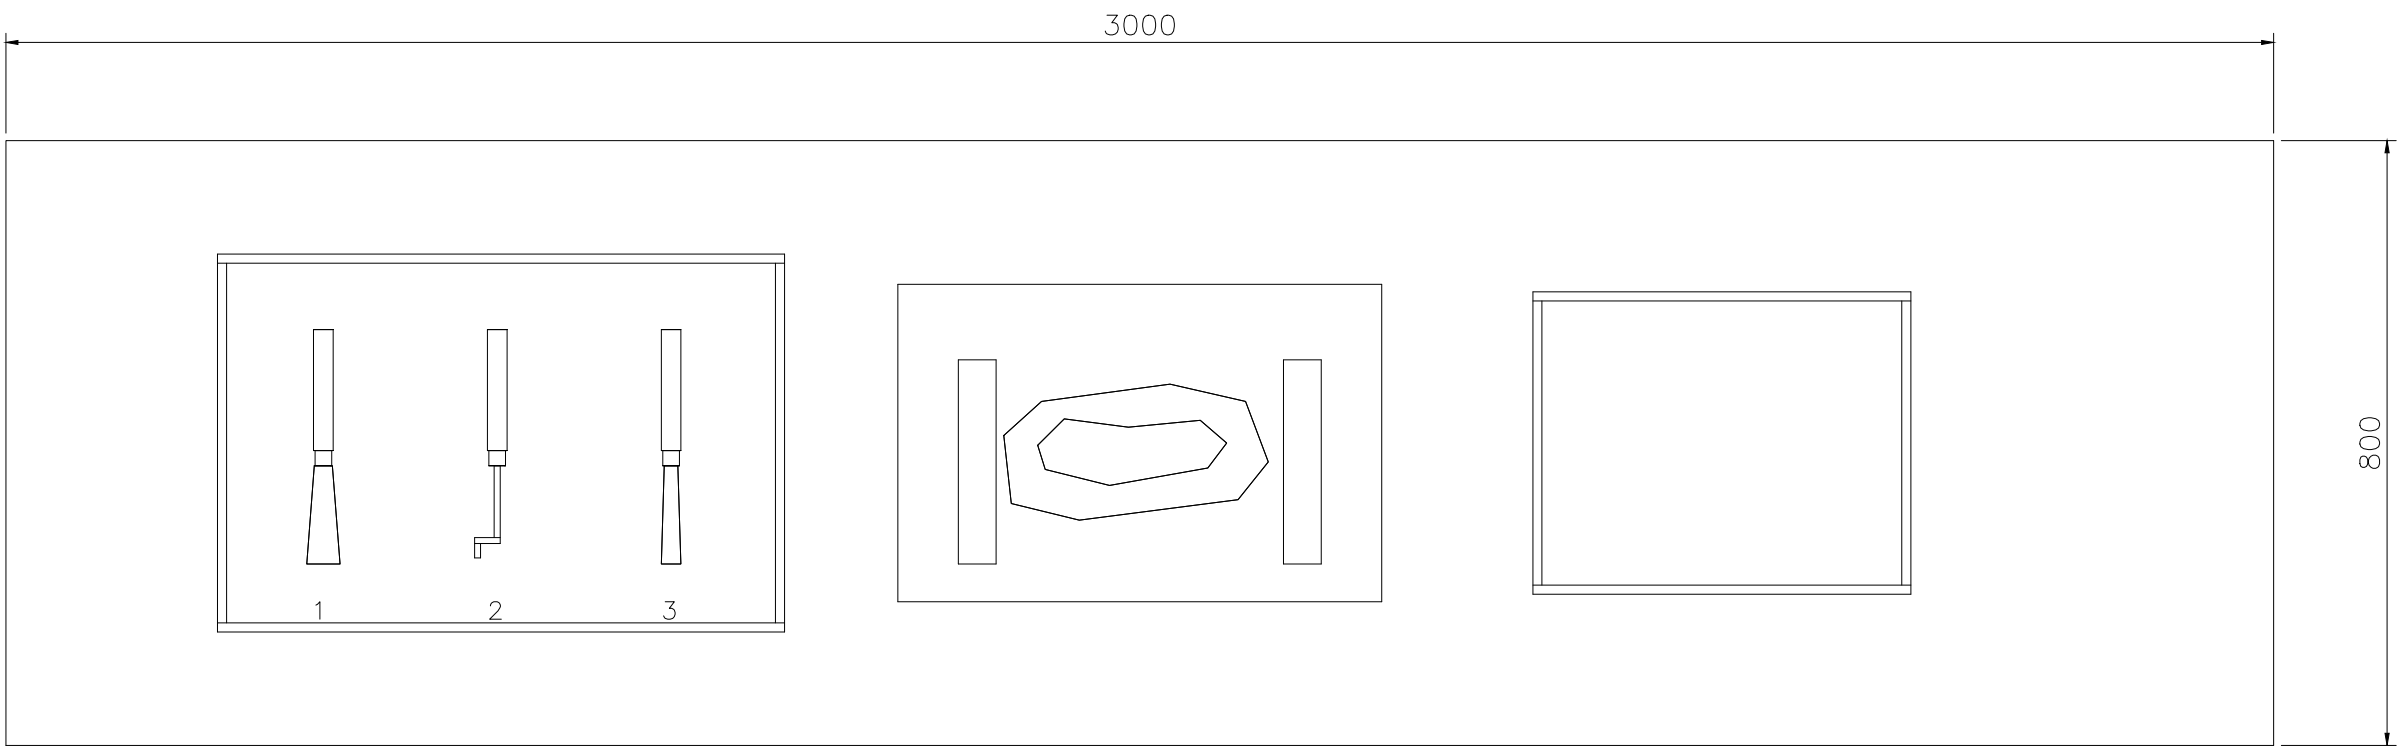

01 台面 / 北为演示者，南为观众

02 观众侧立面 / 储物正面向北侧

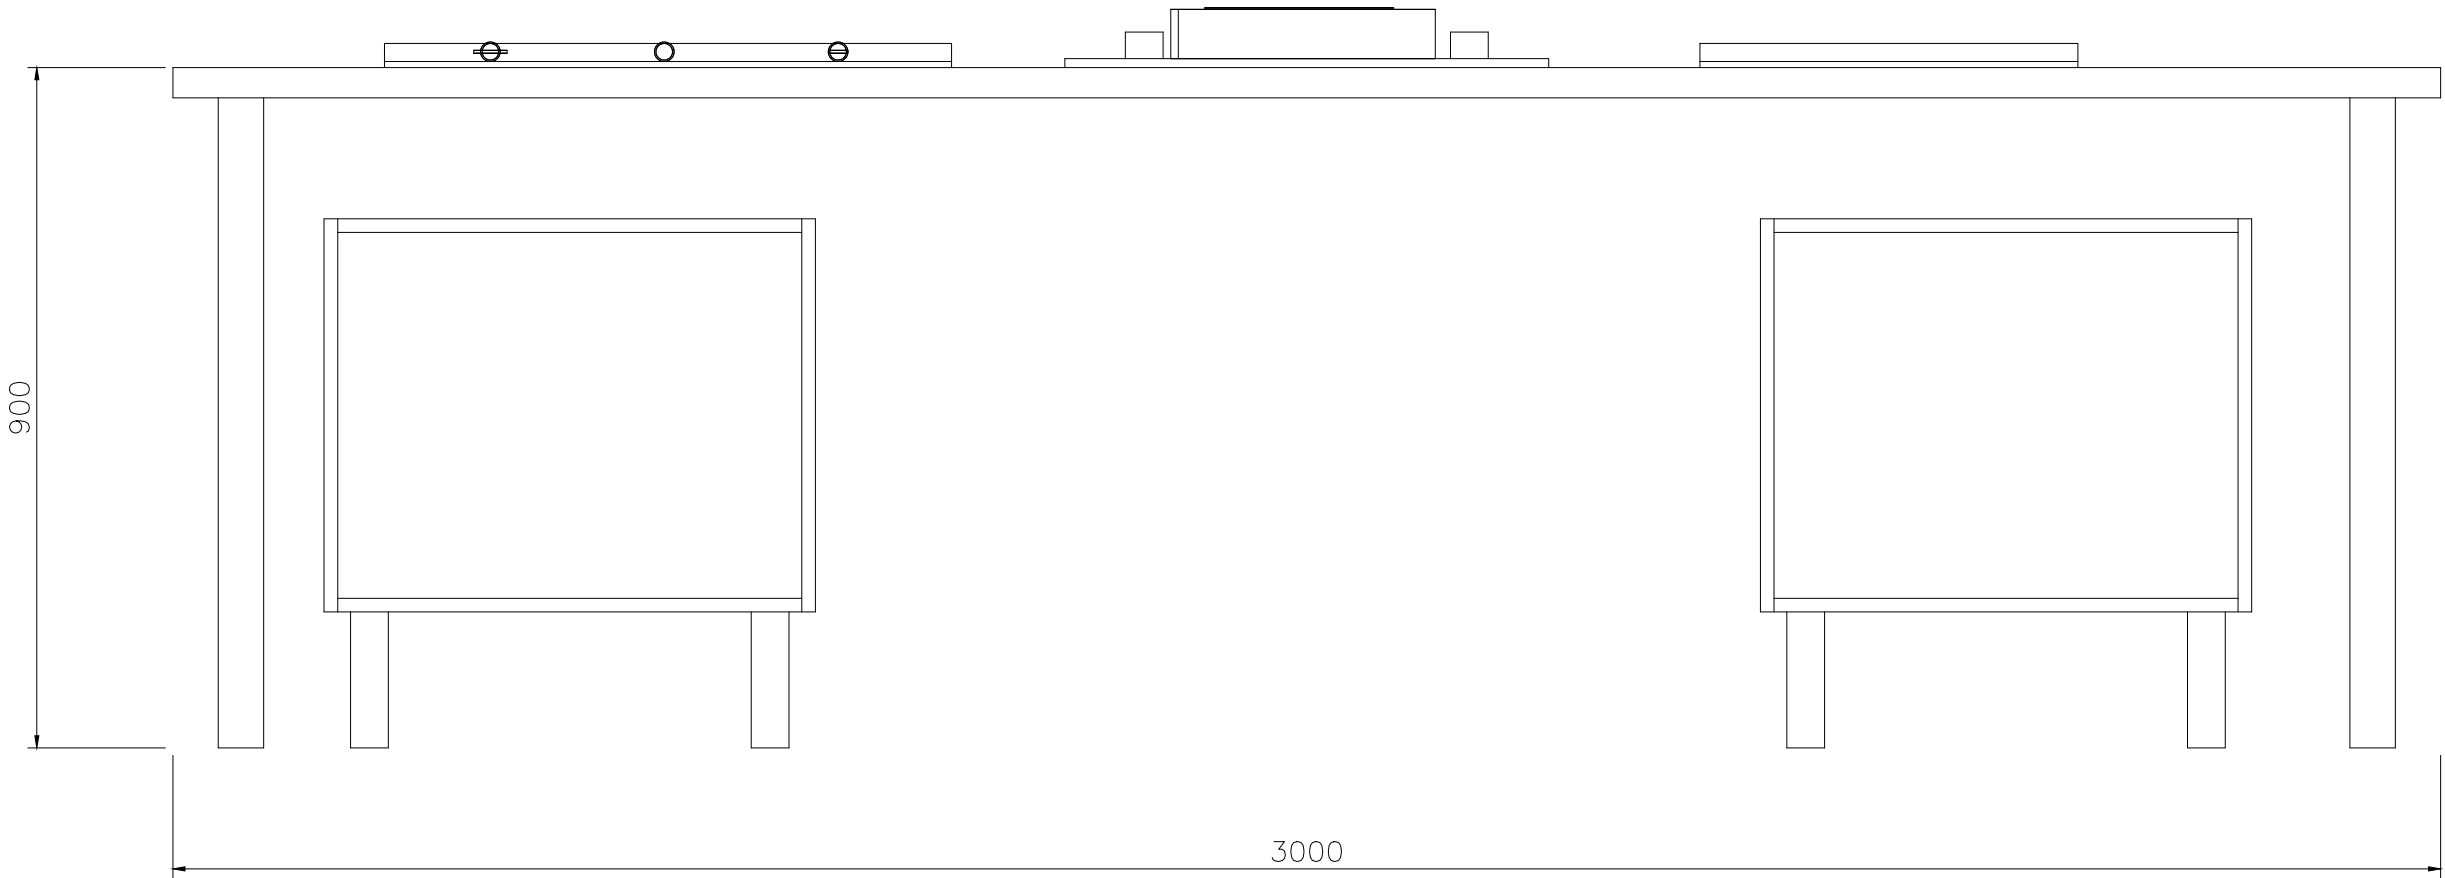

台面及腿架沿用已确认尺寸。储物柜与台腿落地独立；五金、承载及制造连接待进一步落实。

左：750×500可取工具托盘。

1 铲刀 / 2 勾丝刀 / 3 凿子。

中：640×420示范垫，低位托块定位。

右：500×400接料托盘。

工具尺寸/轮廓为原创概括示意，

工具名称见对应图文说明。

材料深浅色表示拟保留部位；

不代表实测树脂分布或等级。

抽屉6个，均朝演示者侧开启。



每个行程300，示范期间保持关闭。

本页不提供真实工具使用姿势。

托座实际夹紧方式由演示者复核。

储物 / 演示者侧抽展开启

纵剖面X=22025；方向南→北。最上层单抽展开启；支脚为后方投影。

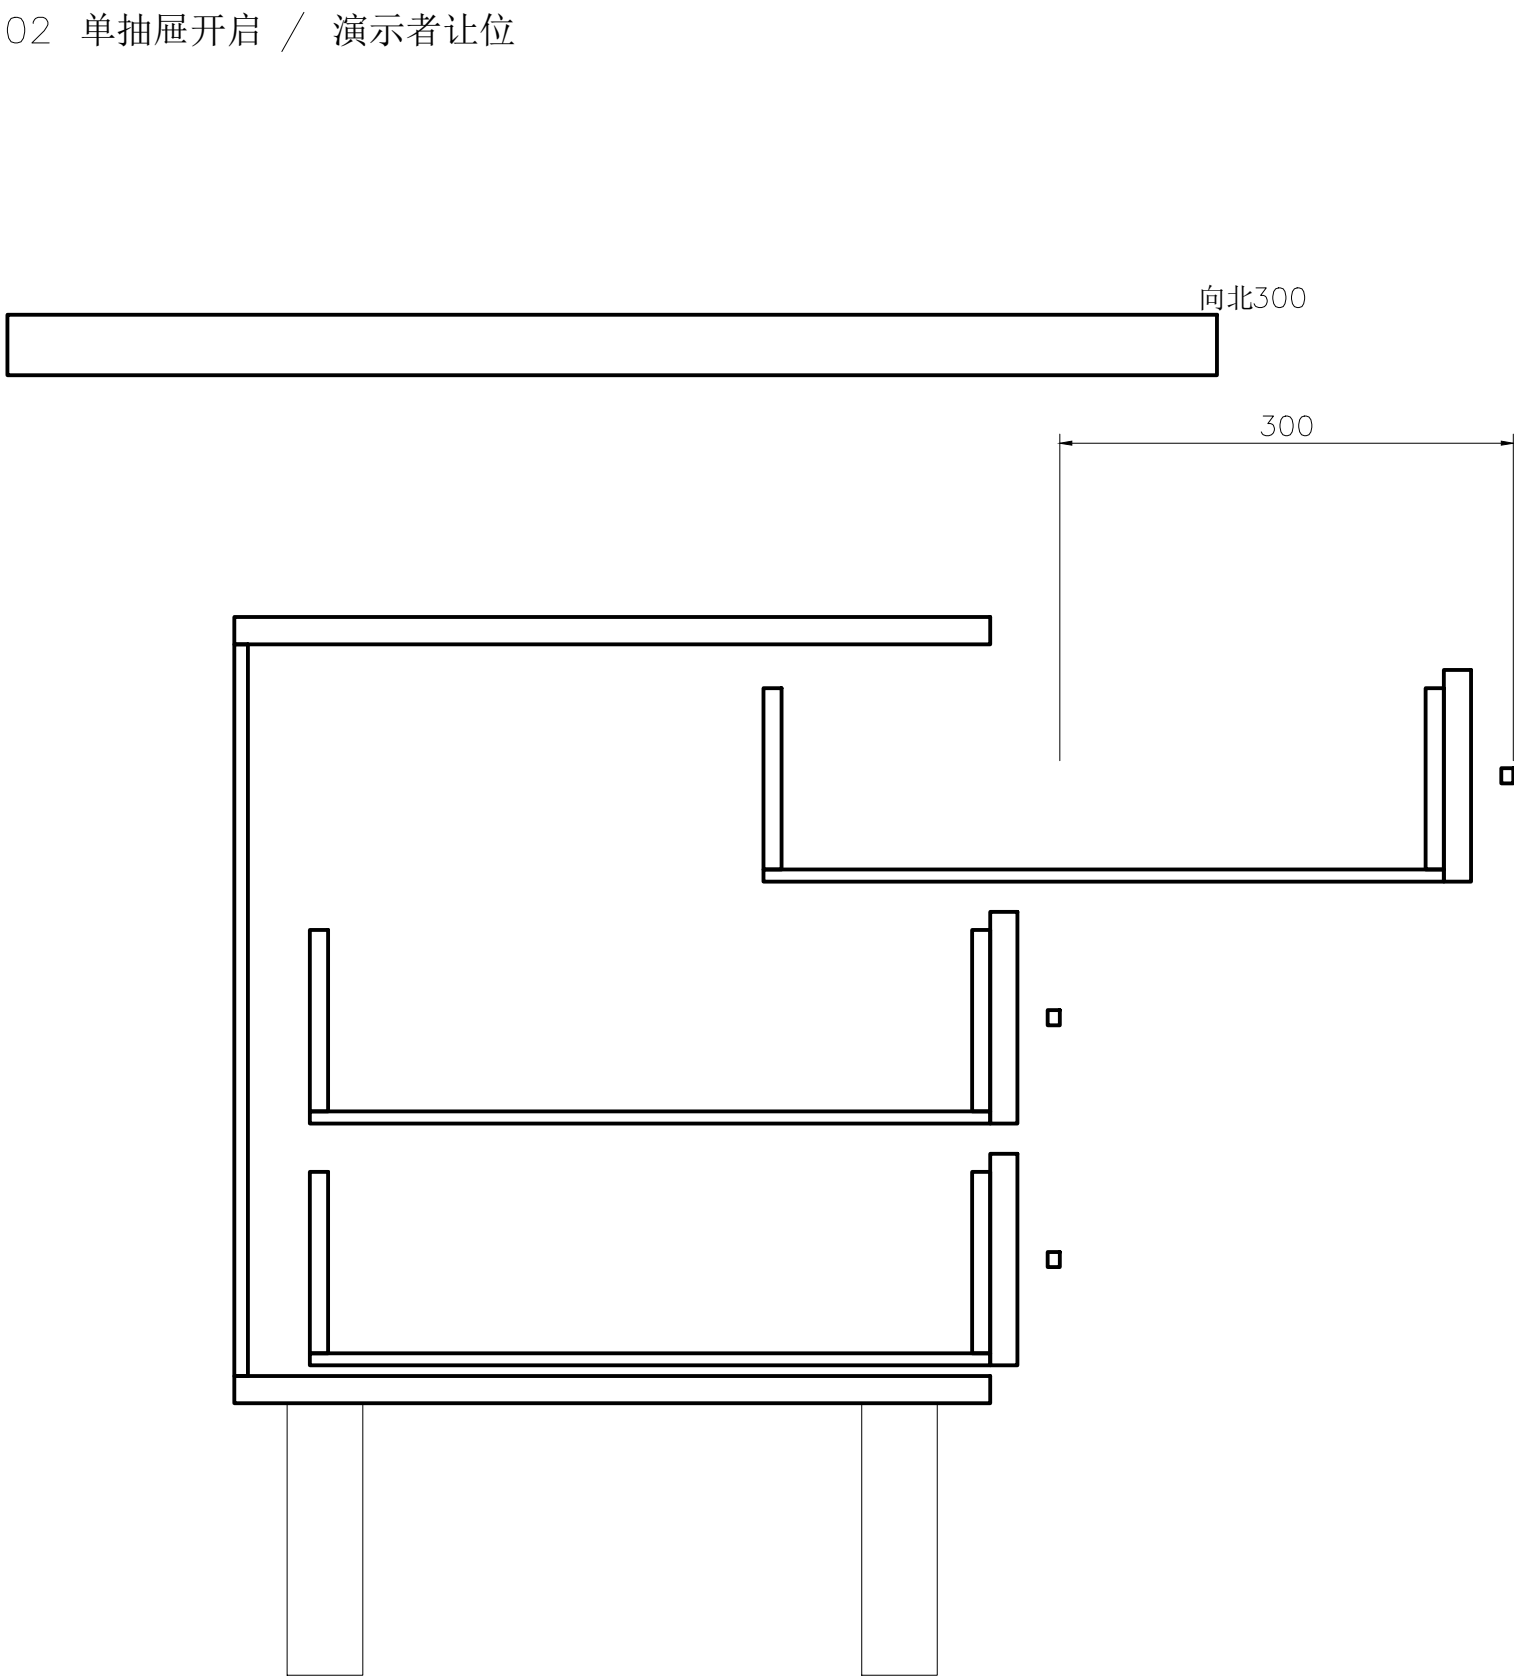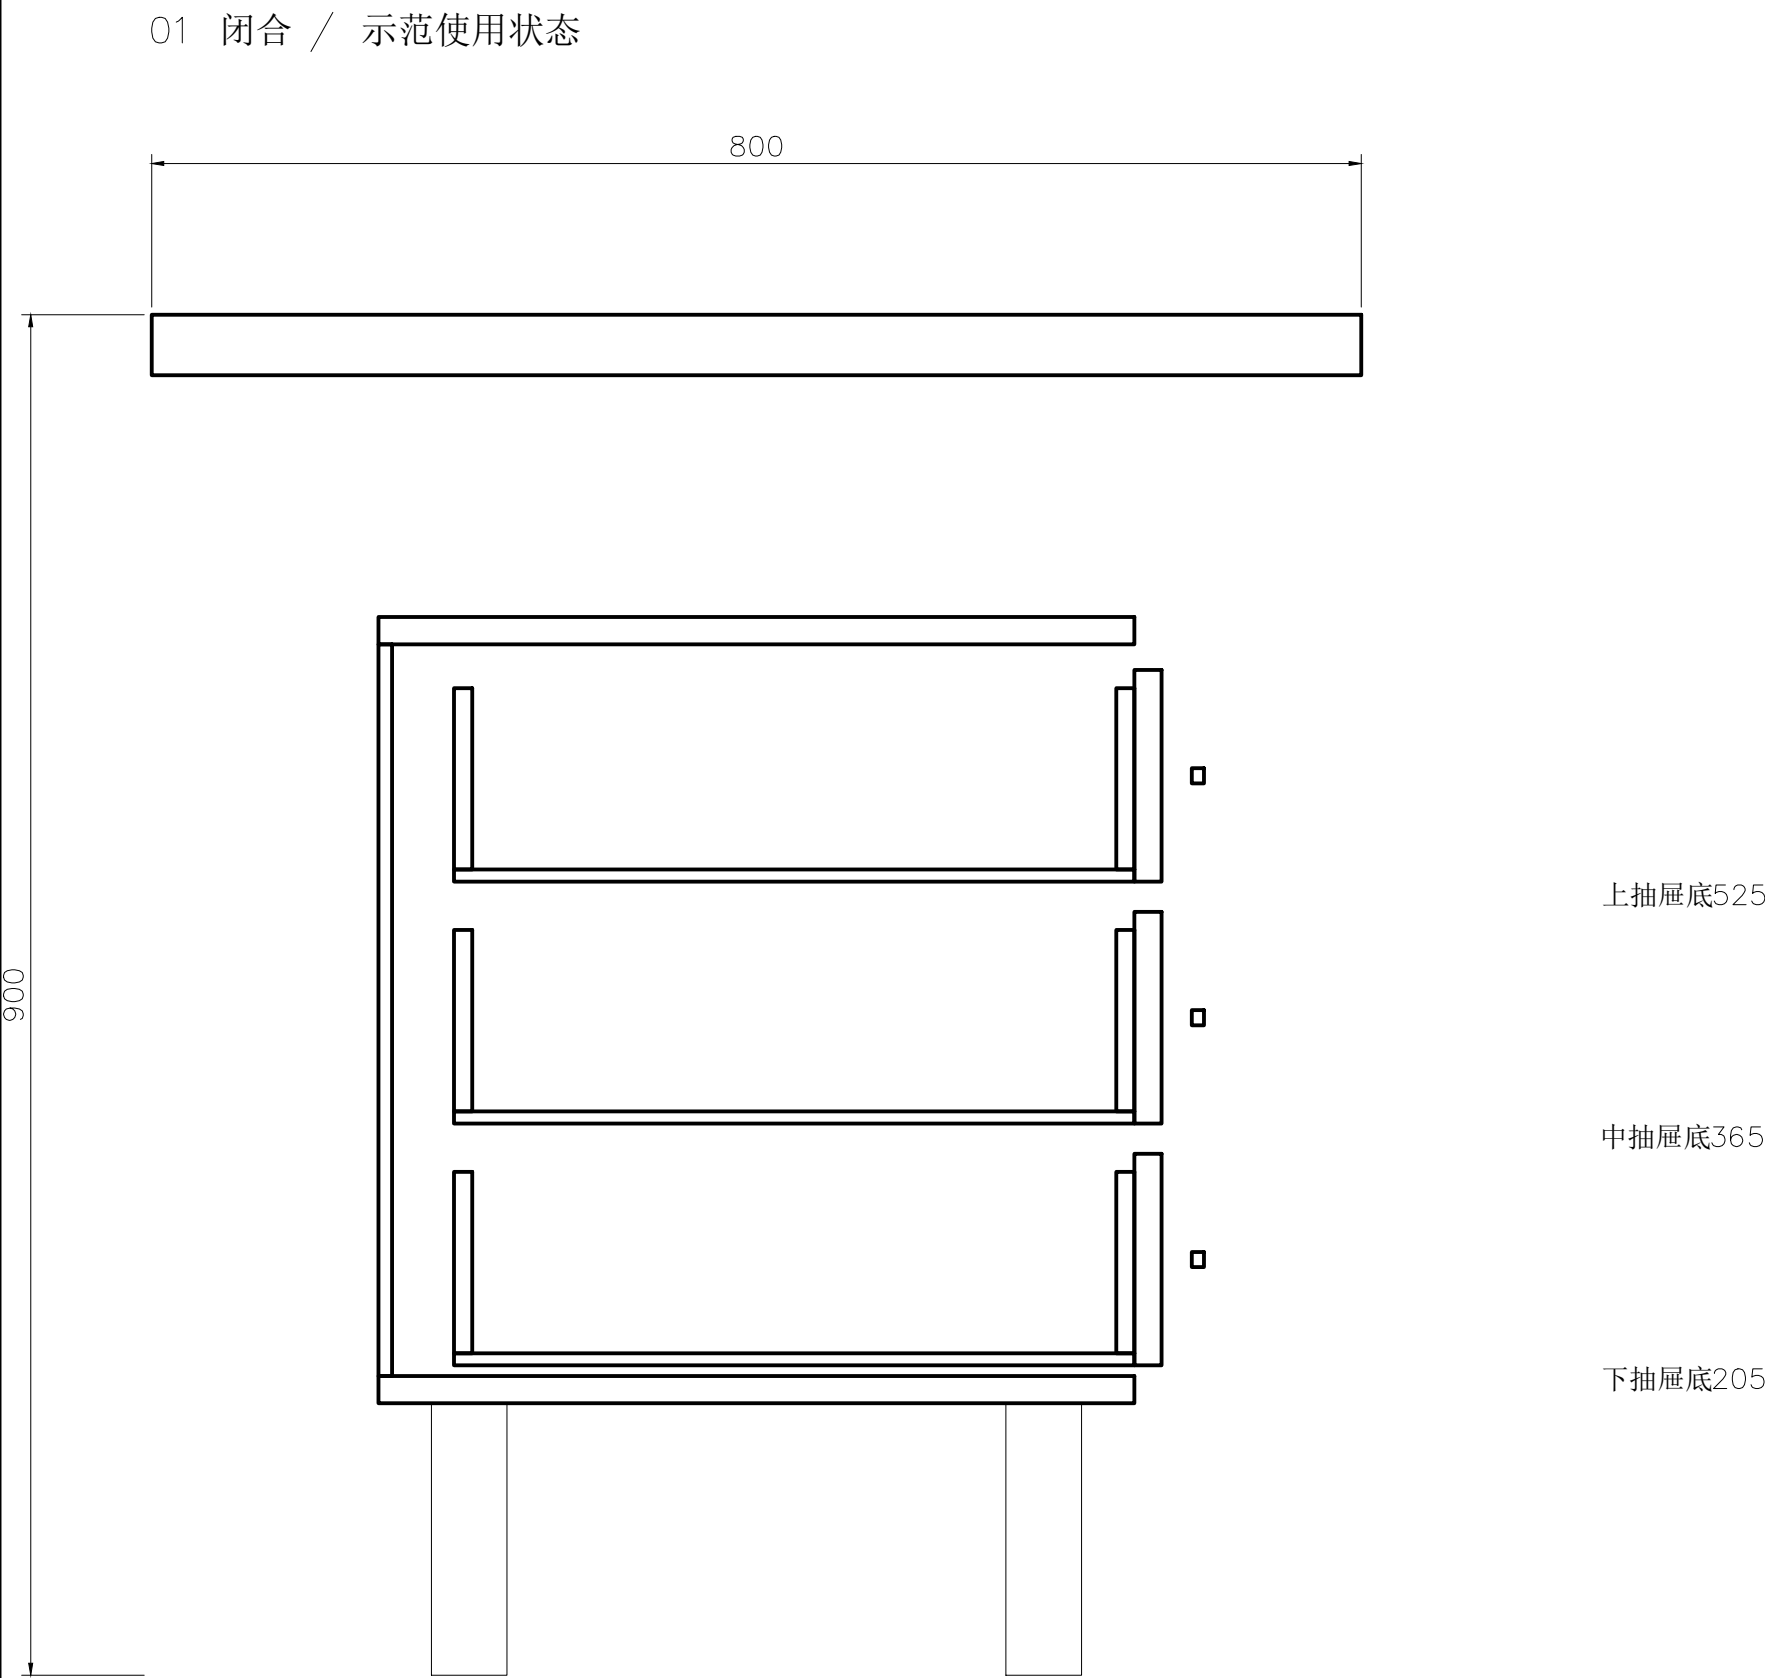


18柜体板 / 9背板 / 8抽屉底 / 12盒壁 / 18面板，单位mm。柜体650×500×520，底标高180。

固定及移动导轨仅为空间包络。全开剩余重合130；实际滑轨、承载、防脱、限位和连接未选型。

最大北端Y=6096，至演示区北边界6900余804。逐个开启；该余量不是通行或人体使用合规结论。

EX20 / 理香前后辅助比较

辅助台本体3000×800，台面850高；承接站立示范，供近看样件与工具说明。

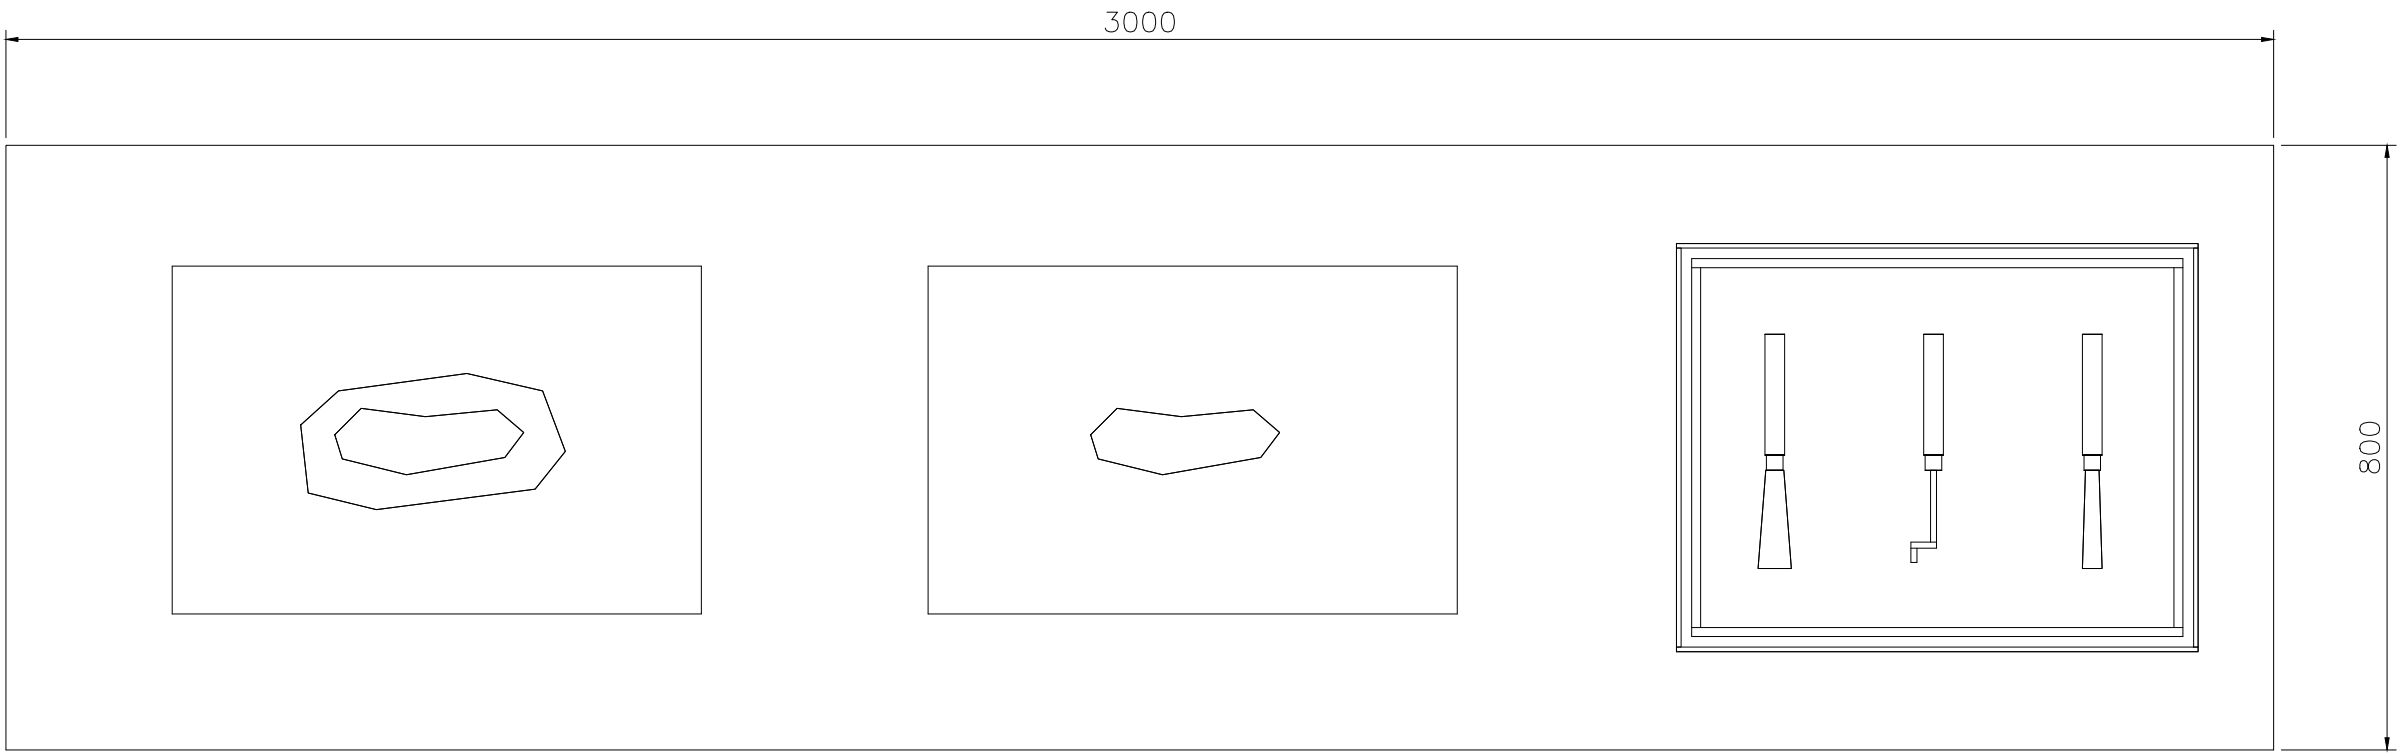

01 台面 / 左处理前 · 中拟保留部位 · 右工具示意

两件材料用共同轮廓表达去木留香，

示意关系不对应已征集的真实标本。



工具罩690×540，壁/顶6厚；

可取下展示，实际连接和材料待选。

无观众动刀、加热或实操课程。

03 代表性视线 / EX19

02 观众侧立面 / 保护罩含顶板总高206

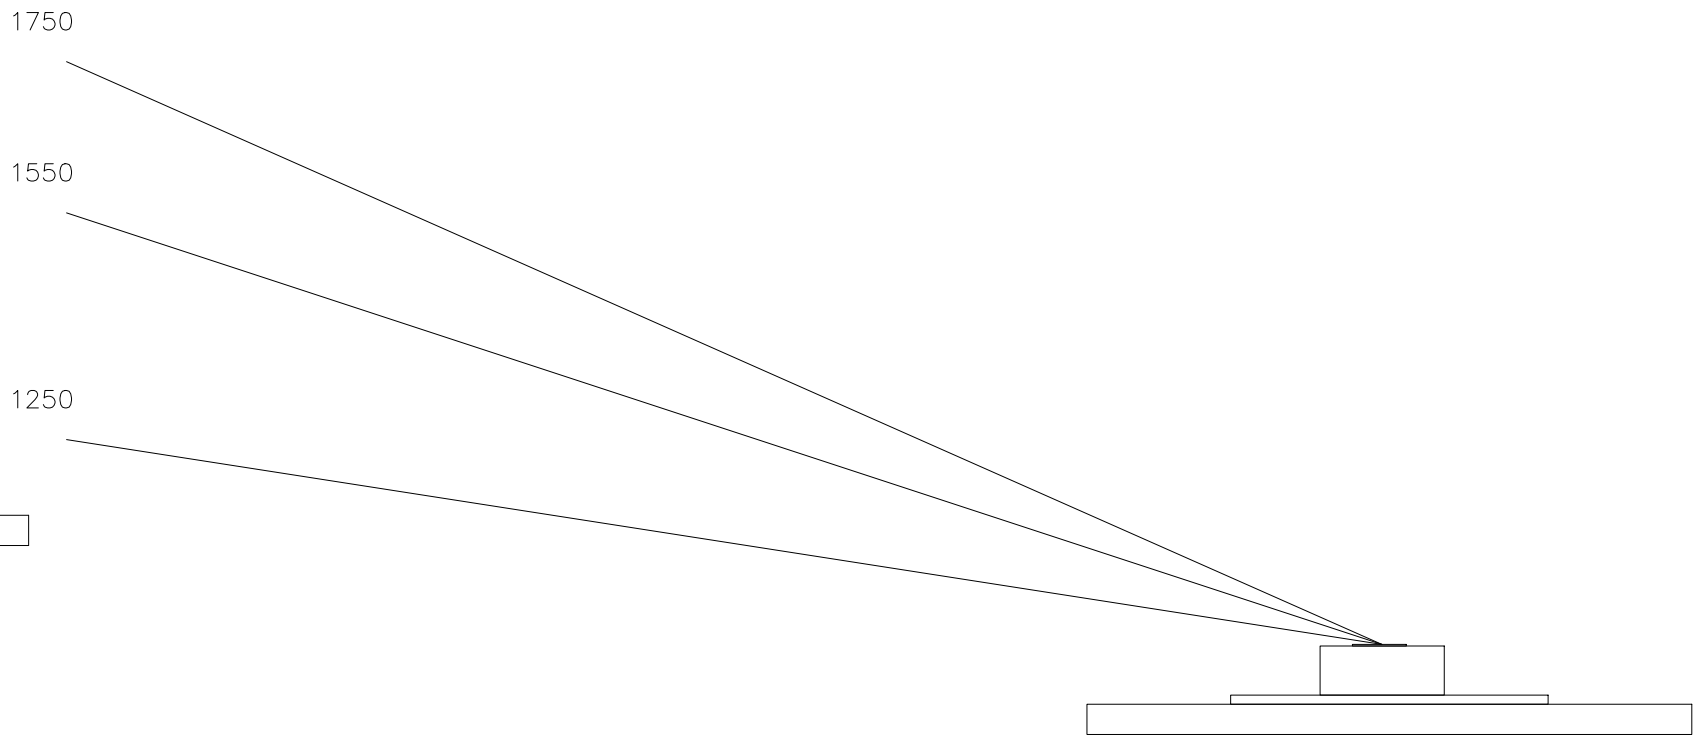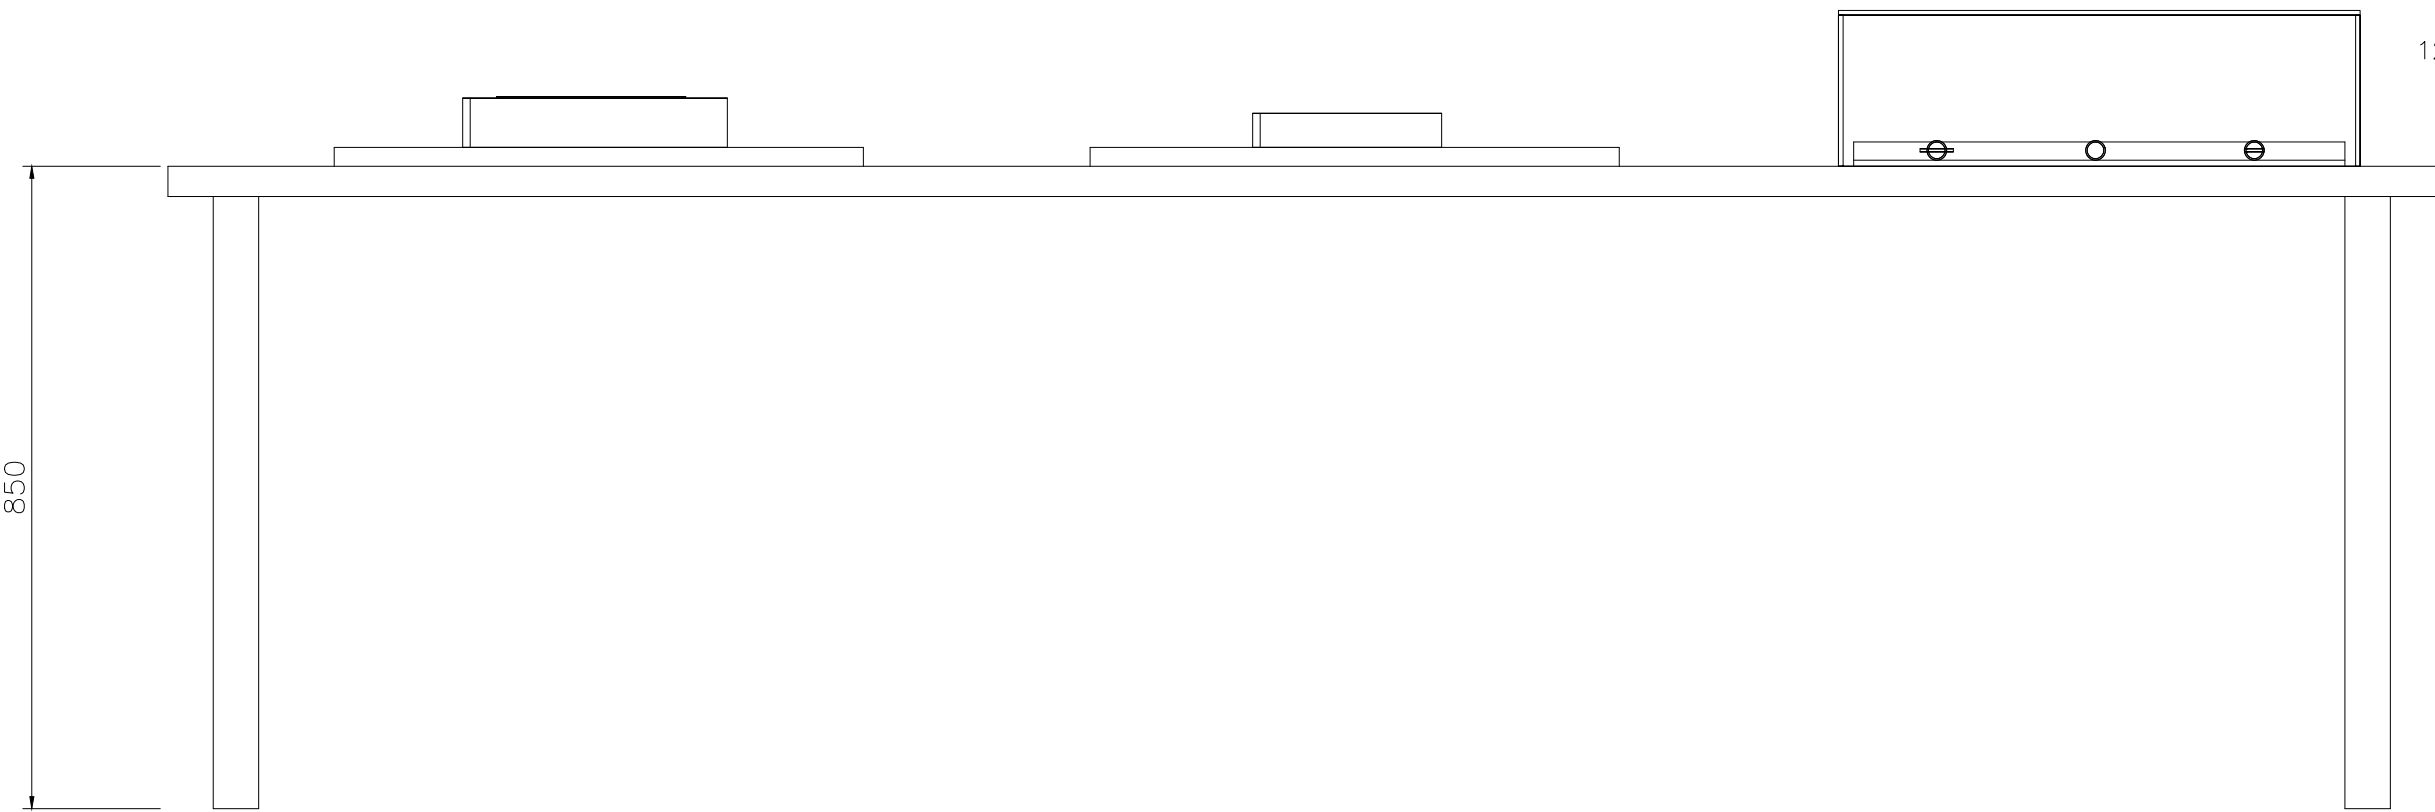


工具、材料和保护罩为教学示意；独立标识位置见总平面，图文见展陈分册。

眼高1250/1550/1750至样件。
图中无演示者手臂或人群；
24条代表线检查不代替现场体验。

EX09北墙16列×6行 / 屏体定位与支承组织

屏体与支承定位；截面及连接为空间协调预留。尺寸mm；标高m。

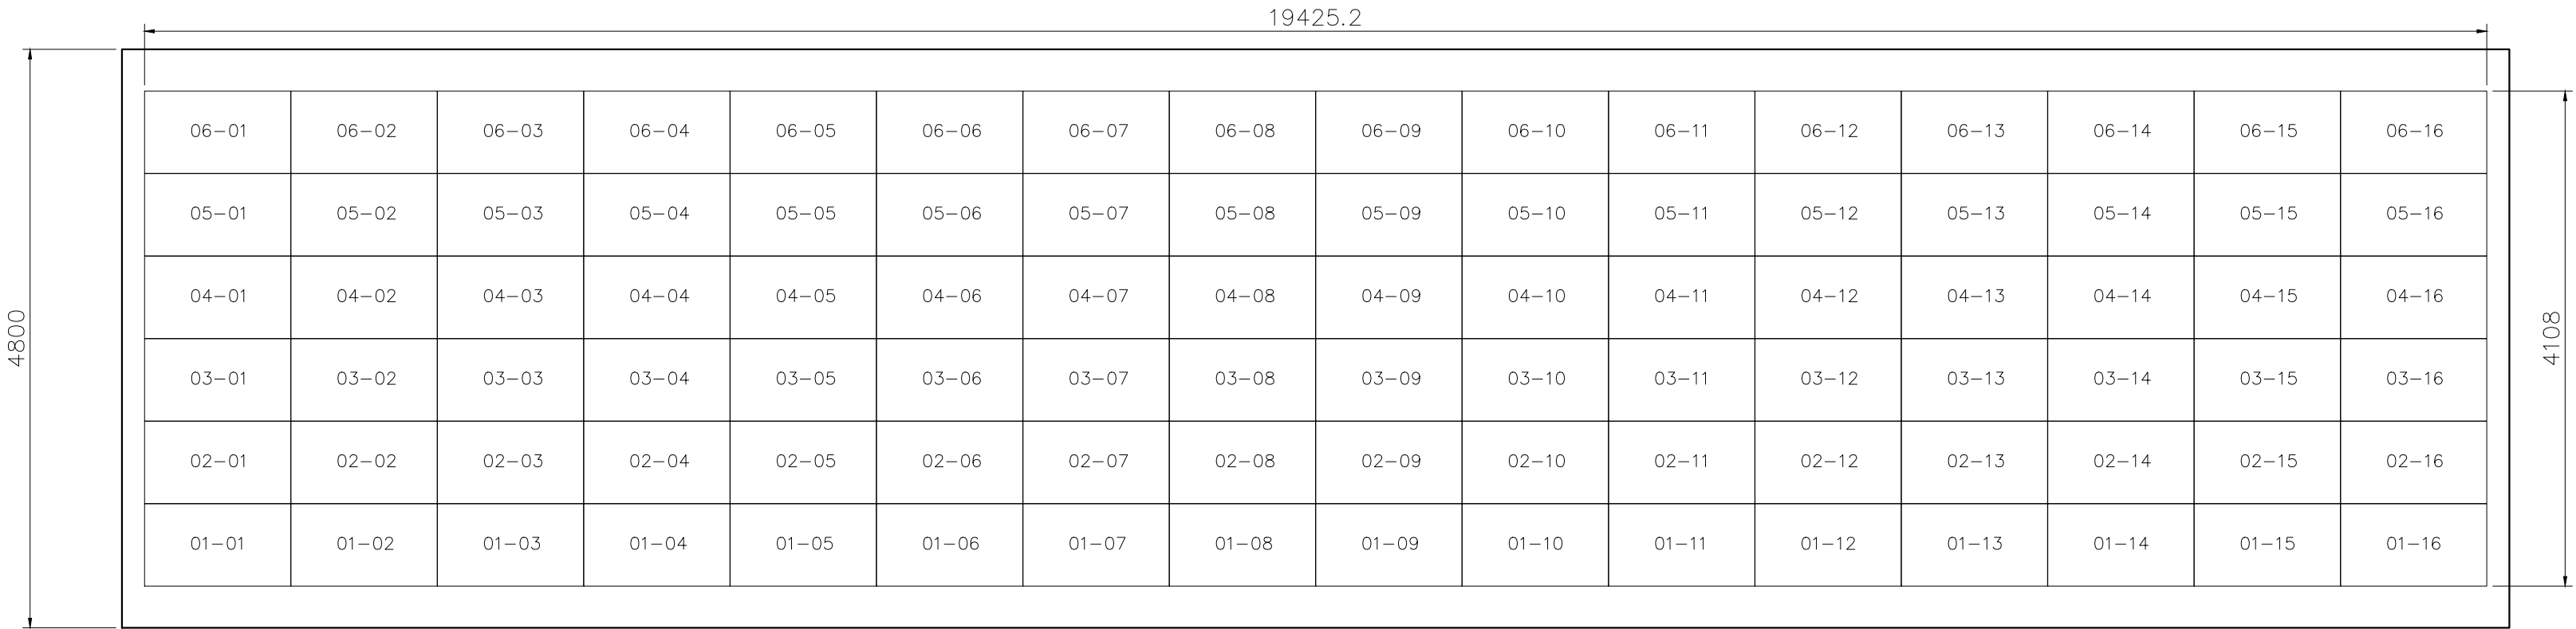

96台 LG 55VH7J-H 尺寸参考

单机1212.2×683×86.9

屏阵19425.2×4108

X=10287.4~29712.6

Y屏体前=28450

Y屏体背=28536.9

北墙内面Y=28800

两侧控制余量各187.4

下部和顶部各346

留空观看区方向不变

周边余量按19800控制宽计算；


西侧局部实际开放，不增造墙。

墙后≥200、周边≥100为参考值。

几何距离满足上述数值；

气流组织及冷却性能仍待验证。

支承正投影 / 隐去屏体与活动支架，表达安装承接关系

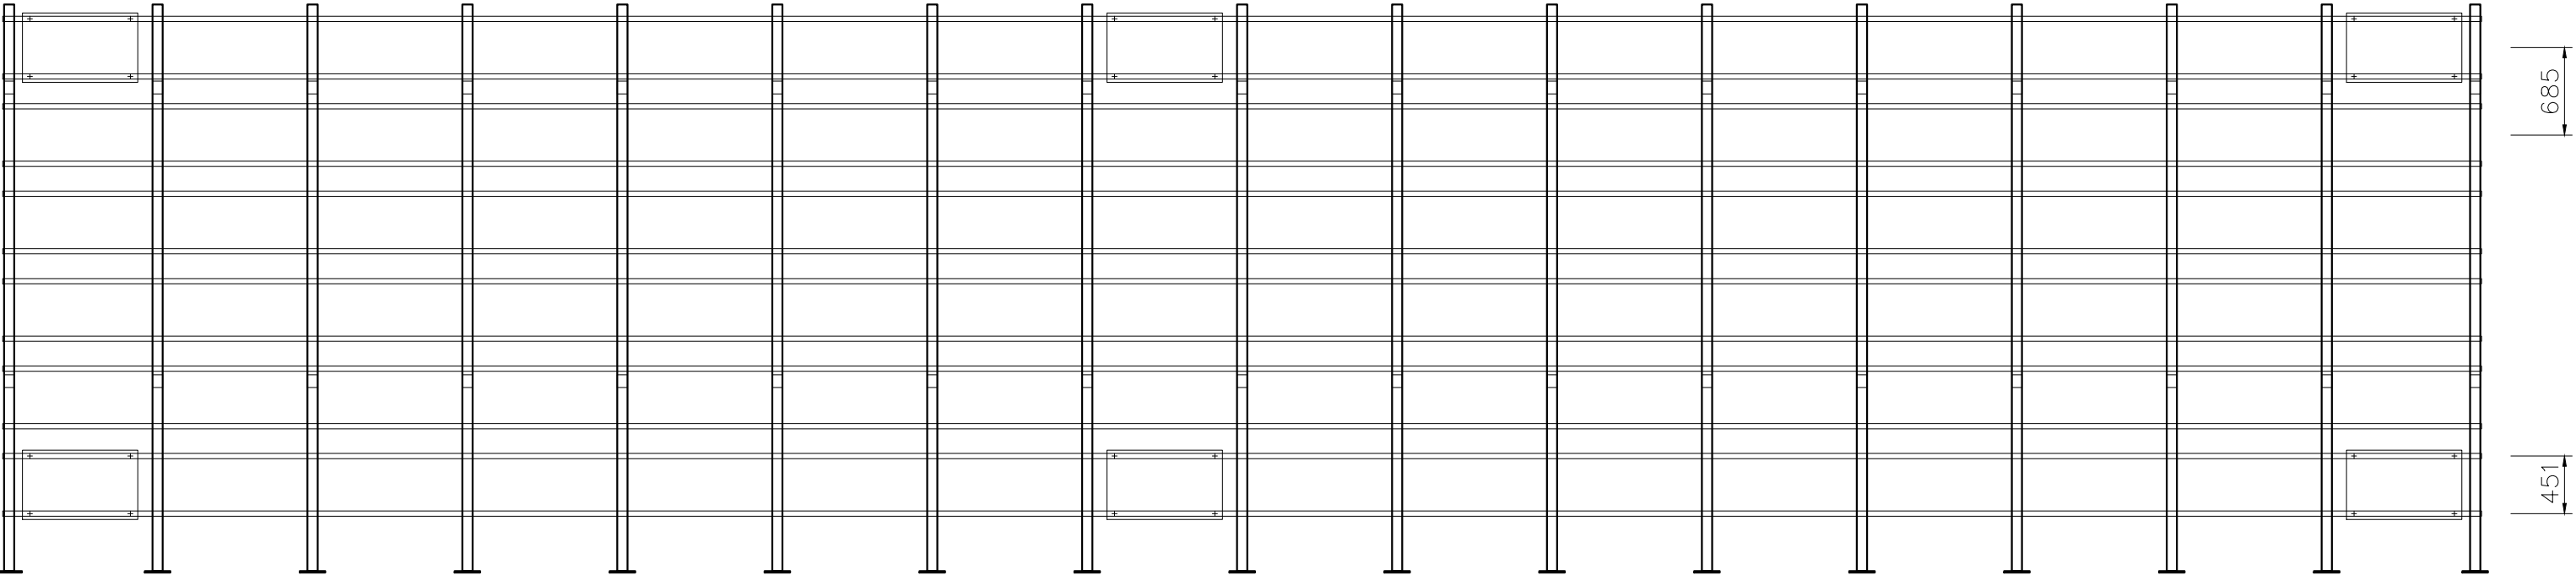

承力路径：

屏体 → 前维护支架

→ 横轨 → 竖向支承

→ 楼地面承接及侧向约束

横轨采用41系列通道参考；

柱预留80×100安装空间。

截面、壁厚、连接与锚固

按设备荷载和主体条件核定。

柱脚200×140×12为空间预留；

本图不作结构承载结论。

支架+ 屏体合计约3187.2kg，

未含自制框架、线缆和辅件。


支承柱17处、横轨12条、墙面约束34处；每台4个固定点示例标十字。安装板相对屏体基准待实测。

横轨每行上下中心距451；柱脚落地，侧向约束在+1.500/+3.800处。详见D12A-02/03。

前维护剖面与作业区 / 屏体保持竖直拉出

平行拉出表示屏体扫掠；支架机构、取屏与作业平台须按实物复核。

A—A 沿屏体法向 / 1: 20

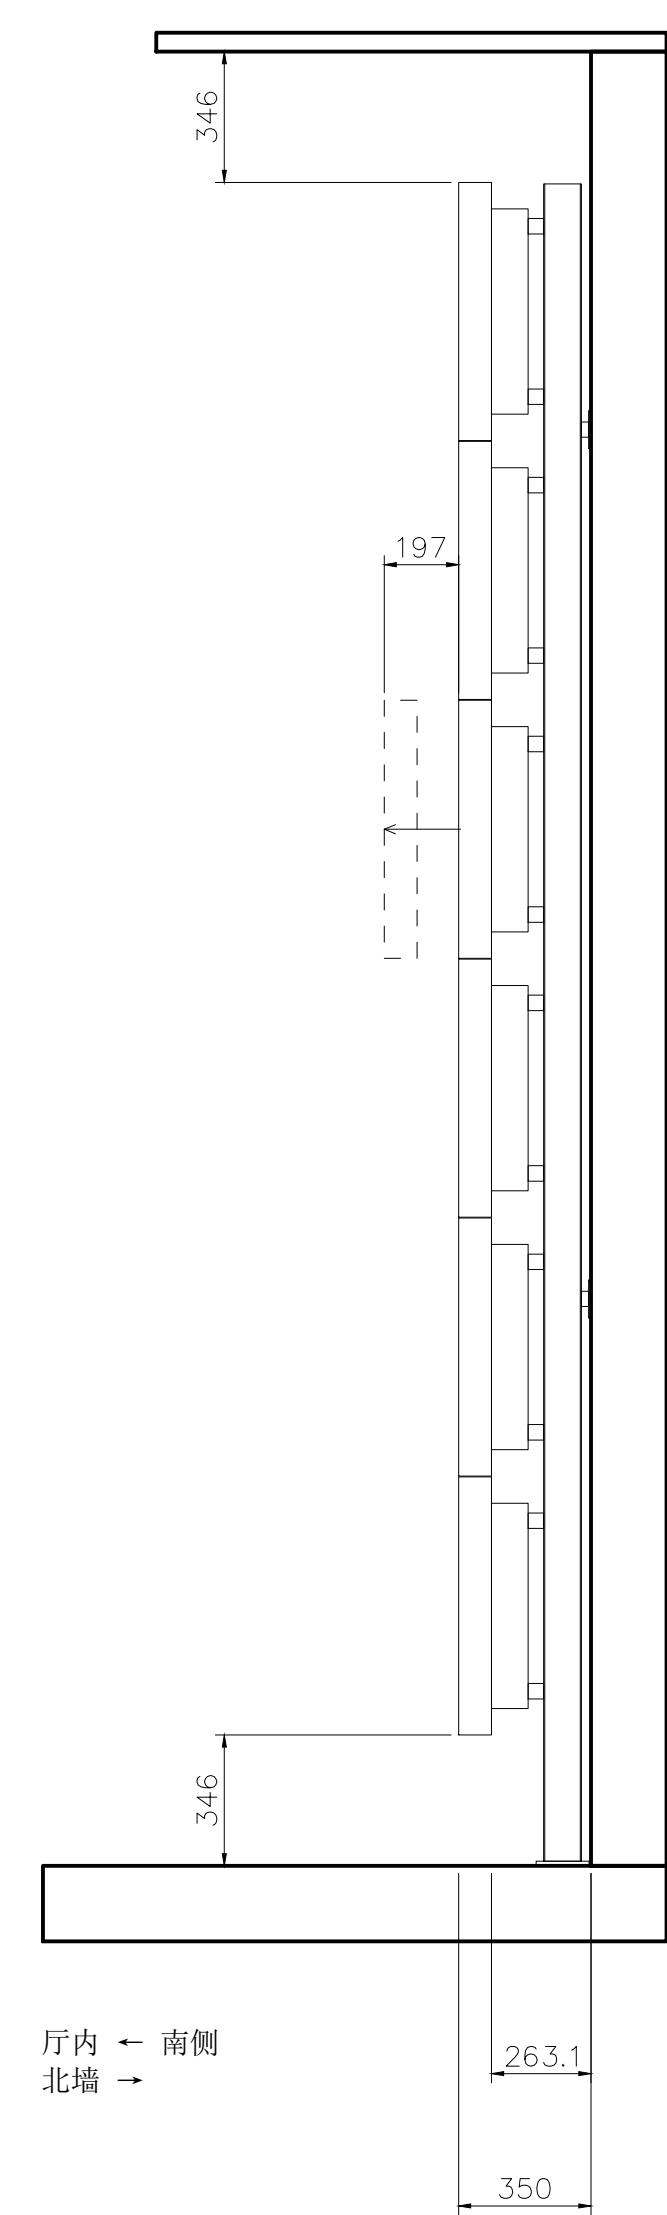

固定安装面：Y=28633.9。

闭合支架厚97；参考展开深294。

推算平行拉出位移197。

闭合屏体前面Y=28450；

展开后前面Y=28253。

背部到建筑墙263.1，为总距离，

其中包含支架及支承层，非净通道。

横轨深41＋柱深100＋后余25.1。

后余内局部设墙面约束，并非连续净空。

不设背面人员通道，采用前维护。

下方和上方保留开放散热带。

进、排风路径不得被封闭饰面截断。

支架与走线避免封堵机身散热口。

96台屏幕典型20.16kW、最大24kW；

该数值不是设计冷负荷或配电选型。


控制器、散热和辅助负荷另计。

前维护释放区与观众区分时使用；

上排使用适配作业平台及搬运辅助。

关闭展示并断电后再维护。

局部平面 / 两列屏前作业位置示意

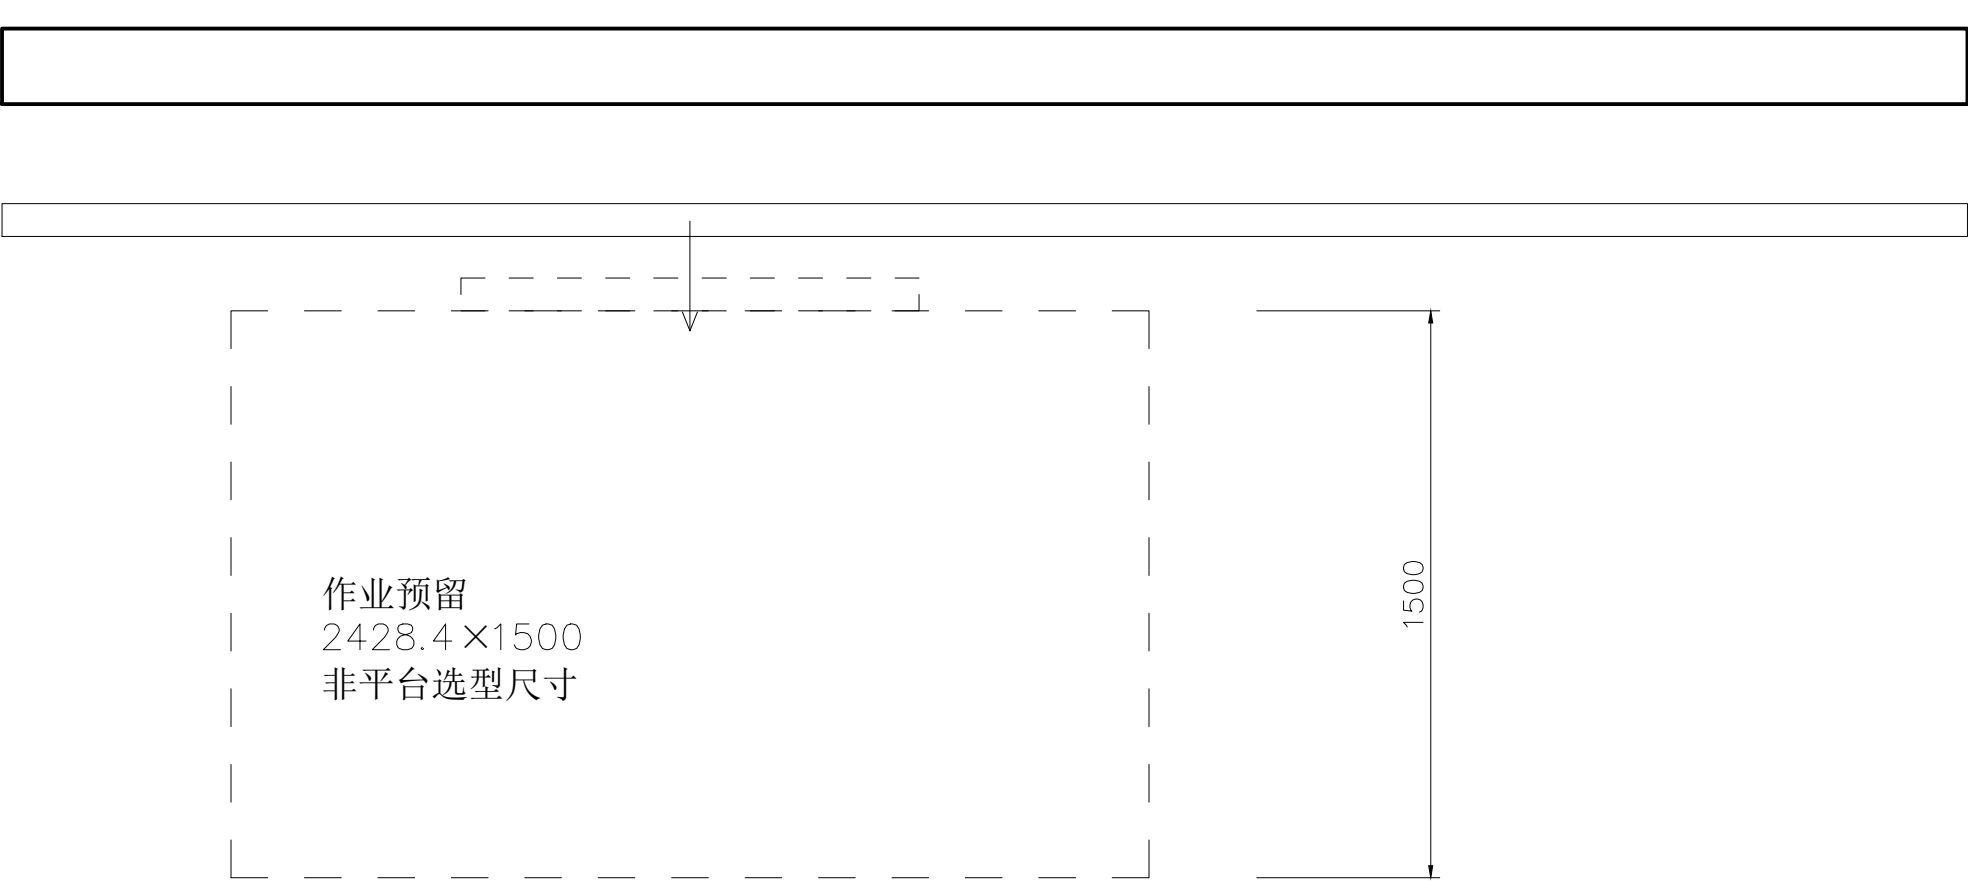

虚线区域按两列宽度、展开屏前1500深预留。须与实际平台、搬运路径和围挡协调。


上排屏中心+4.1125；不得把手直接够到等同于可维护。平台载重、外伸、就位路线待专项核定。

维护顺序：编号定位与断电 → 释放/平移拉出 → 线缆和固定检查 → 依厂家步骤取屏、复位及校准。

2mm 安装缝下的倾斜、上提、取屏与相邻屏避让尚未完成实物试装；本图不宣称全拆装路径已通过。

墙端安装接口与深度链 / 方案协调节点

支架闭合深97。安装孔的墙端基准须与实际型号核对。图内mm。

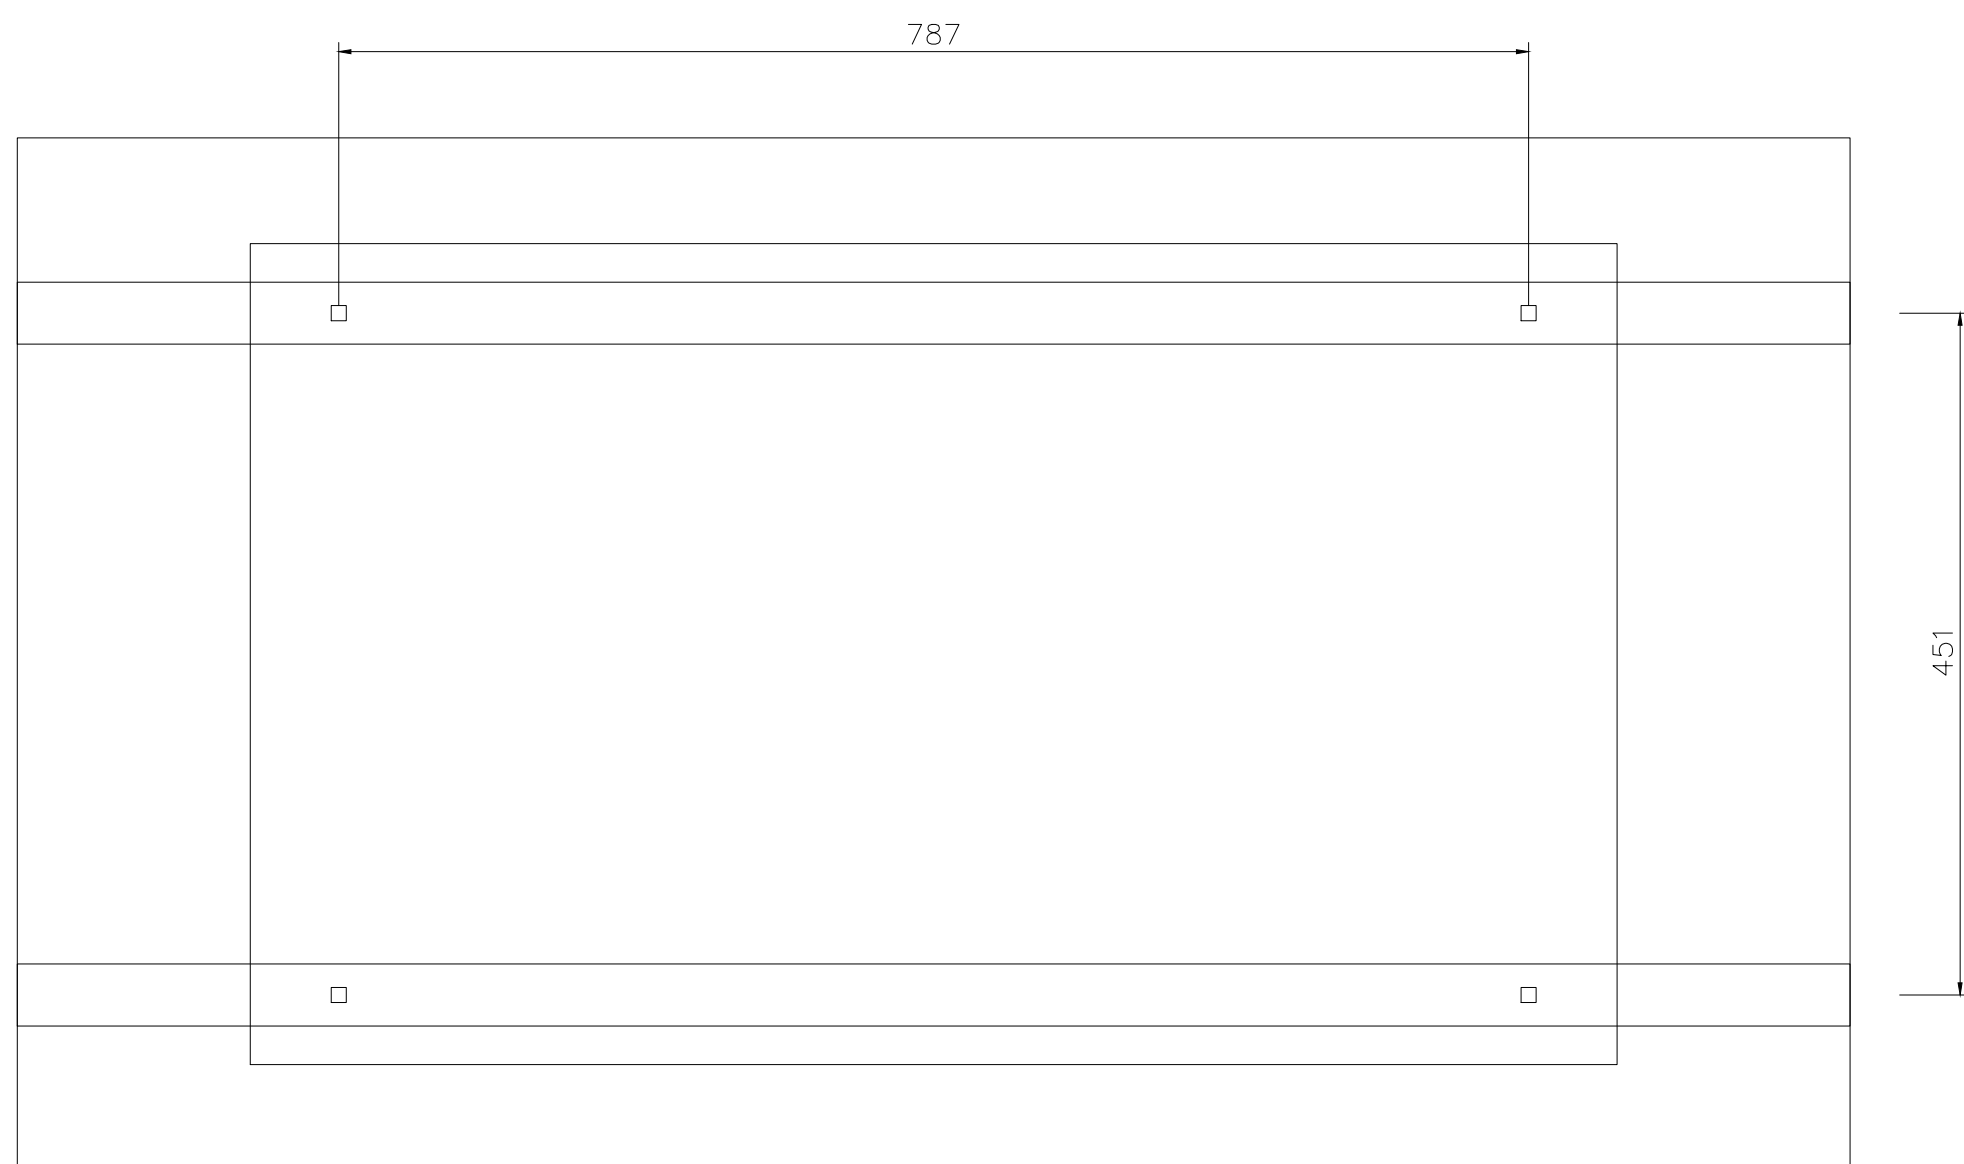

墙端轨道中心451，横向紧固点787。

屏端VESA为600×400；两套孔距不混用。

接口建议：采用匹配通道的螺母、垫片和紧固件；安装板先找平后锁紧。

参考支架配用1/4-20通道螺母；不得直接替换为公制件。


通道图中壁厚2.5、开口/卷边为表达假设，具体P系列截面须按厂家资料。

柱壁预留3；主体、柱脚、墙面约束与锚栓设计待核定。

电源与信号分别整理、留编号和活动余量；线缆弯曲半径取设备要求。

设备尺寸为方案参考，型号与采购参数待核定。

12条横轨、17处支承柱与柱脚、34处墙面约束；线缆待深化。



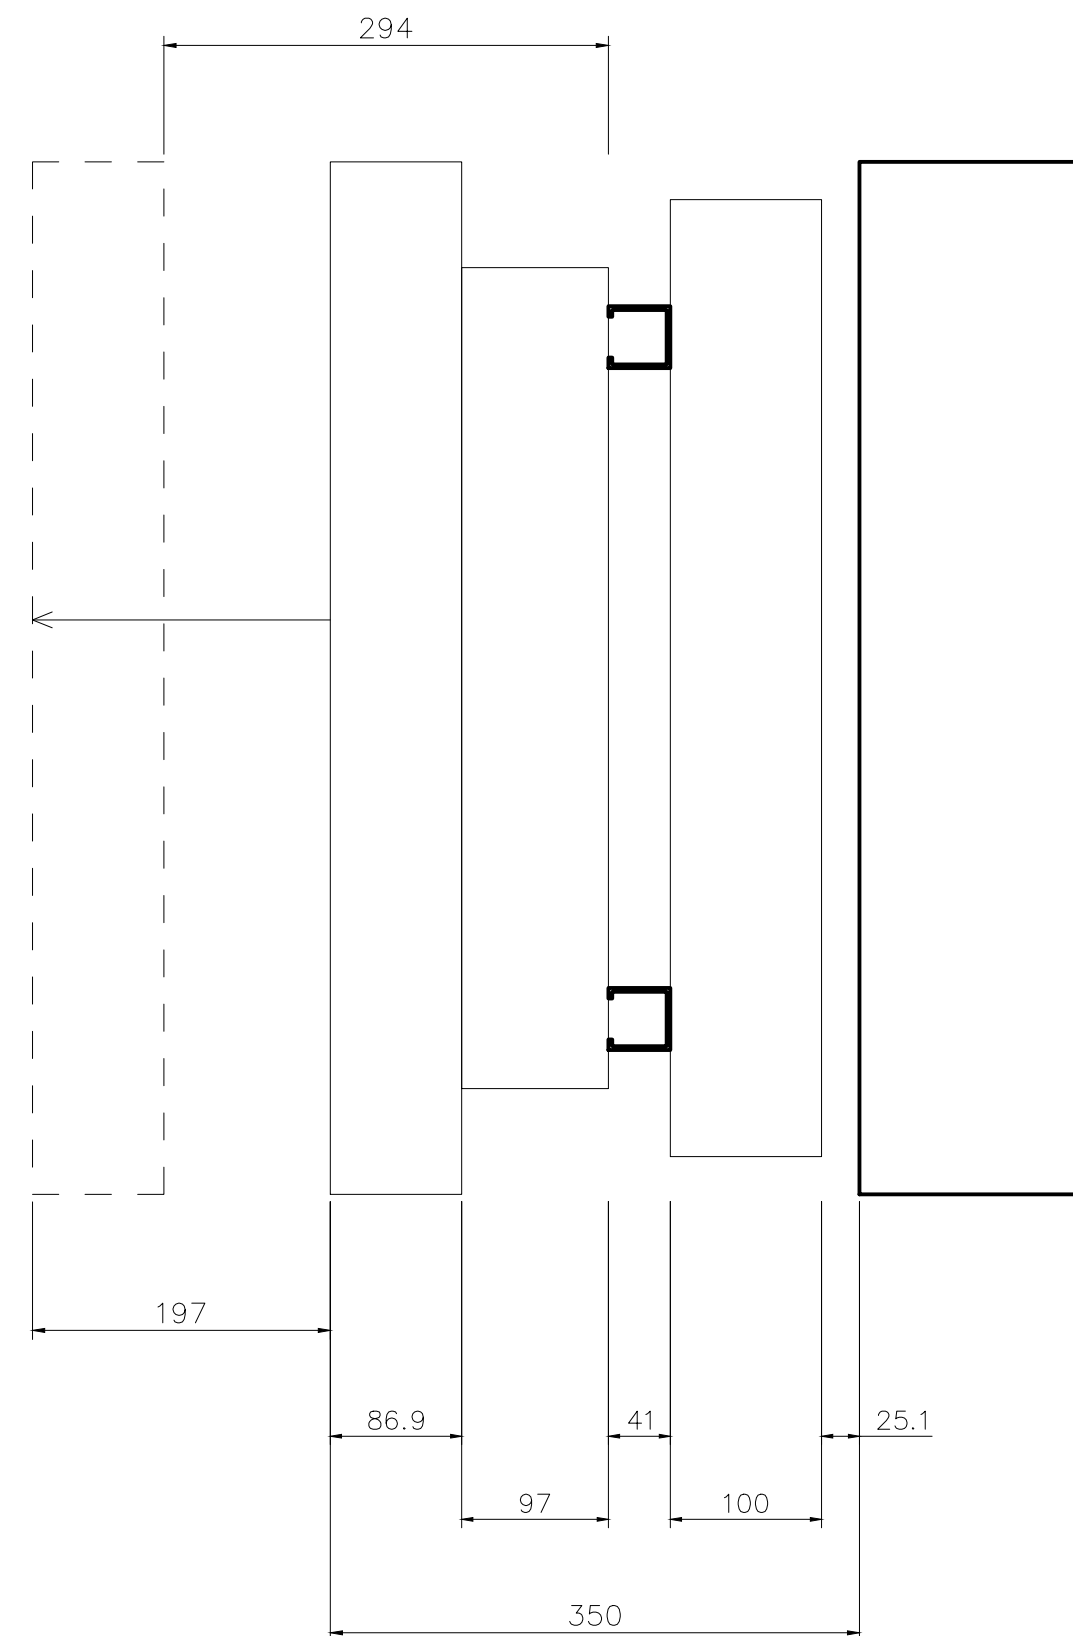


深度链: $86.9 + 97 + 41 + 100 + \text{后余} 25.1 = 350$; 后余内设局部约束。

展开294为厂家侧视尺寸；按闭合97推算位移197。

五柜通用 / C02 构造 • 闭合状态

柜身1500×600×1337，含锁面总深623.15。尺寸单位mm。

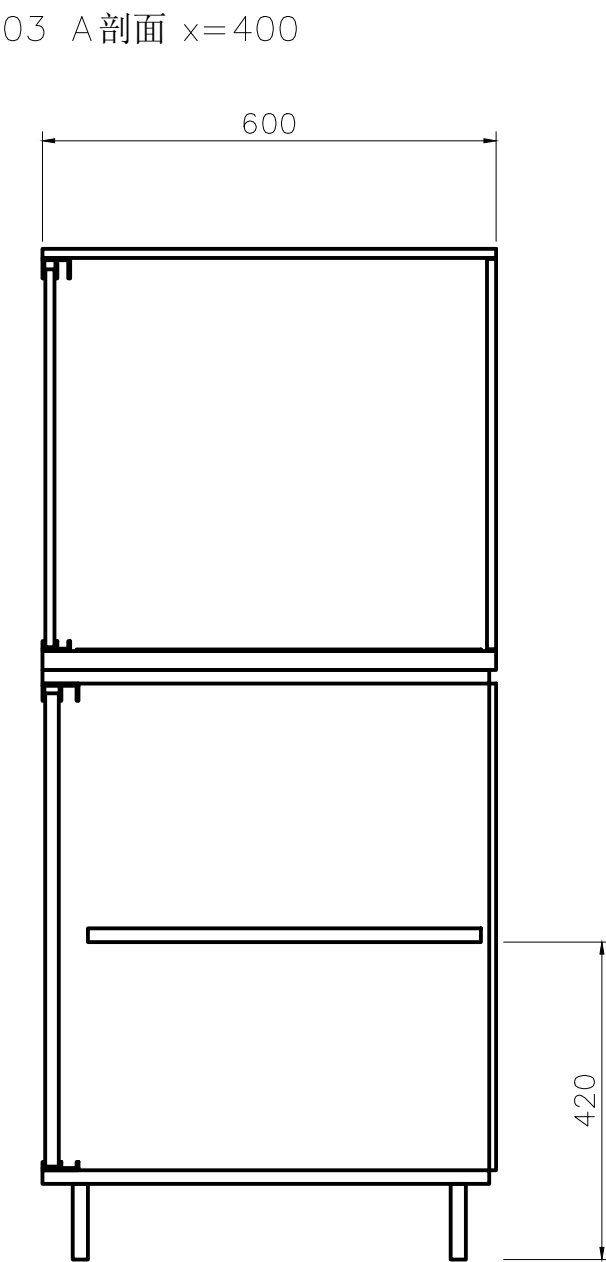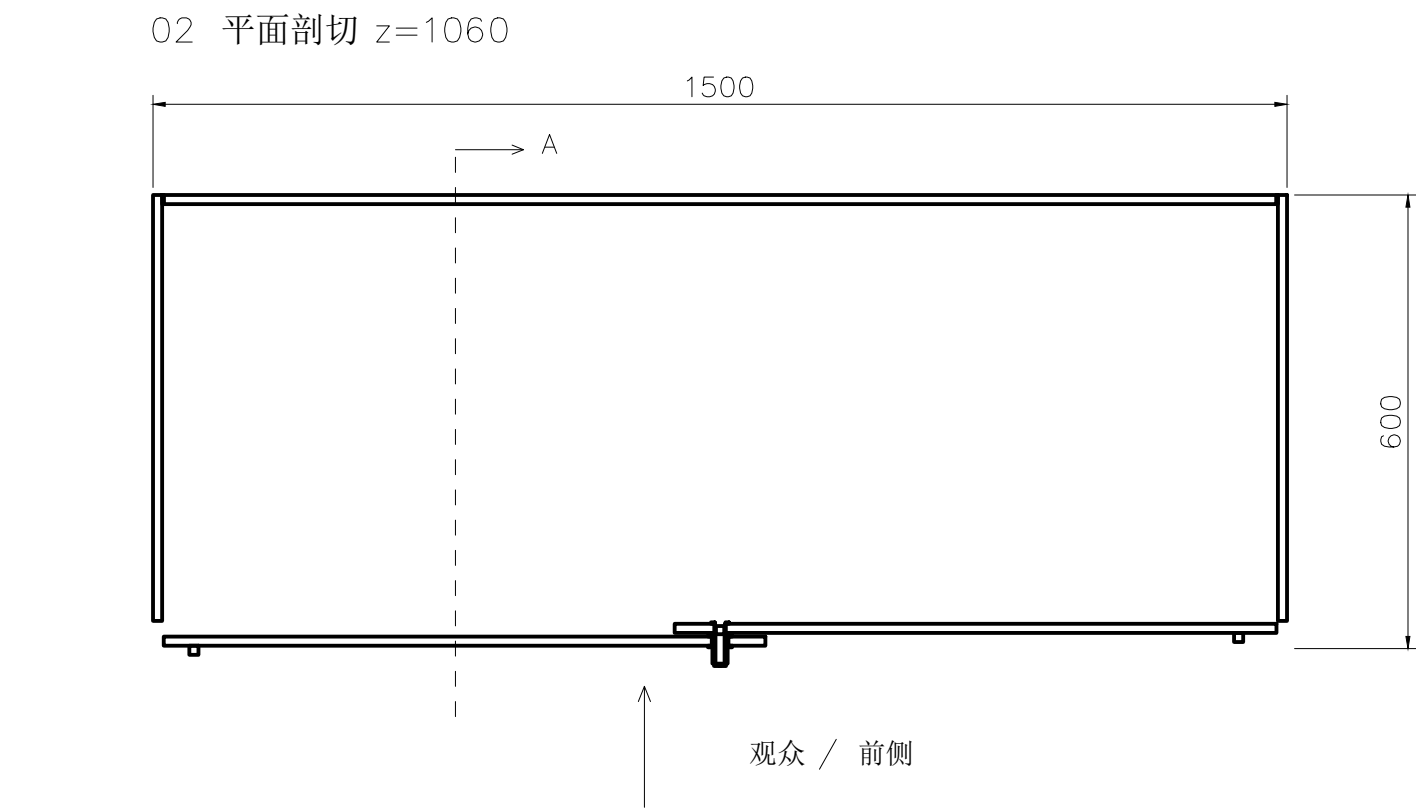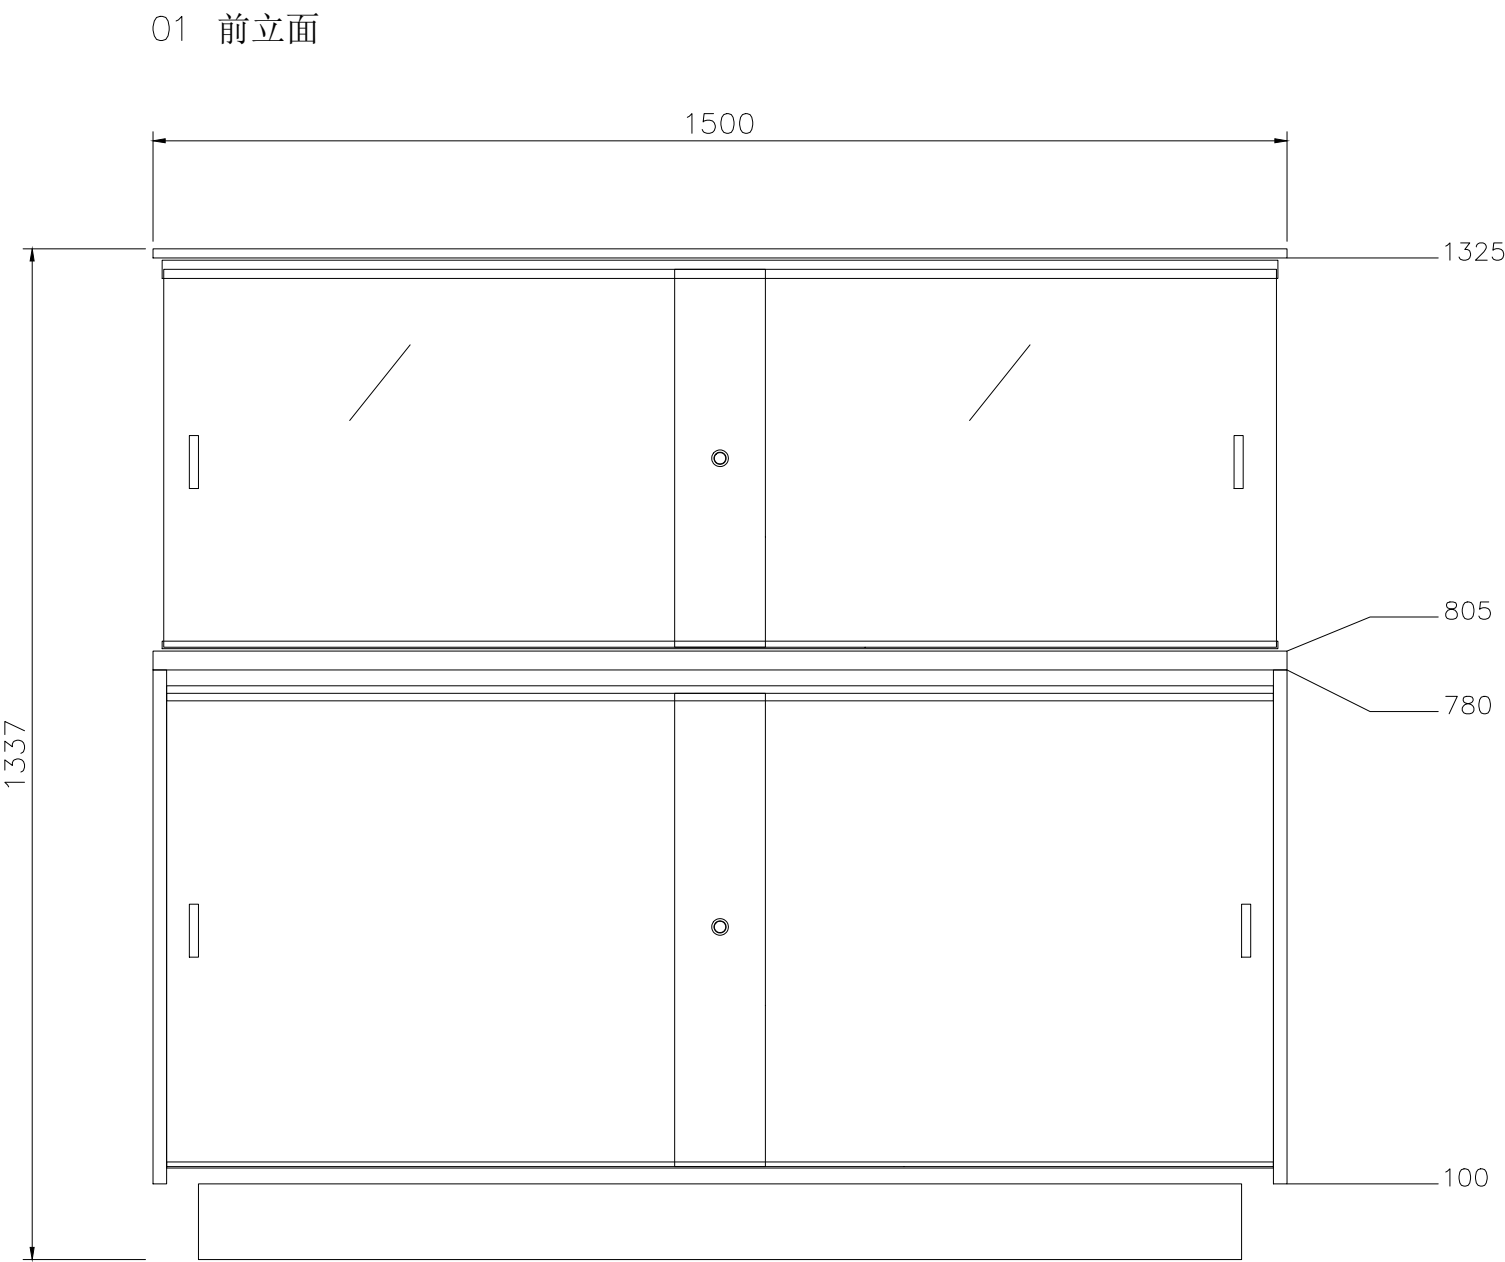

深度方向展开：板件实切。
侧板、背板、层板与轨道均独立。

构造尺寸

柜门闭合与解锁滑动关系见03。
尺寸单位：mm。
图中设计尺寸不是设备采购参数。

构造与使用

- 01 柜身：18侧/顶/底/隔板，9背板。
- 02 两块18活动层板，标高420；
八块承托木块提供可读支承关系。
- 03 25承托板+2展示衬面。
- 04 固定玻璃：侧、后、顶12；
底垫2、顶垫1、后角缝2。
- 05 上部两扇12玻璃门；下部两扇
18木门。前后轨道分开。
- 06 上门行程594、下门592；仅操作
一扇，关闭后再操作另一扇。
- 07 加入可退锁销、压圈与接收套；
先解锁再滑门，产品仍待选型。
- 08 板厚/玻璃/轨道为方案尺寸；
孔位为几何预留，强度与五金待定。
- 09 五柜内部教学陈设；
本页为结构图，陈设见05/06。


详图索引

D12B-02：轨道断面、垫条与防抬。
D12B-03：开启、维护和主要板件表。
D12B-04：锁位、固定孔与五柜位置。
D12B-05/06：五柜内部陈设。
D12B-07/08：托盘取放与柜内灯体。

轨道、垫条与防抬构造 / 1:2


轨道为方案断面；实际系统需核对承载、滑动、玻璃加工及固定孔位。

J1 玻璃门上轨与防抬

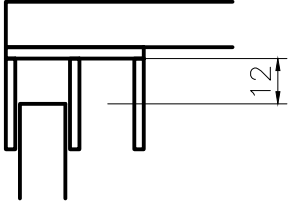


顶玻璃12；上轨顶壁3。
玻璃门顶至轨顶净距12。
可拆挡块8高，底标高1313，
与门顶留3间隙。
拆挡块后上提10，轨顶仍余2。

J2 玻璃门下轨与承托板

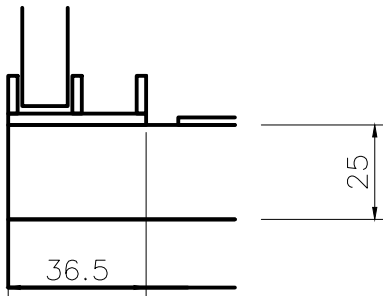


25展示承托板，上设轨道。
下轨底壁3；轨壁顶标高818。
门底810，上提10后为820，
高于轨壁2。
衬面仅铺内部，避开滑轨。

J3 木滑门上轨与防抬

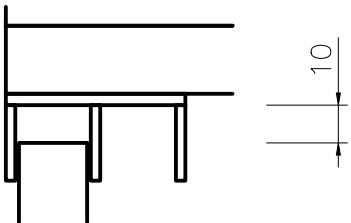

木门18，双通道净宽20。
门顶749，轨顶下皮759。
拆6高挡块后上提8，
门顶757，仍余2。
轨顶固定于柜顶板下。

J4 木滑门下轨与柜底板

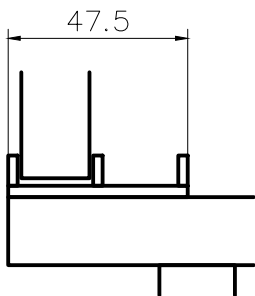

18柜底板，上铺3轨底。
门底123、轨壁顶129。
上提8后门底131，脱轨余2。
轨壁厚2.5；侧向间隙1。
拉手轮廓未穿入另一门行程。

连接与维护条件

轨道两端以柜侧/罩侧承接；螺钉、端盖及锁具系统仍需产品定型。固定玻璃底垫2、顶垫1，后角缝封条2。
解锁后拆除锁具附件及防抬挡块，按前扇、后扇次序取出；上提及倾斜路径仍须样柜验证。
滑动门不是气密文保展柜；本图未完成玻璃强度、密封性能或连接承载验收。

开启、维护与板件 / EX01 典型柜

一次仅移动一扇；图示解锁后，上部前扇向右594、下部向右592；后扇向左同等行程。

04 前扇开启状态
594



木门有效侧向开口592；玻璃门开口596。
限位与拉手位置配合，禁止两扇相向同时移动。



05 维护关系

图示500深仅为站位研究；
完整托盘取出范围见第07页。
玻璃拆卸需两人、适配吸盘及
实际操作空间复核；不作人数
或无障碍净宽结论。

日常取放和维护安排在前侧。
柜右侧至现有墙面450。

主要板件与玻璃 / mm

部件	数量	尺寸/说明
侧板	2	18×600×680
底板分片 / 检修盖	见清单 / 4	18厚分片；盖58×58×18
柜顶	1	1464×591×18
背板	1	1464×9×644
中隔板	1	18×541×644
活动层板	2	723×520×18
层板承托块	8	18×30×18
展示承托板	1	1500×600×25
展示衬面	1	1460×535×2
木滑门	2	792×18×626
侧玻璃	2	12×563.5×517
后玻璃	1	1472×12×517
顶玻璃	1	1500×600×12
玻璃滑门	2	796×12×500
上罩双轨	各1	1476长 / 深36.5
下柜双轨	各1	1464长 / 深47.5
拉手 / 限位 / 挡块	各4	尺寸见对应节点

尺寸按X×Y×Z列示，含垫条与轨壁。
材料种类和五金定型后，
按实物复核加工尺寸。

维护顺序


- 1 闭馆清空台内展品，解锁并确认限位。
- 2 拆锁具附件及防抬挡块，再处理前扇。
- 3 前扇移出后再处理后扇；不得强行跨轨。
- 4 清洁滑轨、检查垫条，复装挡块及锁具。

锁具与固定孔已作空间协调；实际系统和玻璃加工未定型。

锁位、固定孔与五柜投放 / 1:1 局部实尺度

锁具为几何协调方案，圆孔不是玻璃加工单；实际产品、边距及强化处理需厂家确认。

J5 上部玻璃滑门锁 / X=750

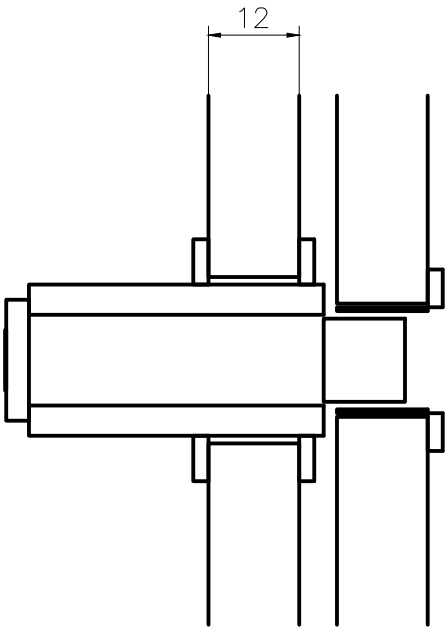

前扇Ø22 / 后扇Ø15。

锁销Ø11，接收套内Ø13。


解锁先向前退出12。

退销后与后扇前面留3。

前后玻璃重叠120。

单扇行程594，侧开口596。

J6 下部木滑门锁 / X=750

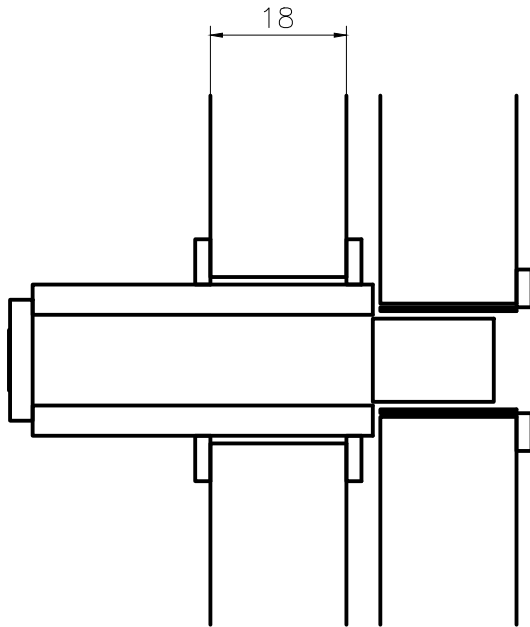

前扇Ø22 / 后扇Ø15。

锁销Ø11，接收套内Ø13。

解锁先向前退出17。


退销后与后扇前面留2。

前后木门重叠120。

单扇行程592，侧开口592。

锁销退回后方可滑门；内部锁芯按实际产品配置，防盗性能须另行核定。

J7 左前固定板平面 / 剖切Z=14

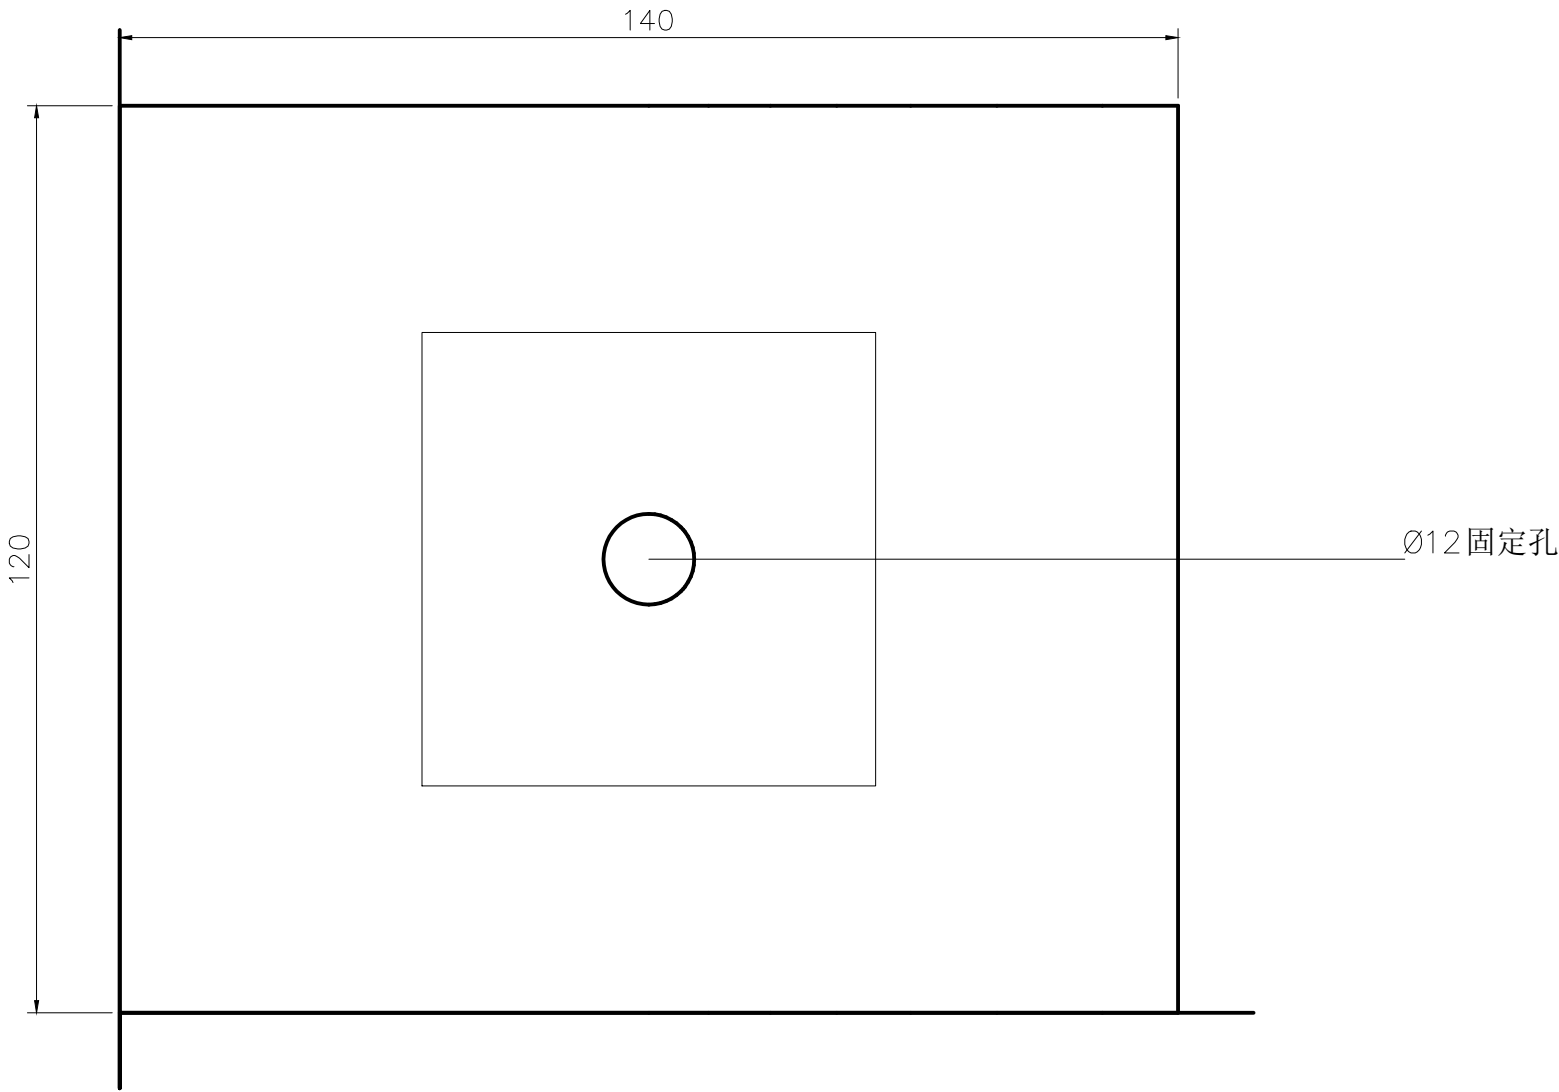

上方60×60检修孔配58×58盖；四角共4处。
锚栓、地面钻孔和抗倾覆验算依据实际基层另定。

五柜局部原点与朝向 / 坐标m

编号	X	Y	正面
EX01	7.950	8.200	南
EX07	2.000	19.000	南
EX08	2.000	22.000	南
EX10	6.000	26.000	南
EX12	28.500	24.550	西



局部原点为柜身X/Y零点，不含前突锁面。
EX12 旋转－90°，宽度方向指向南；其余不旋转。
陈设见第05/06页；独立图文架位置见第09页。

五柜内部陈设 / EX01 • EX07 • EX08

本页1:10、柜体局部坐标mm；展示件为教学示意。

EX01 莞香材料

正面 / 玻璃轮廓为参照

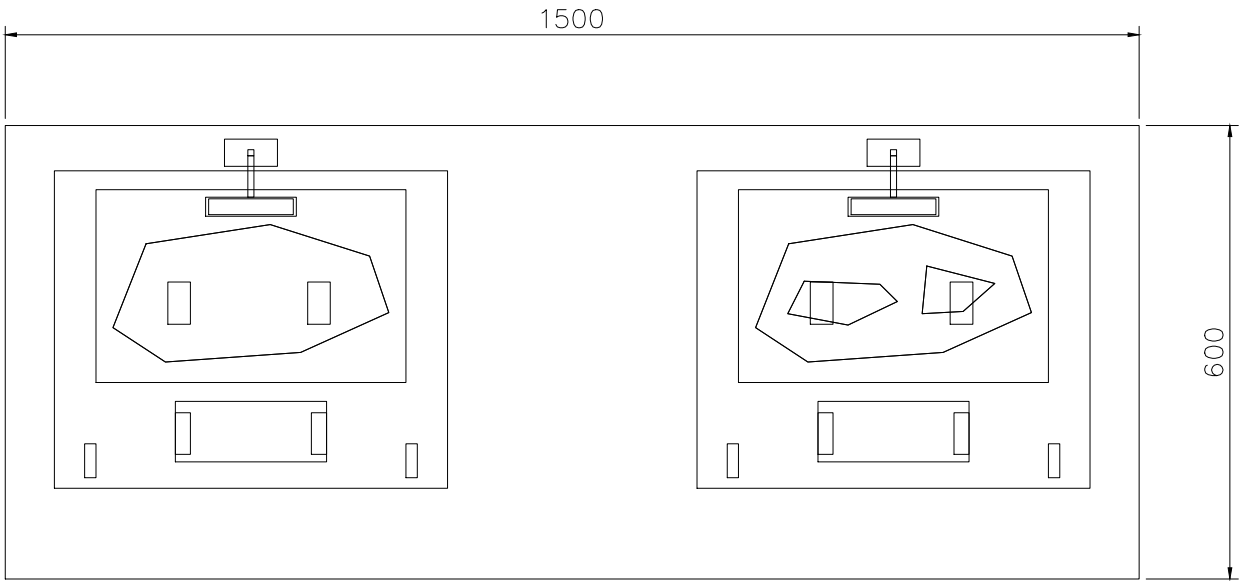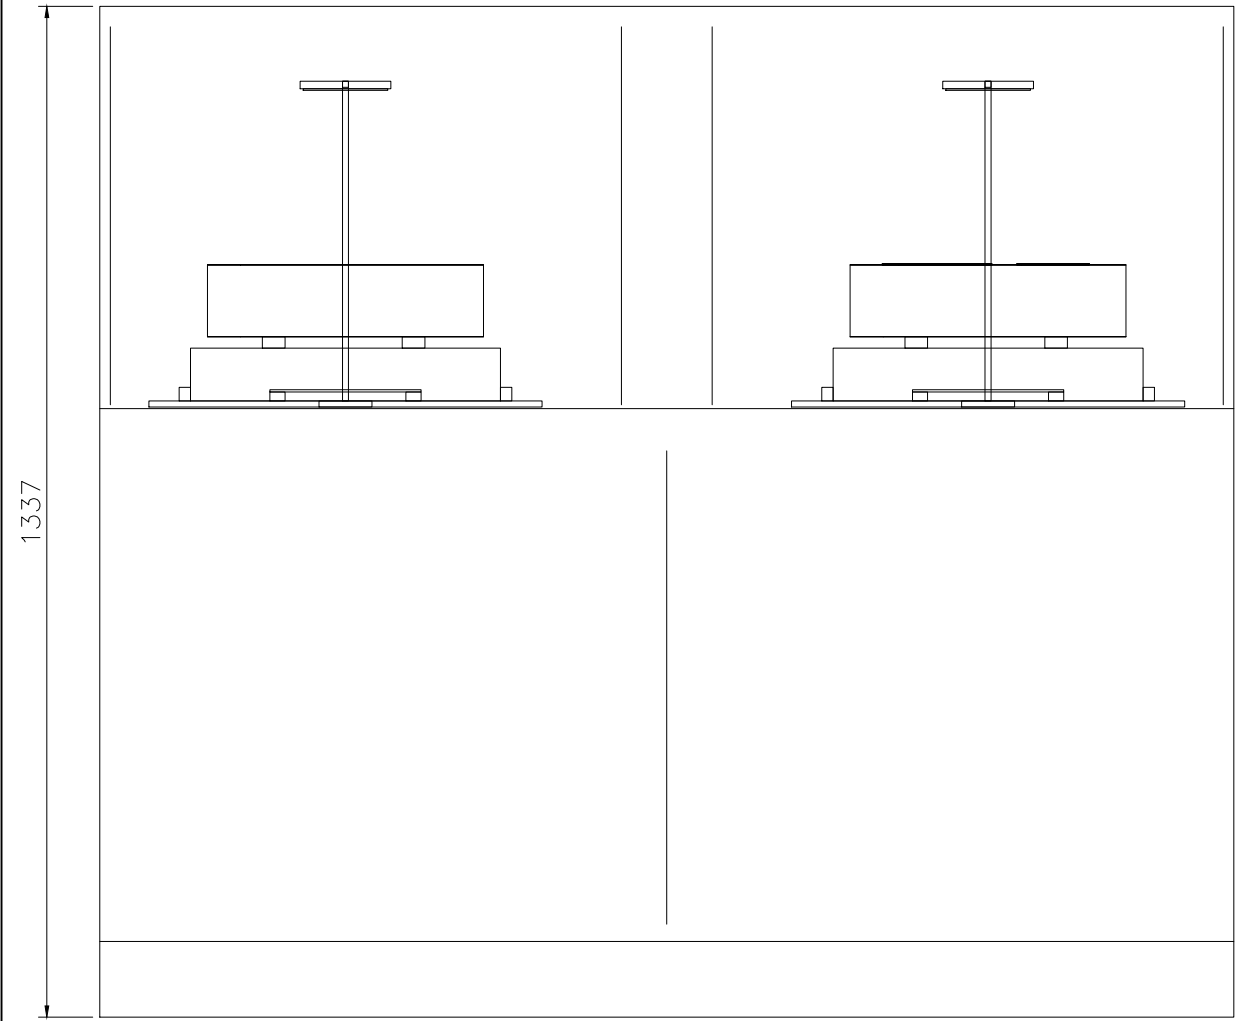

上视 / 顶玻璃隐藏：正面为图下方

陈设与支承



左右各一件材料示意，右件加入局部深色区域。
示意件底标高900，面顶995；衬垫与底座承托。
两托盘520×420；前缘各设200×80可换展签。
不表示已取得样本、固定树脂含量或鉴定结论。

柜内两灯：X=325 / 1175；发光面底1226。
灯具独立后立杆，后座与托盘留开；局部见08。
电源接口、穿线及实际光学产品仍待深化。

柜内展签200×80，图文见展陈分册。
柜侧独立图文架与柜体位置关系见第09页。

EX07 白木香形态

正面 / 玻璃轮廓为参照

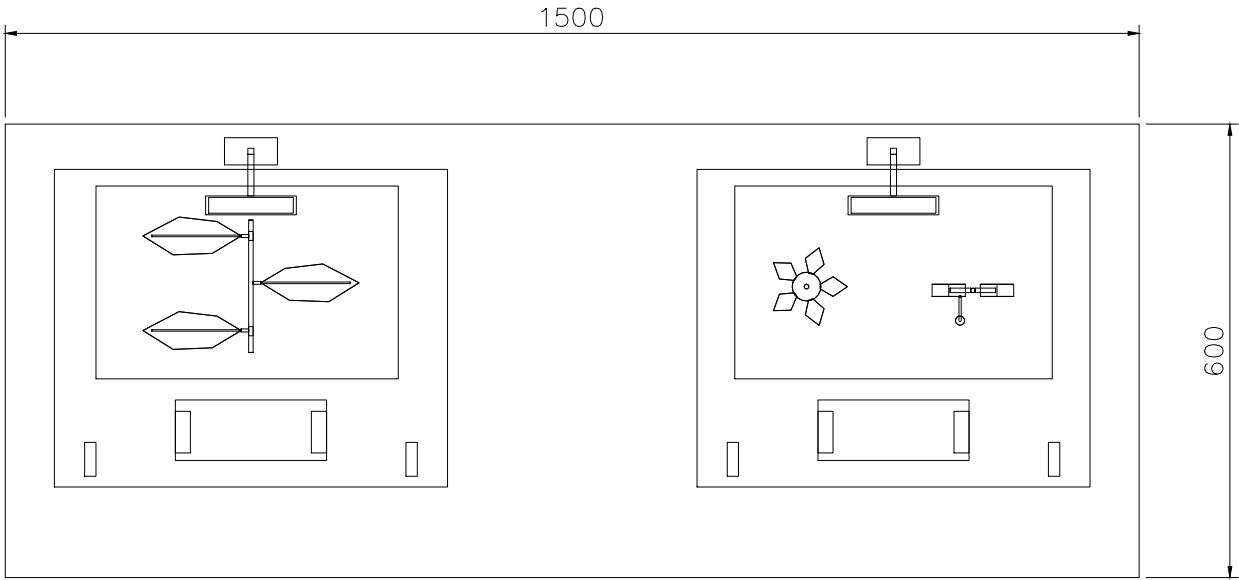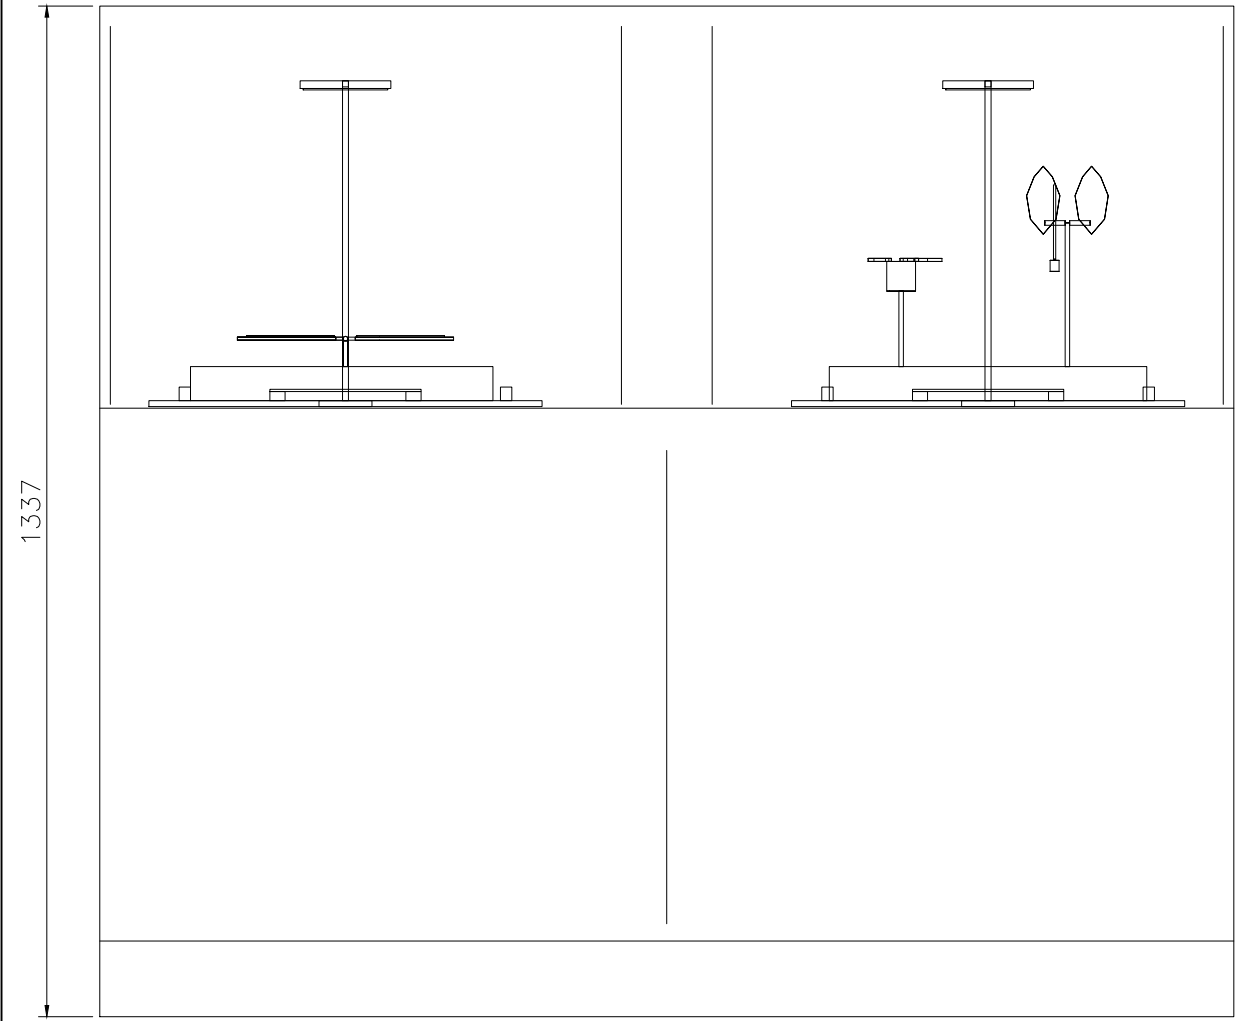

上视 / 顶玻璃隐藏：正面为图下方

陈设与支承



左侧：原创互生叶枝，两托杆支承。
右侧：简化花部、两瓣裂果与悬种关系模型。
植物器官为独立放大比例，非一套等比标本。
真实标本身份、保管和光照条件未落实。

柜内两灯：X=325 / 1175；发光面底1226。
灯具独立后立杆，后座与托盘留开；局部见08。
电源接口、穿线及实际光学产品仍待深化。

柜内展签200×80，图文见展陈分册。
柜侧独立图文架与柜体位置关系见第09页。

EX08 结香局部

正面 / 玻璃轮廓为参照

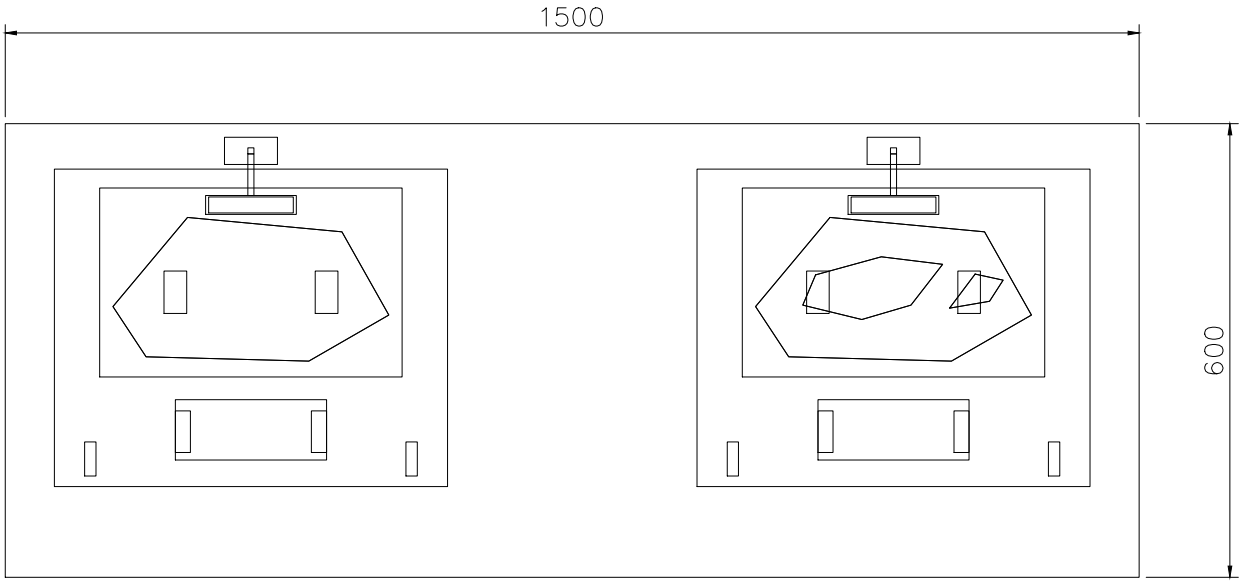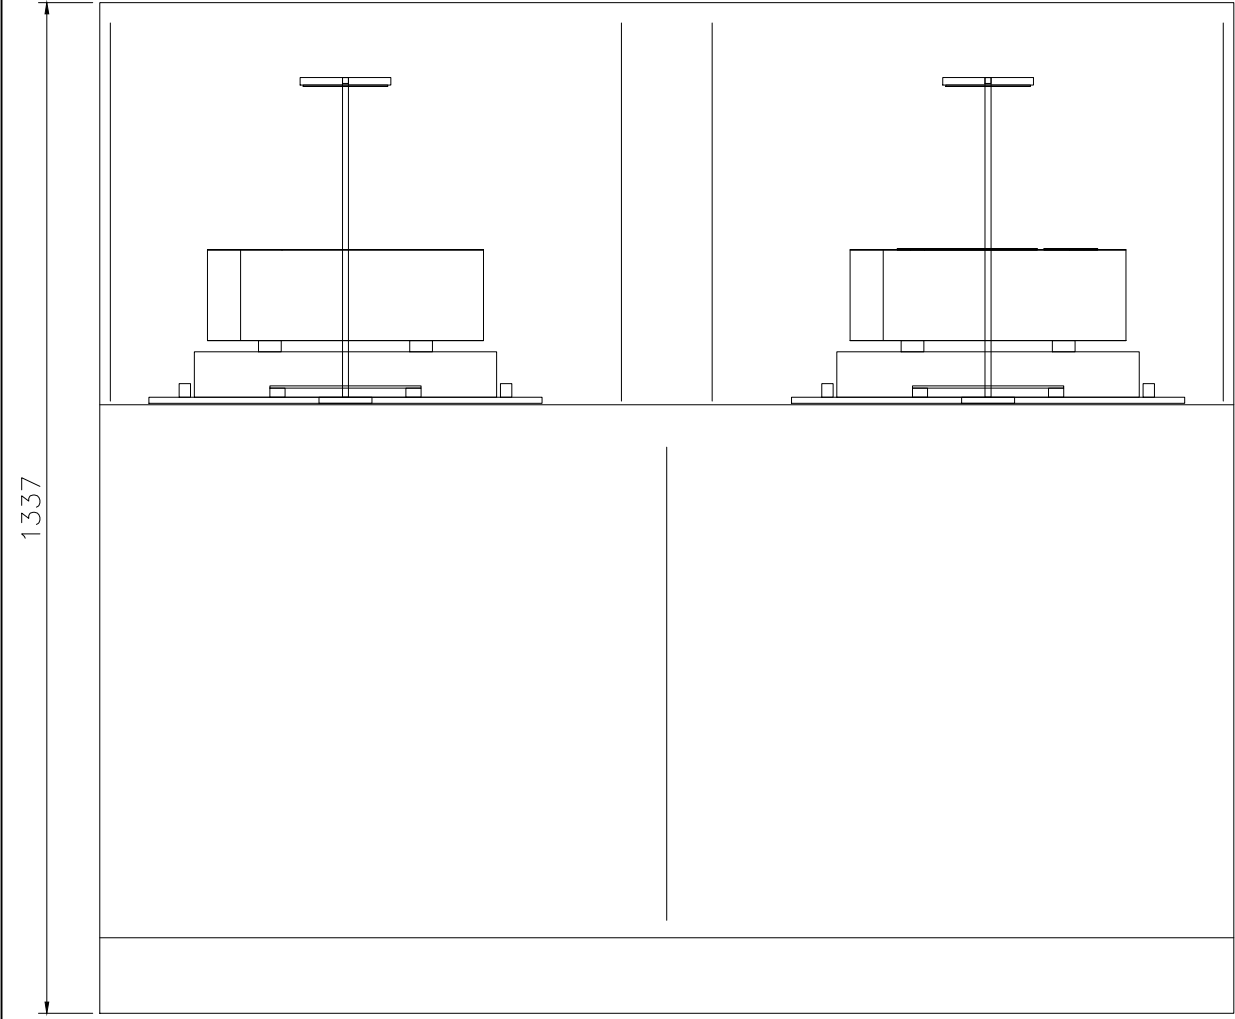

上视 / 顶玻璃隐藏：正面为图下方

陈设与支承

左右材料局部作关系比较；右件深色区域为示意。
材料底标高890，主体面顶1010。
没有用年轮、倒计时或固定比例表示结香规律。
结香机制图见柜侧独立图文架。

柜内两灯：X=325 / 1175；发光面底1226。
灯具独立后立杆，后座与托盘留开；局部见08。
电源接口、穿线及实际光学产品仍待深化。



柜内展签200×80，图文见展陈分册。
柜侧独立图文架与柜体位置关系见第09页。

五柜内部陈设 / EX10 • EX12与共同灯位

本页采用柜体局部坐标：EX12现场正面朝西，其余柜正面朝南。

EX10 香材形态

正面 / 玻璃轮廓为参照

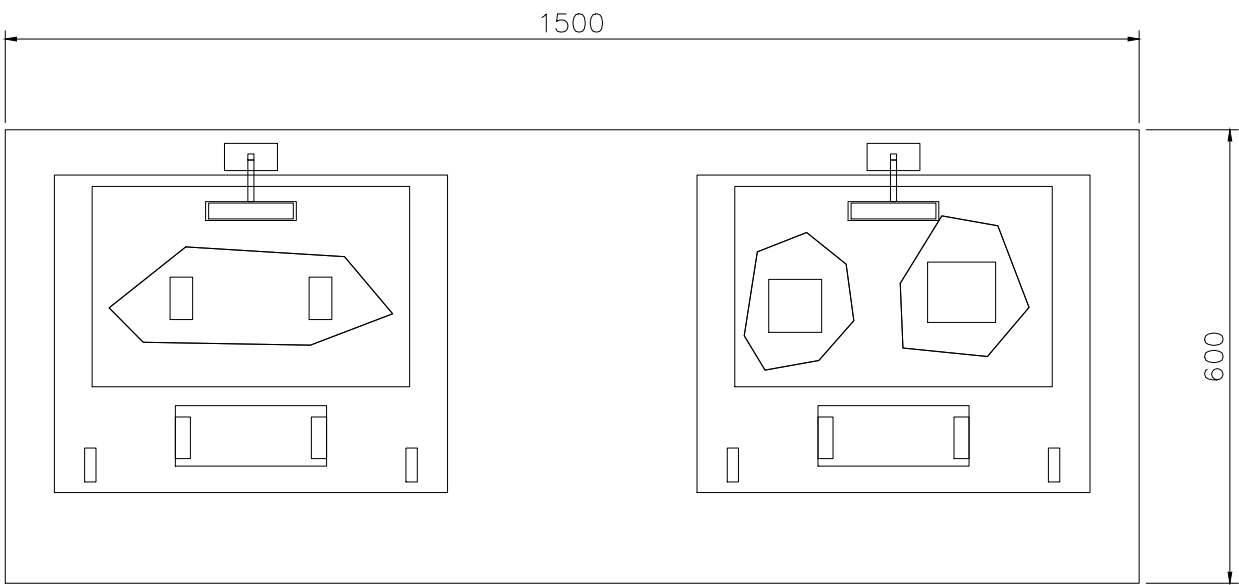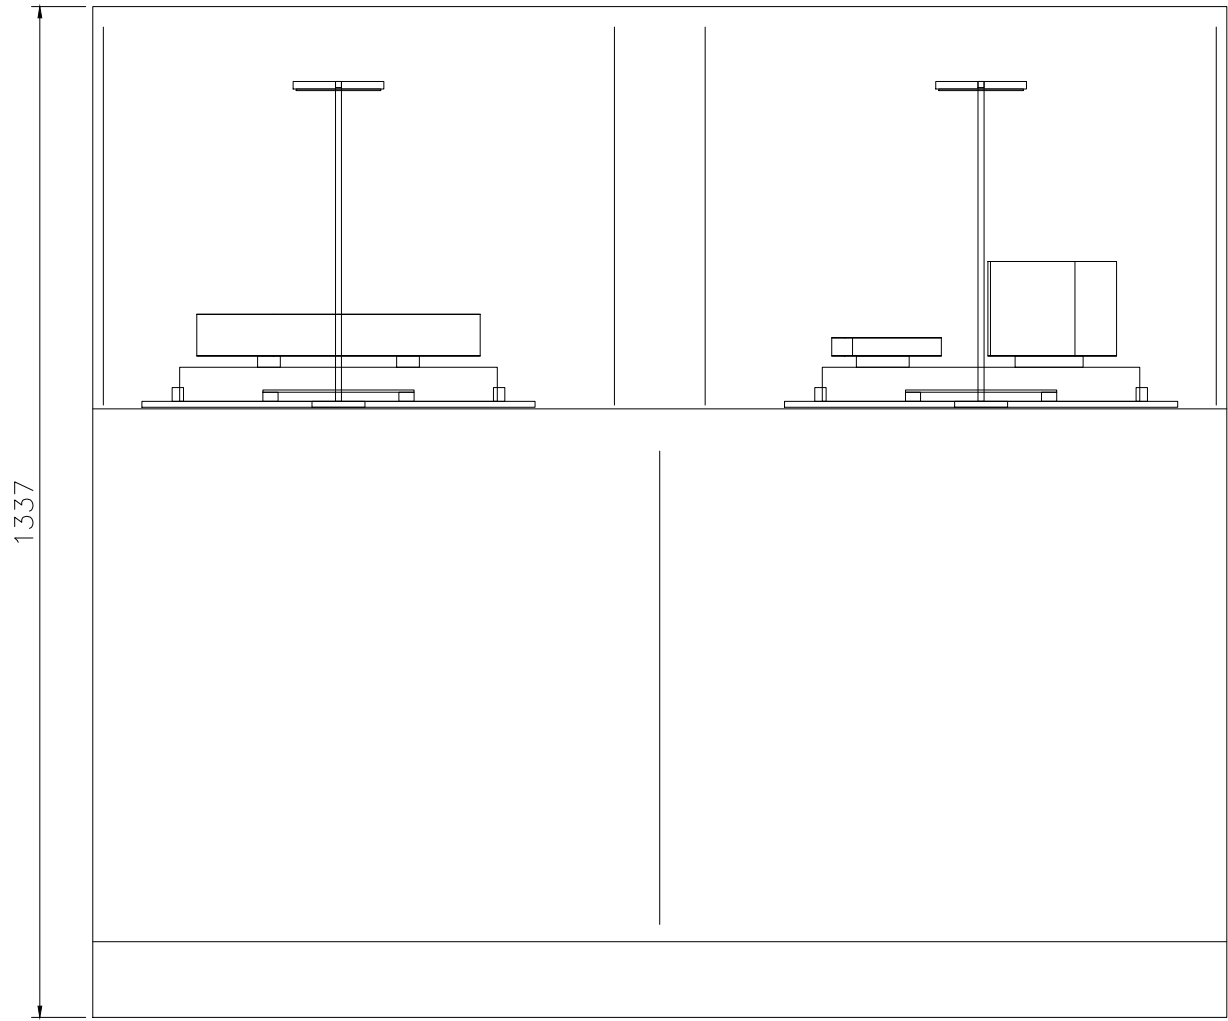

上视 / 顶玻璃隐藏：正面为图下方

陈设与支承



一件长形、一件薄片和一件厚块分别托放。
长形顶930；薄片顶899；厚块顶1000。
模型只表达形态变化，不作为品质或产地判断。
左托盘连续移出关系见第07页。

柜内两灯：X=325 / 1175；发光面底1226。
灯具独立后立杆，后座与托盘留开；局部见08。
电源接口、穿线及实际光学产品仍待深化。

柜内展签200×80，图文见展陈分册。
柜侧独立图文架与柜体位置关系见第09页。

EX12 理香工具

正面 / 玻璃轮廓为参照

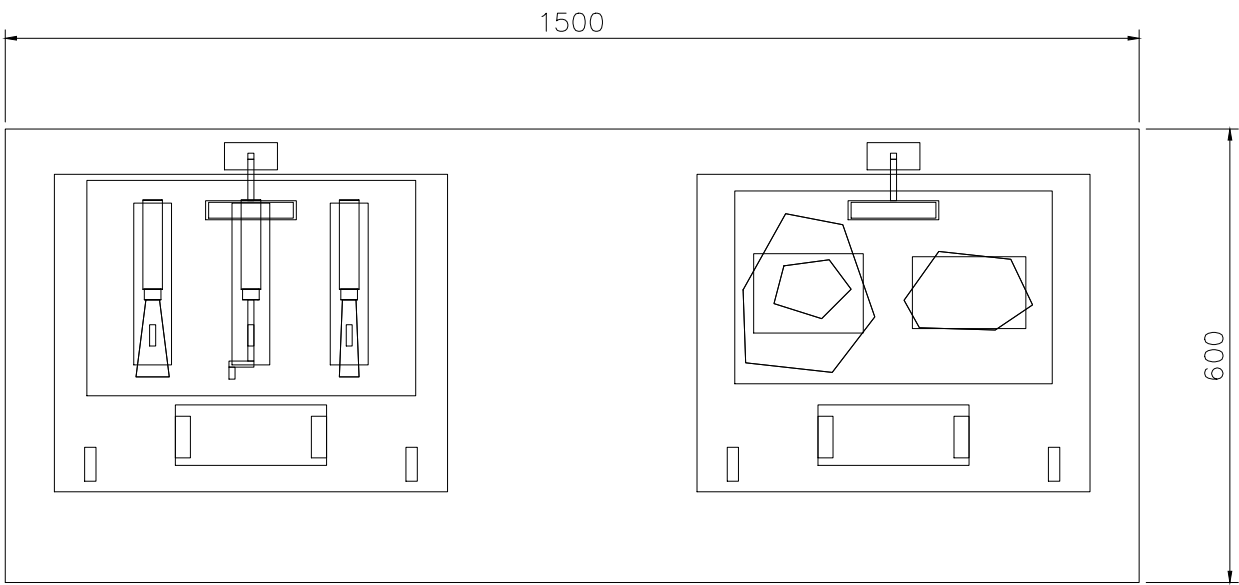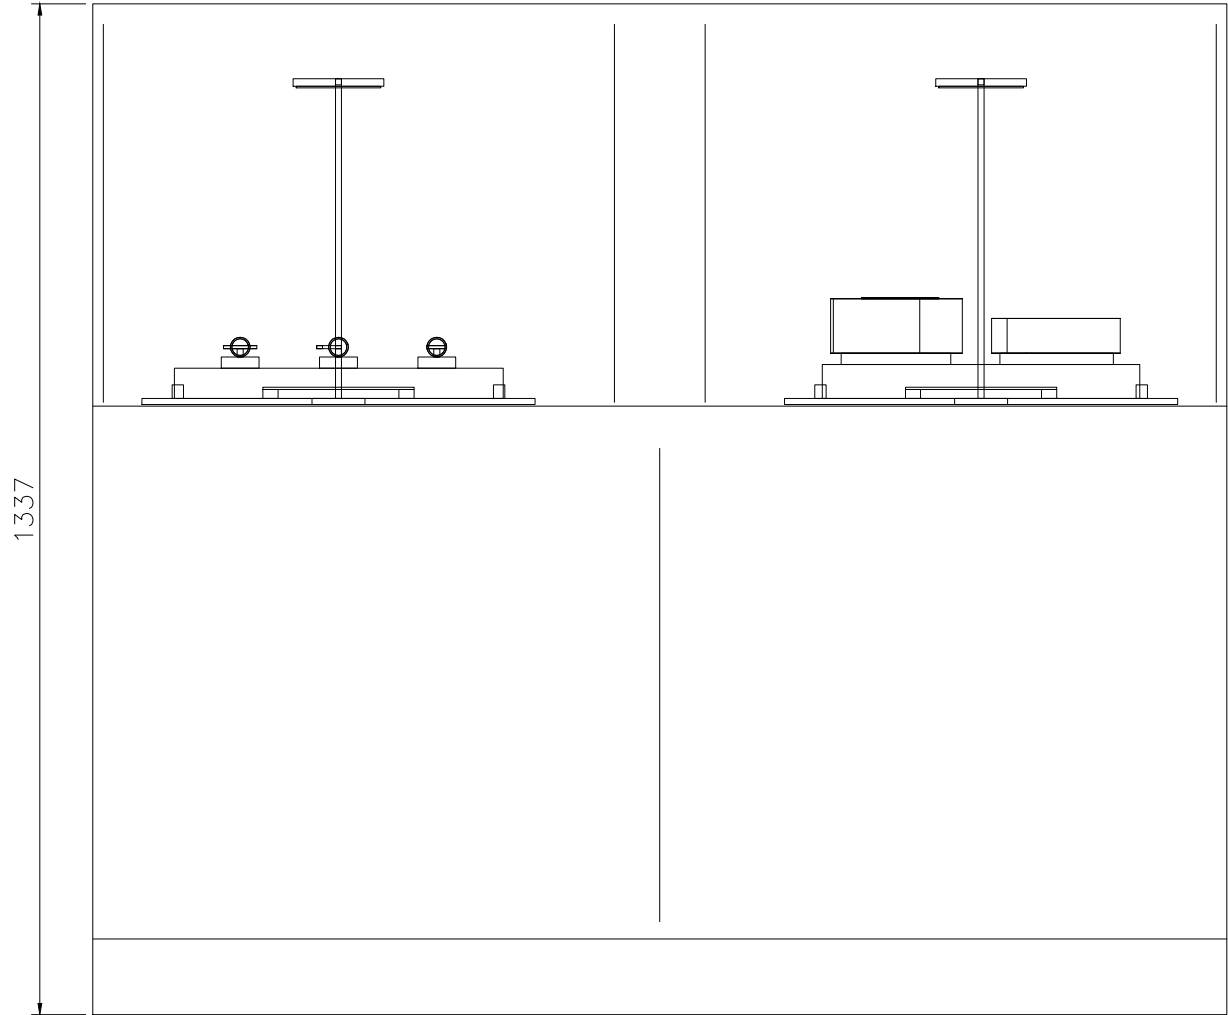

上视 / 顶玻璃隐藏：正面为图下方

陈设与支承

左侧：铲刀、勾丝刀、凿子的钝化展示轮廓。
右侧：去木前后材料去留关系，均为教学示意。
刀身另设承托，木柄与刀身高度已协调。
实际柜正面朝西；本页统一采用柜体局部正面。

柜内两灯：X=325 / 1175；发光面底1226。
灯具独立后立杆，后座与托盘留开；局部见08。
电源接口、穿线及实际光学产品仍待深化。

柜内展签200×80，图文见展陈分册。
柜侧立图文架与柜体位置关系见第09页。

五柜共同控制尺寸

柜身1500×600×1337；展示衬面顶807。
托盘X=65/915，Y=120，底807，顶815。
每组520×420×8；前签面200×80、顶830。


灯座70×36×8，Y=546—582；托盘后缘540。
立杆8×8；灯头120×25×10，发光面112×21。
安装尺寸为方案预留，产品及电气参数须另行核定。

五柜采用相同基础构造，内部陈设按主题区分；外设独立图文架。
照度、光谱、温升、供电和反射眩光须结合产品与真实样本条件核定。

托盘取放与剖面 / EX10左托盘

对应门完全解锁并开到限位；工作人员托持托盘移出，图中省略双手/移动工作台。不是悬挑结构。

01 连续取放平面 / 柜体局部坐标

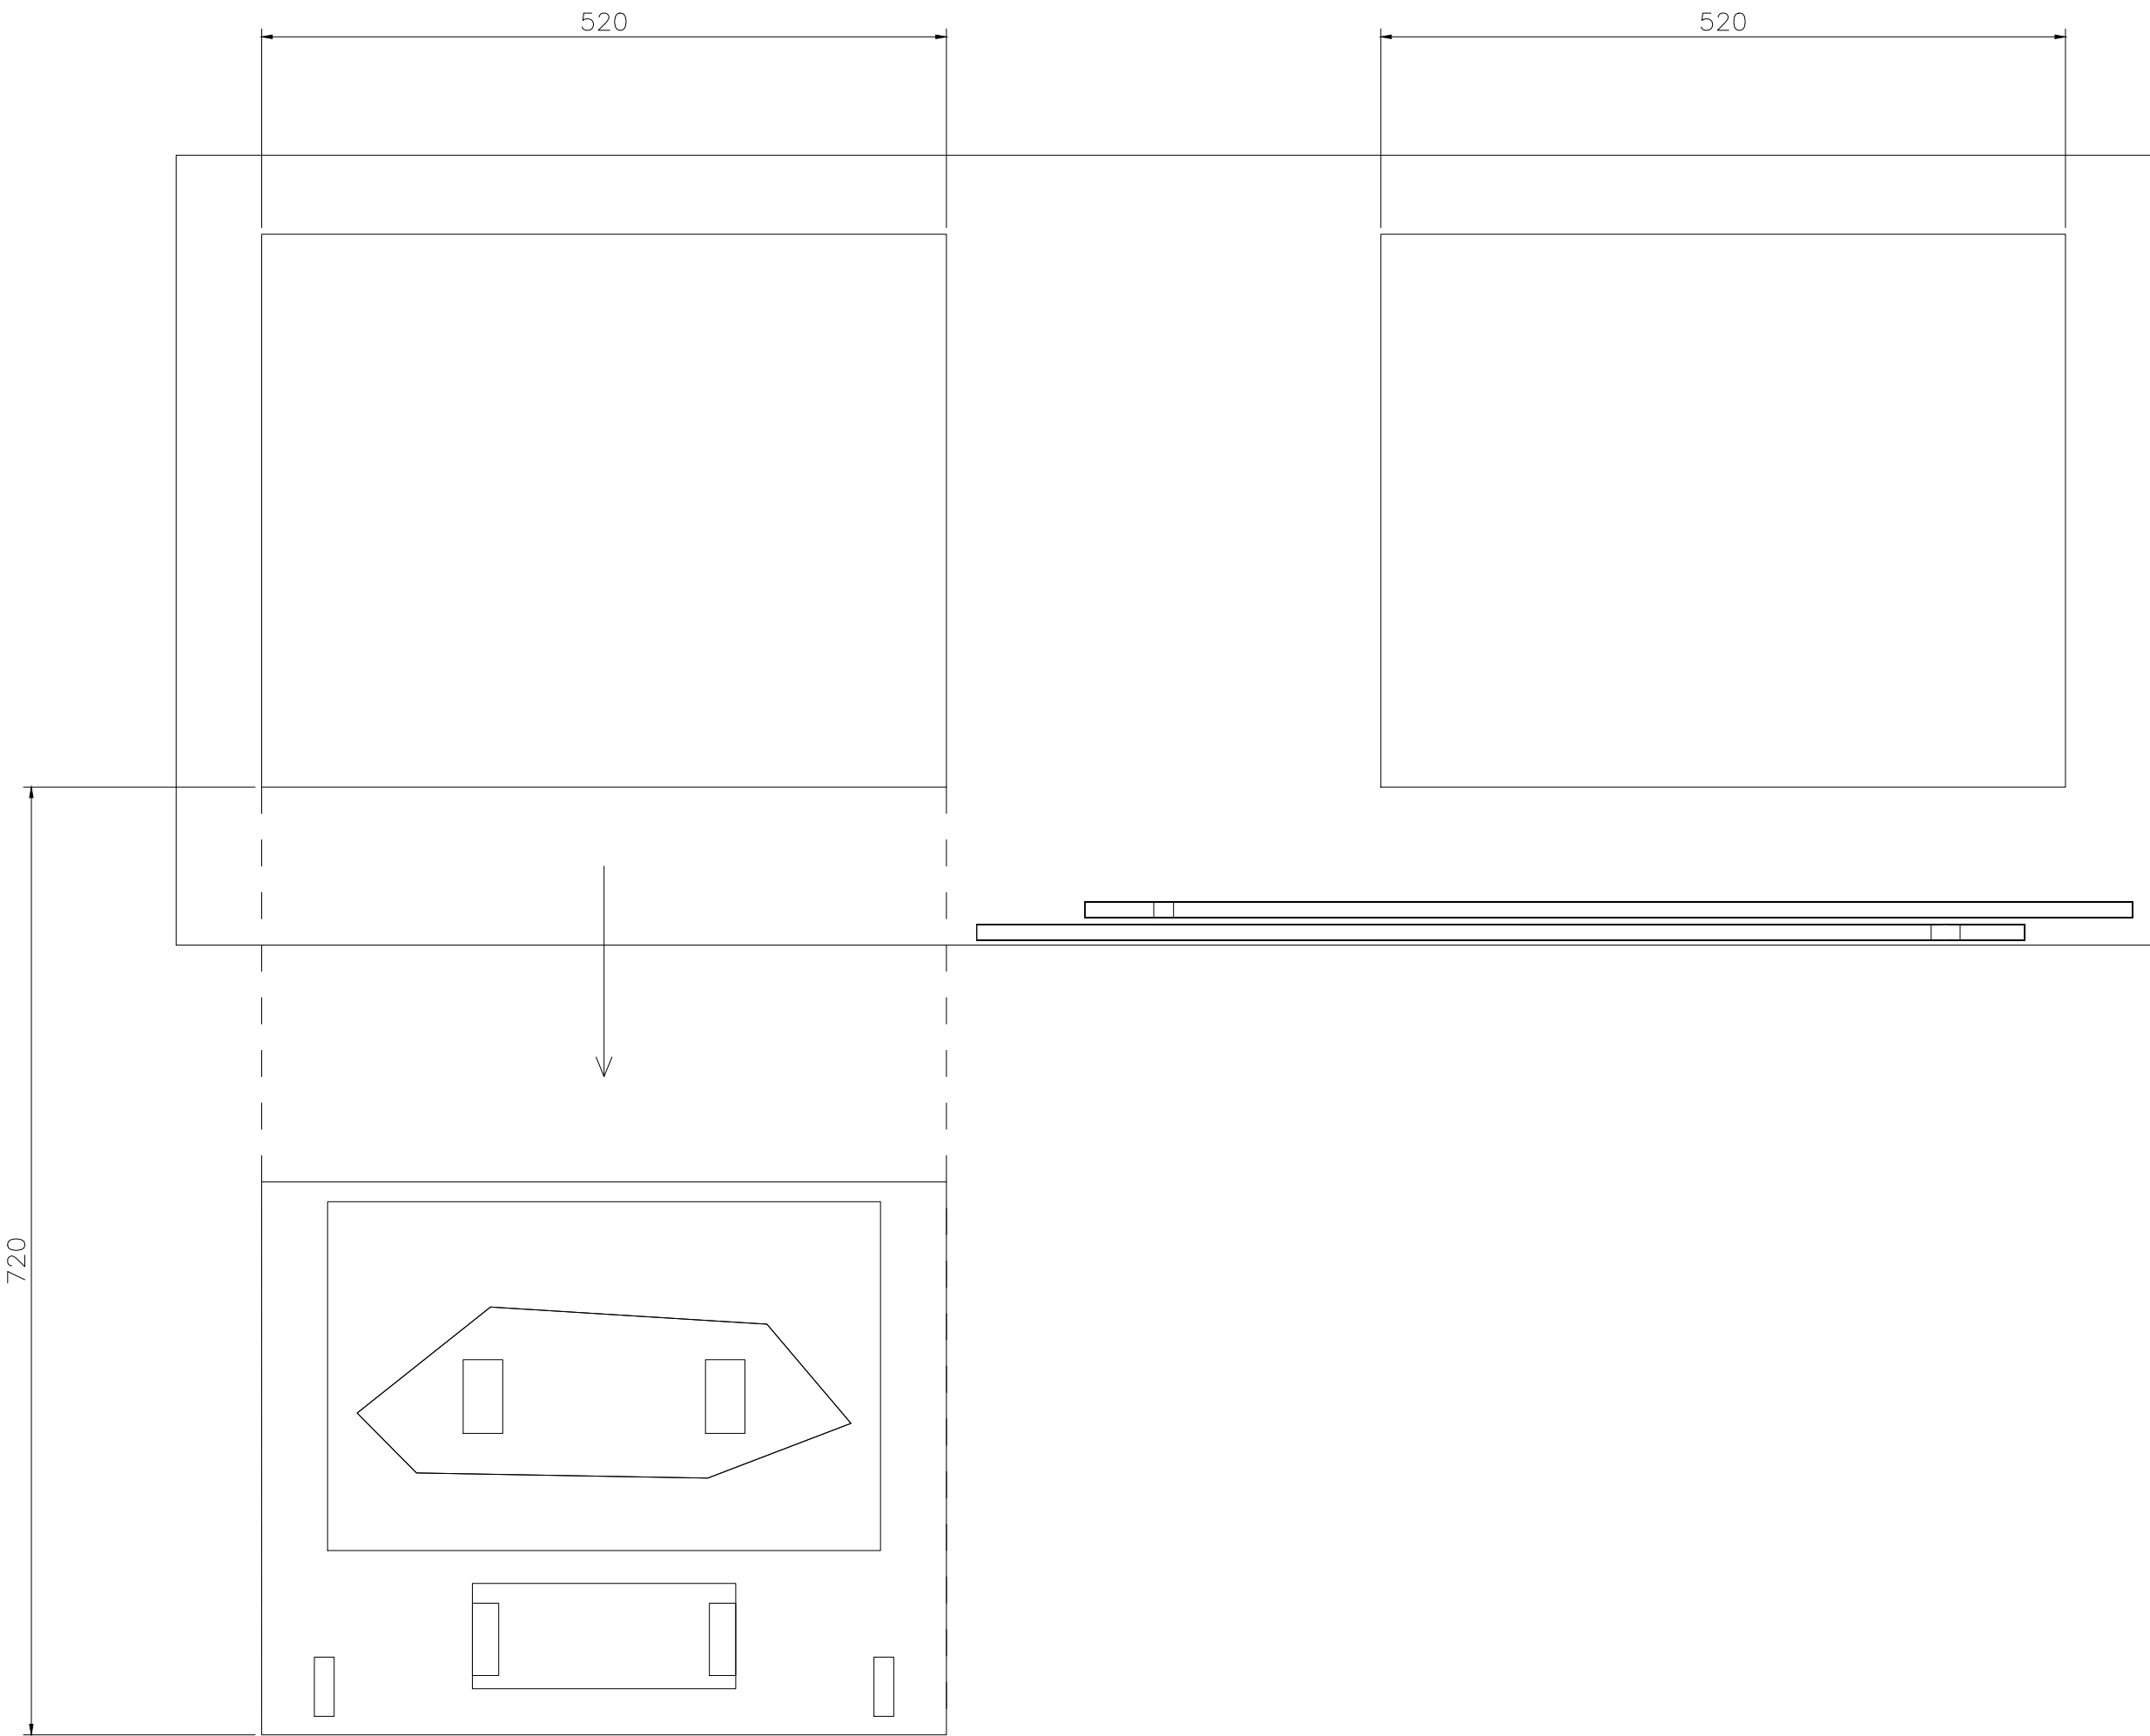


托盘位置：上提15后，向前720；末端完全离开前突锁面。

左开口X=14—608；托盘X=65—585，侧余量51/23。
右开口X=892—1486；右托盘X=915—1435，侧余量23/51。

操作：闭馆 → 解锁对应门 → 单扇滑到限位 → 托持上提/移出 → 放到工作台 → 按反复位后关门上锁。
本页不表示实际玻璃拆卸路径；拆门、锁具及防抬挡块维护仍见03/04并依产品条件深化。

02 x=325剖面 / 真实剖切

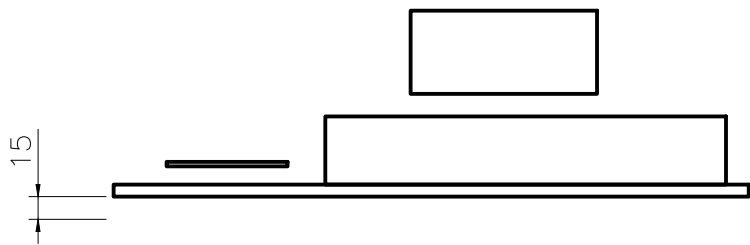


移动托盘底822，高于下轨壁顶818；几何余量4。
图示在左开口x=325取放，不能穿过仍关闭的右门。

路径核验


五柜共十组托盘。
每组先上提15，
再前移720。
两段连续包络均检查。

新件与门扇扫掠
无未解决几何冲突。
实际重量、抓握、
限位与实体操作
仍需样柜核对。

 


柜内灯体与可换展签 / 1:2 局部

真实毫米剖切；产品与供电条件未定型。本图表达位置、体量和接触关系。

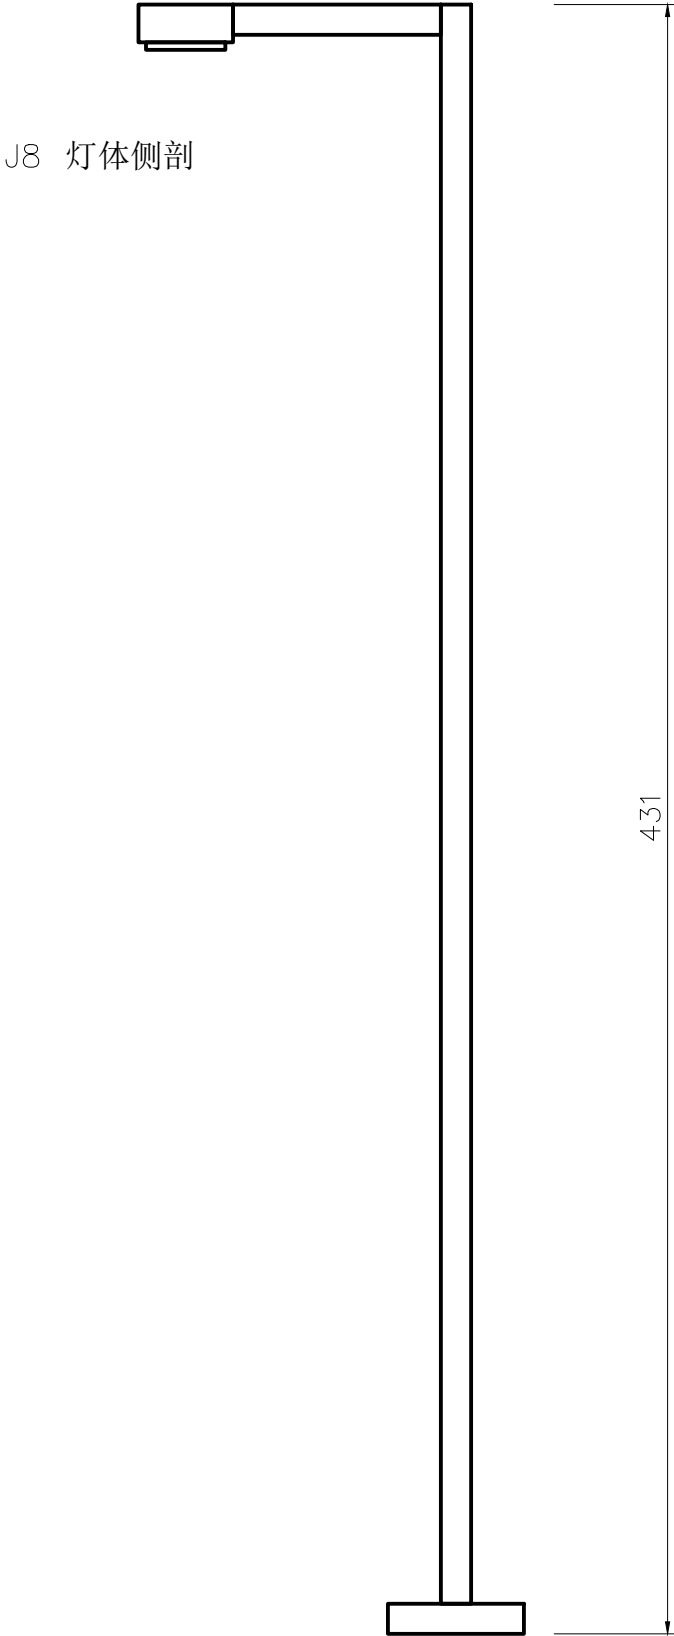


灯头120×25×10，顶1238。
发光面112×21×2，底1226。
支臂8×55×8，与后杆接触。
后杆8×8，顶1238。
底座70×36×8，底807。

后杆为内部低压线的设计占位；当前未确定供电进入柜体的方式。
实际驱动、接口、线径、维护可达性和温升需在产品定型后深化。
设备电功率与照度须按实际产品核定。

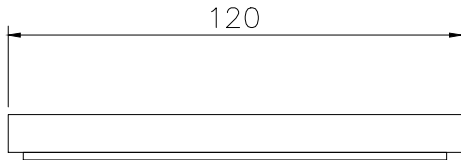

J9 灯头前视：板厚、散热和连接仅占位。

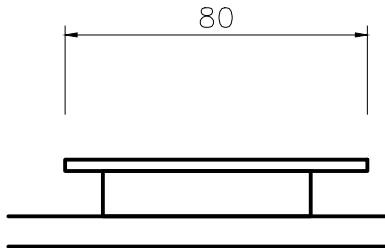



J10 展签侧剖 / x=235。
200×80×3面片，下设两支脚。
面片顶830；托盘顶815。
图文见柜内展签分册。

灯座后侧Y=582，距后玻璃内面588留6；托盘后缘540，
至灯座前缘546留6。该间距为几何核对，非通用安全值。
正式产品与展品确定后复核线缆、散热、保护和玻璃反射。

五柜与独立图文架 / 平面及正面位置关系

局部坐标mm；各柜正面统一朝图下方。EX12局部宽度指向南，深度指向东。平面不表示完整通行净宽。
EX01 / 正面朝南

平面 / 柜身外包与图文架

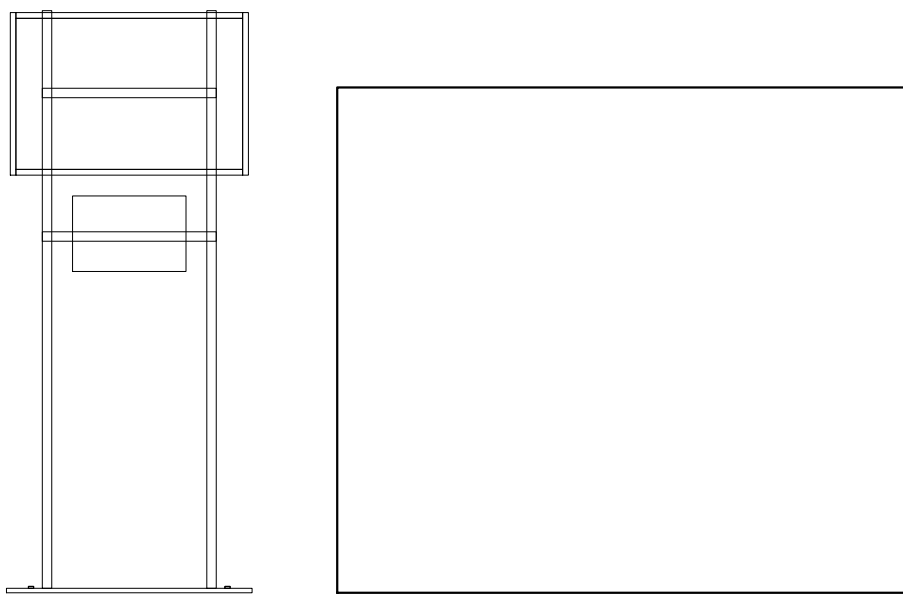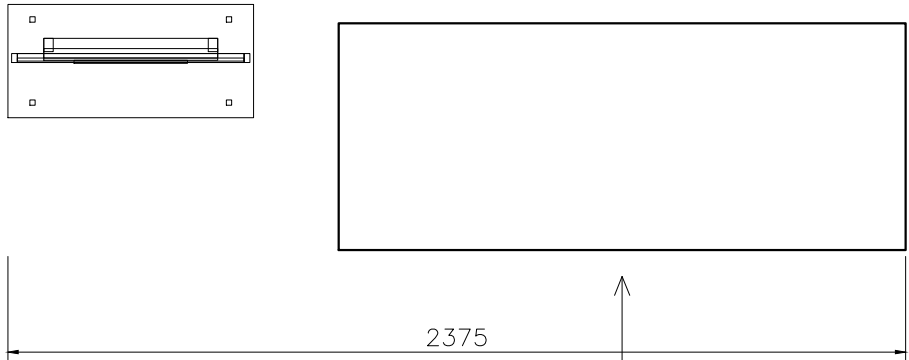

柜身局部原点：X=7950，Y=8200

图文架外包：650×300×1540

全馆X：7075—7725



全馆Y：8550—8850

柜身+图文架局部总宽：2375

图文与编号牌见展陈分册；架体单独落地。

EX07 / 正面朝南

平面 / 柜身外包与图文架

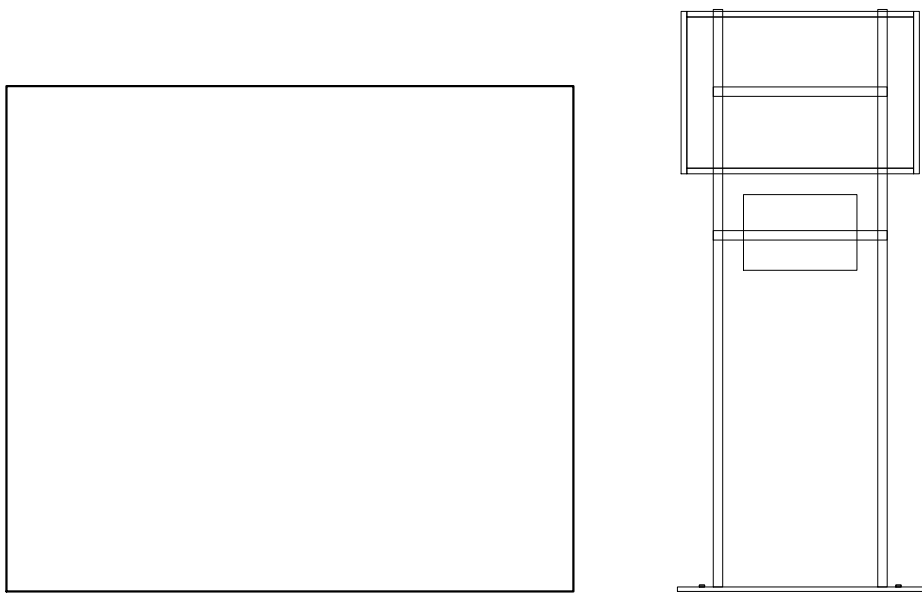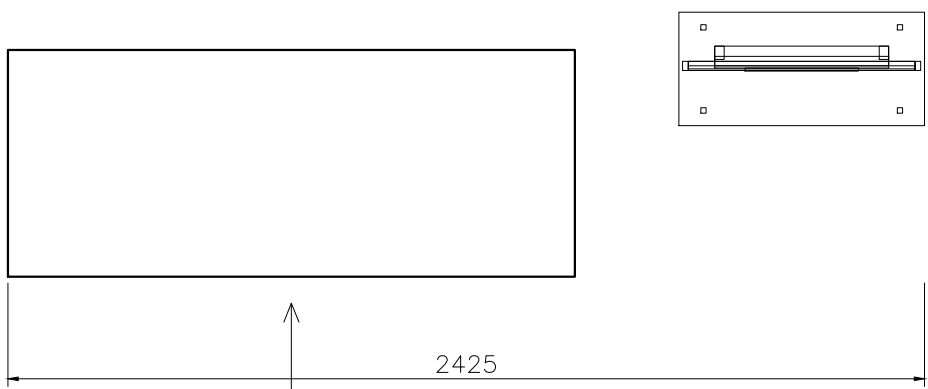

柜身局部原点：X=2000，Y=19000

图文架外包：650×300×1540

全馆X：3775—4425



全馆Y：19400—19700

柜身+图文架局部总宽：2425

图文与编号牌见展陈分册；架体单独落地。

EX08 / 正面朝南

平面 / 柜身外包与图文架

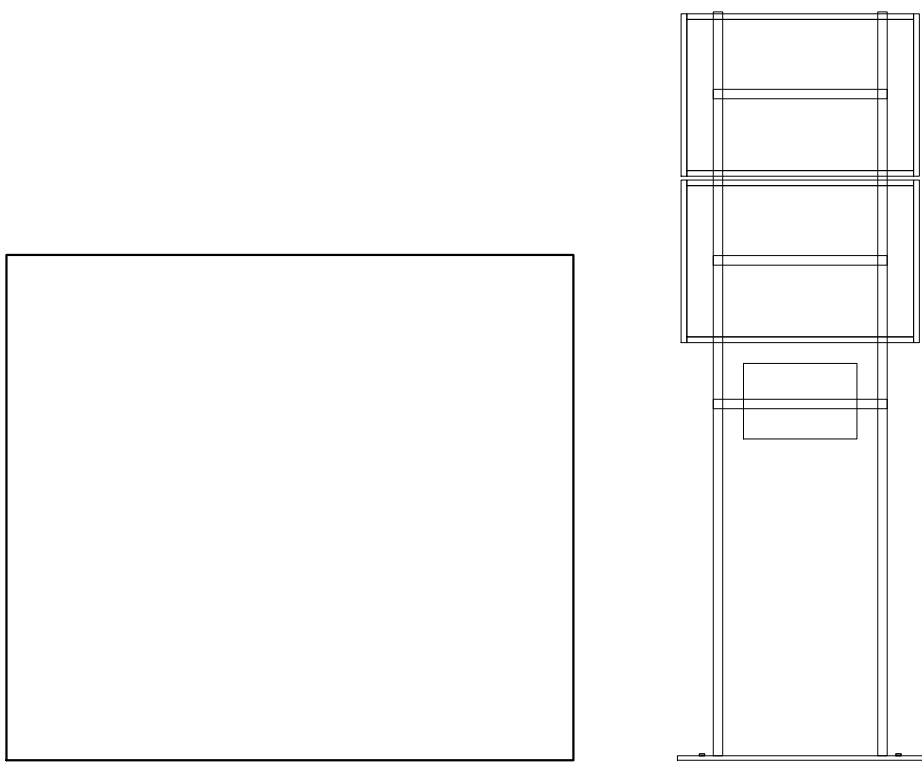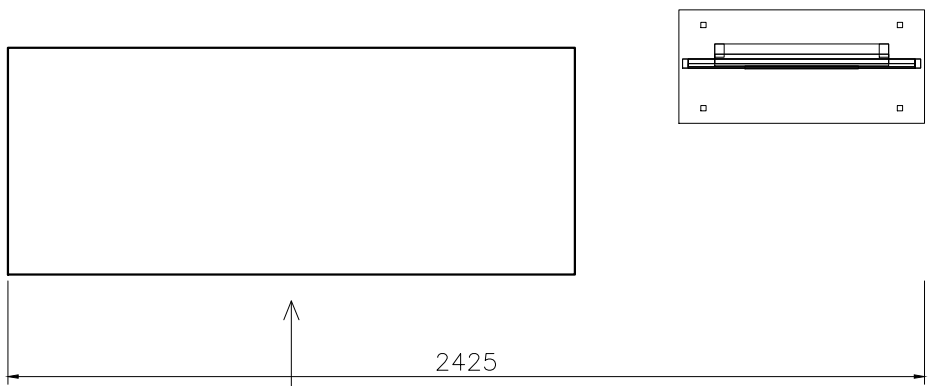

柜身局部原点：X=2000，Y=22000

图文架外包：650×300×1980

全馆X：3775—4425



全馆Y：22400—22700

柜身+图文架局部总宽：2425

图文与编号牌见展陈分册；架体单独落地。

EX10 / 正面朝南

平面 / 柜身外包与图文架

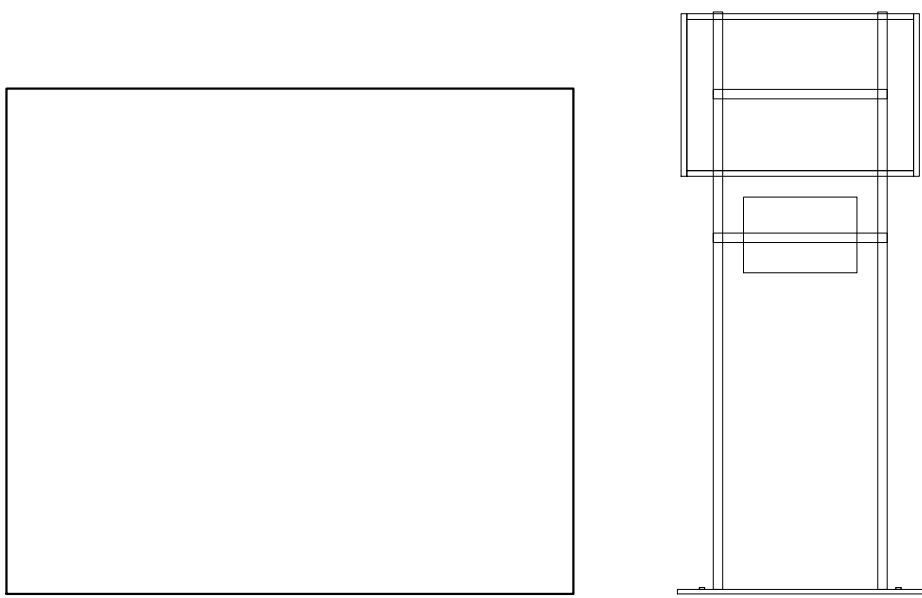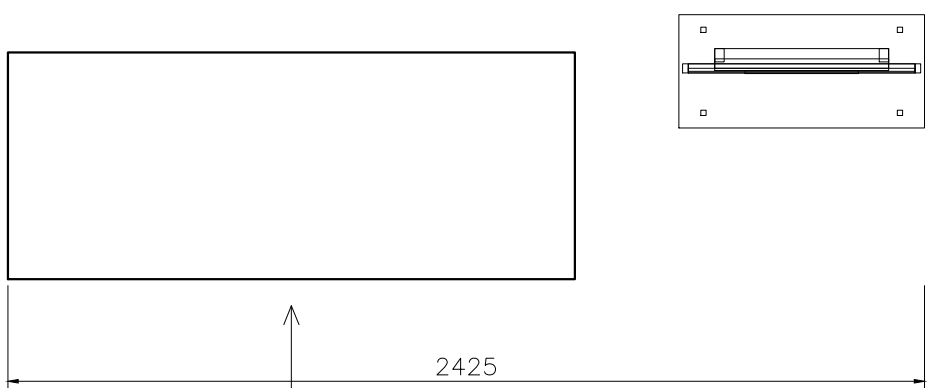

柜身局部原点：X=6000，Y=26000

图文架外包：650×300×1540

全馆X：7775—8425



全馆Y：26400—26700

柜身+图文架局部总宽：2425

图文与编号牌见展陈分册；架体单独落地。

EX12 / 正面朝西

平面 / 柜身外包与图文架

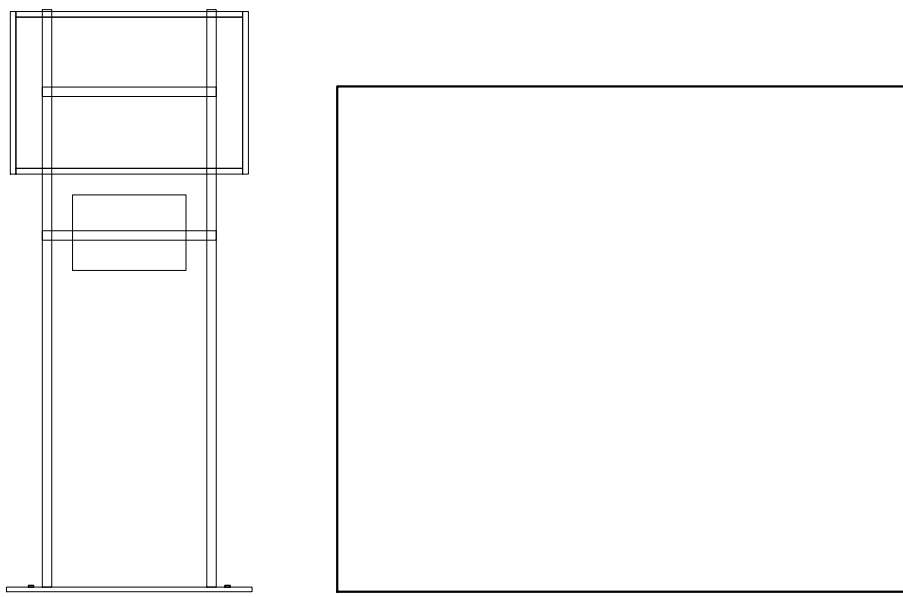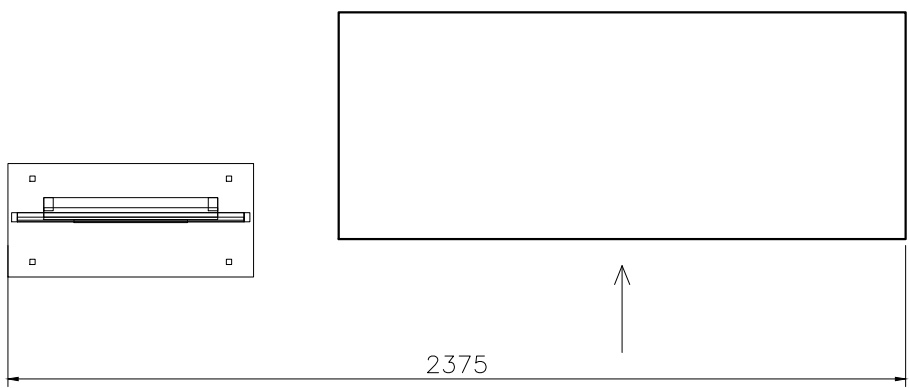

柜身局部原点：X=28500，Y=24550

图文架外包：300×650×1540

全馆X：28400—28700

全馆Y：24775—25425

柜身+图文架局部总宽：2375

图文与编号牌见展陈分册；架体单独落地。