


从空间分层，到微缩装配

建筑、展具与模型制作 / 1:100数字制作准备

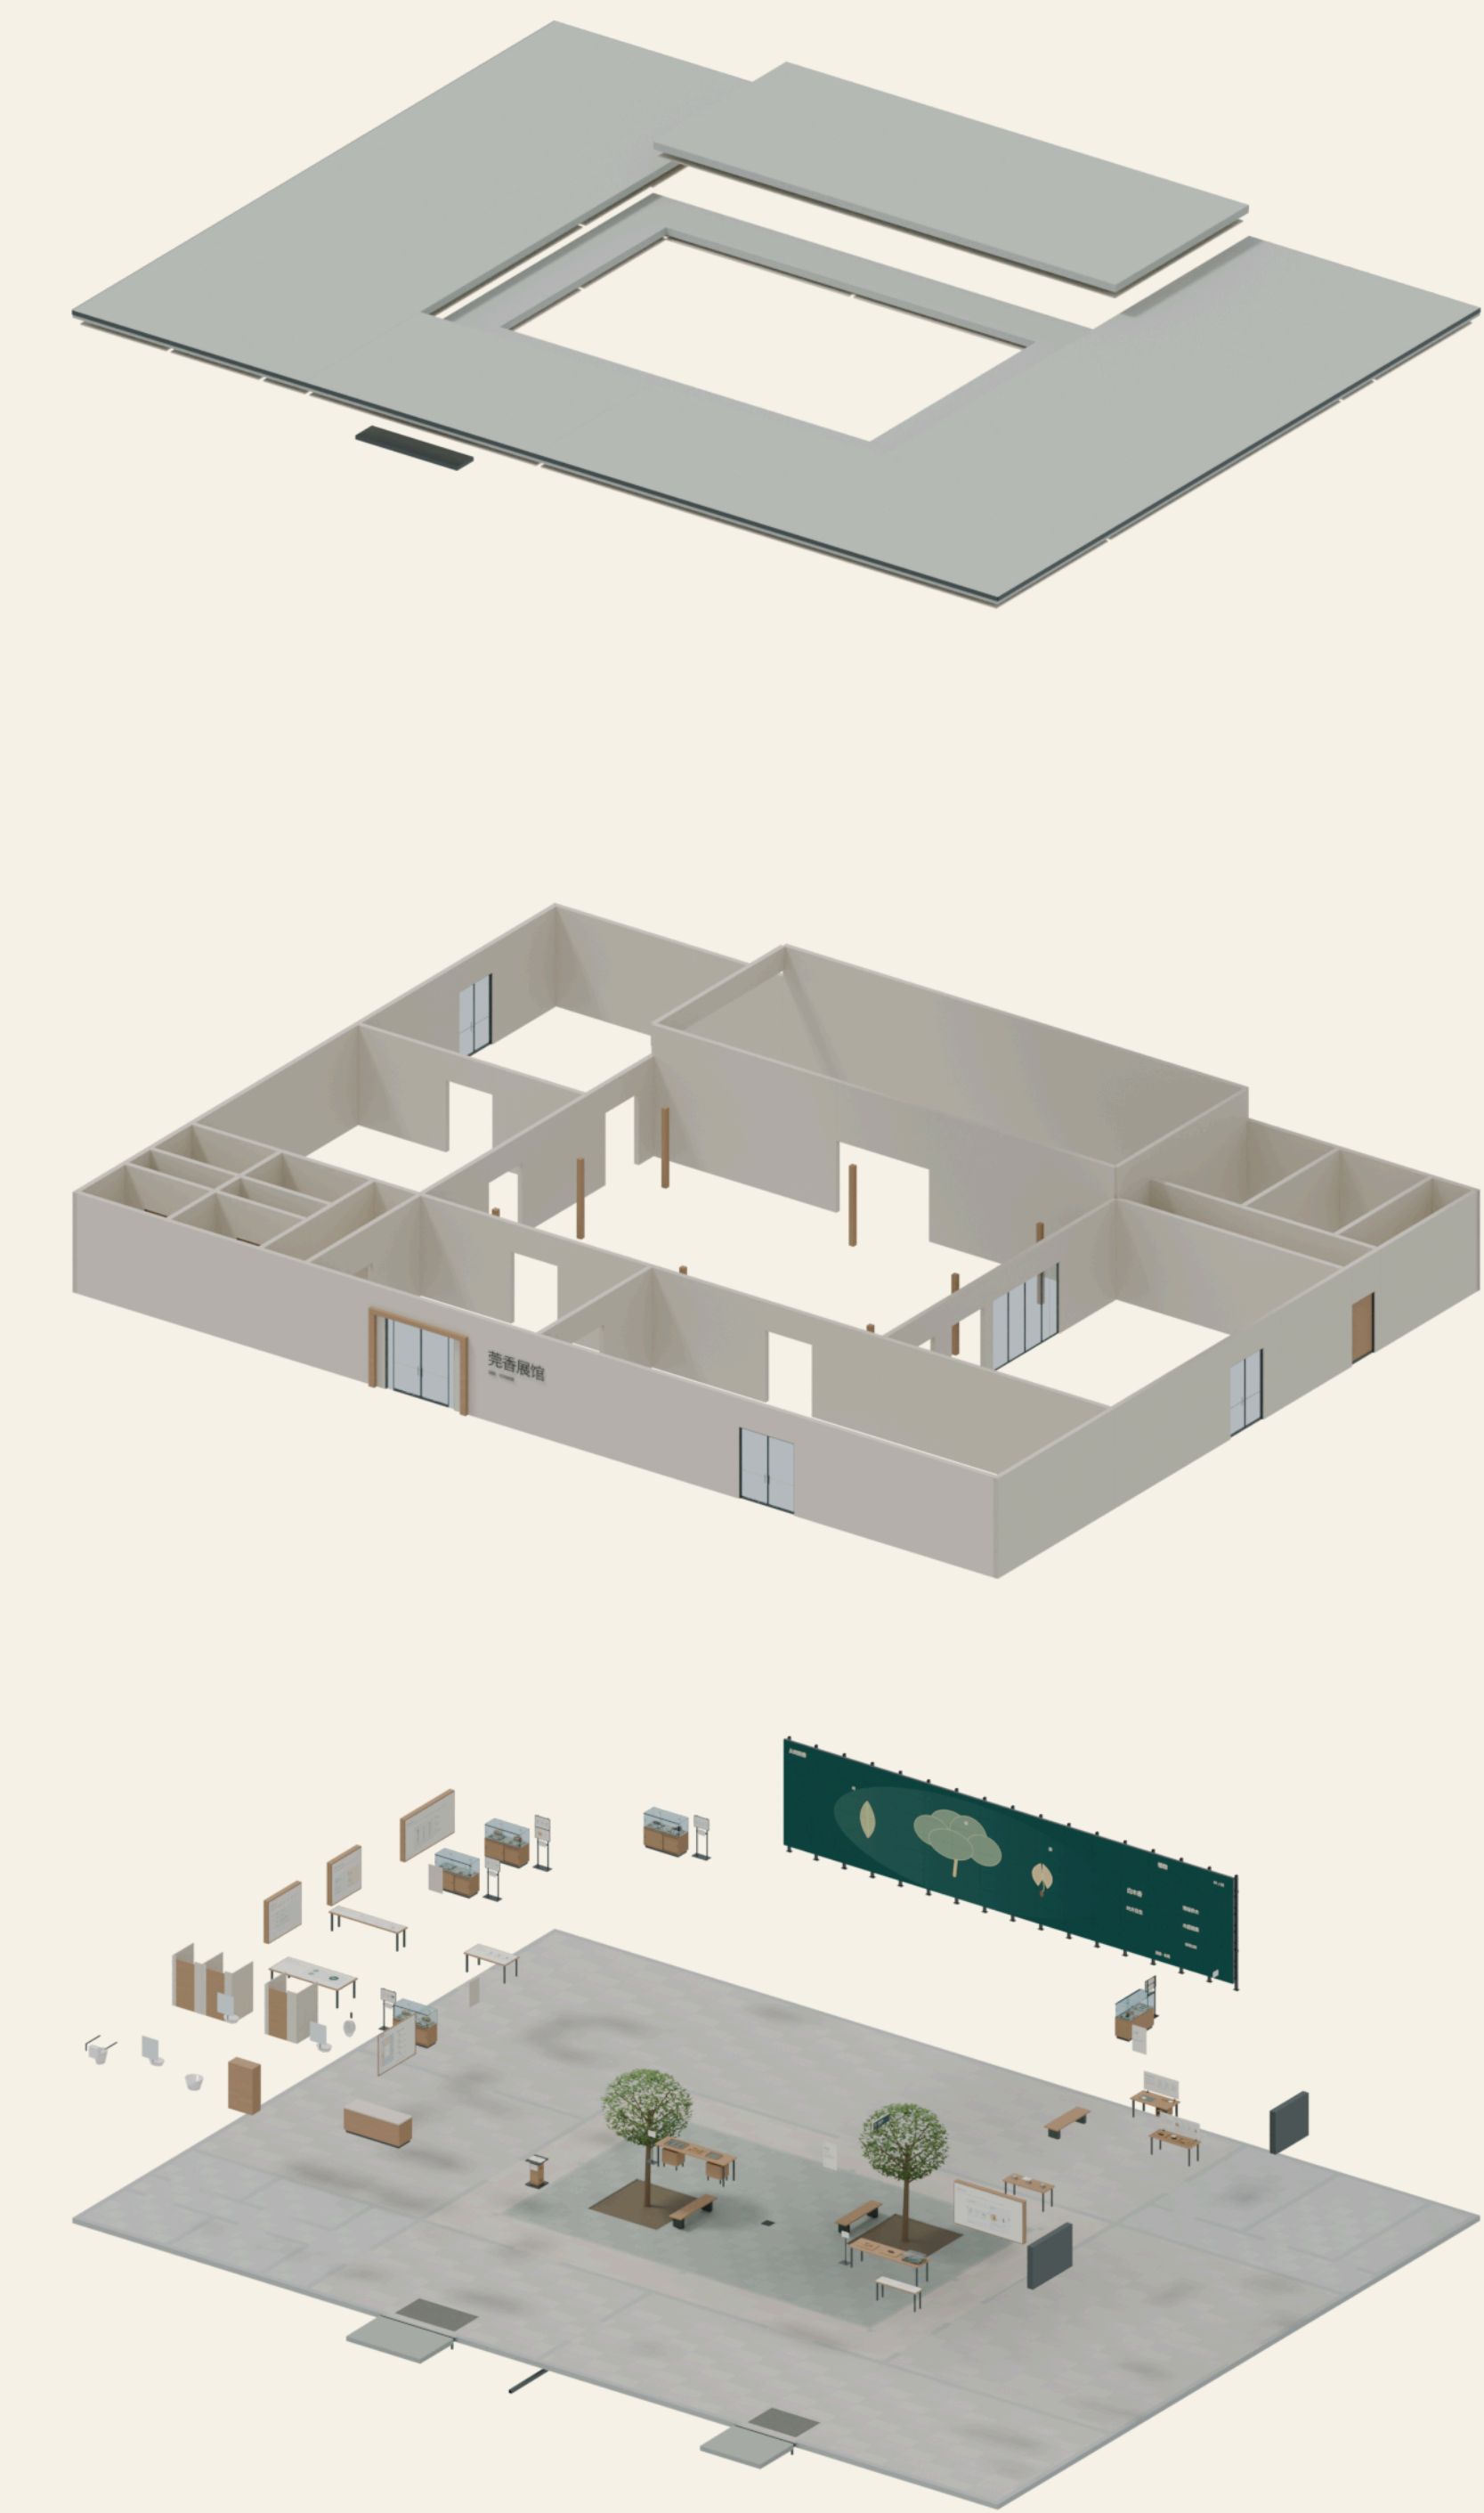

建筑分层

屋面、围护、展陈与地坪分层表达。
图示为展开距离，不代表实际层高。

八类展具组件




C01 比较与记录台




C02 透明展柜




C03 壁面展板

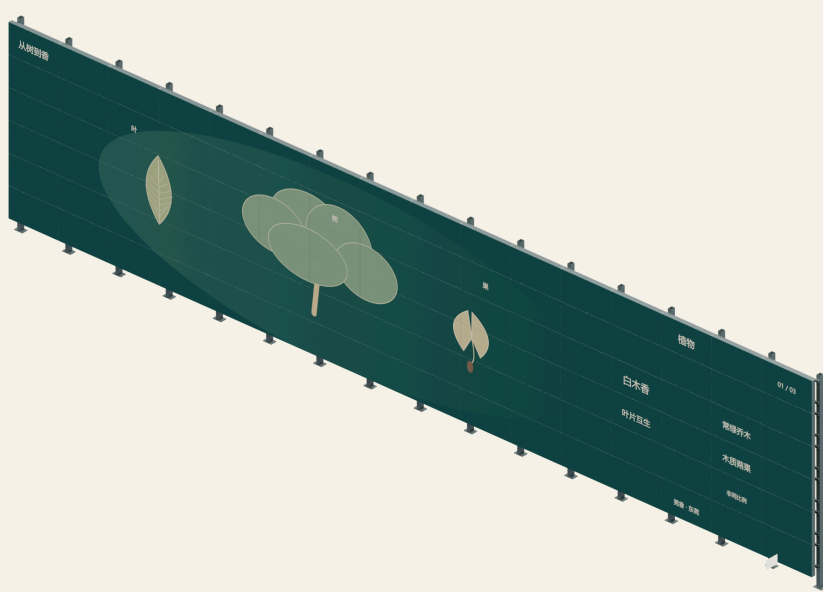


C04 整墙影像

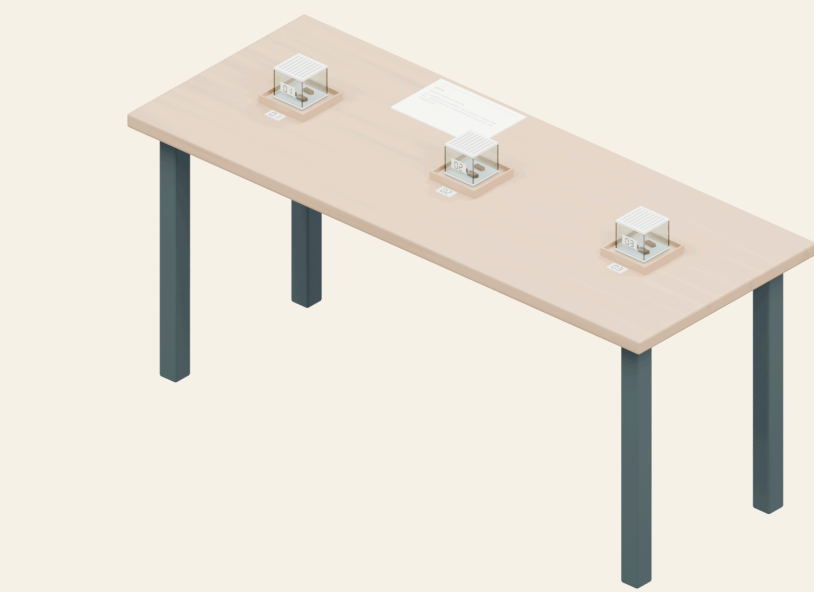


C05 闻香台

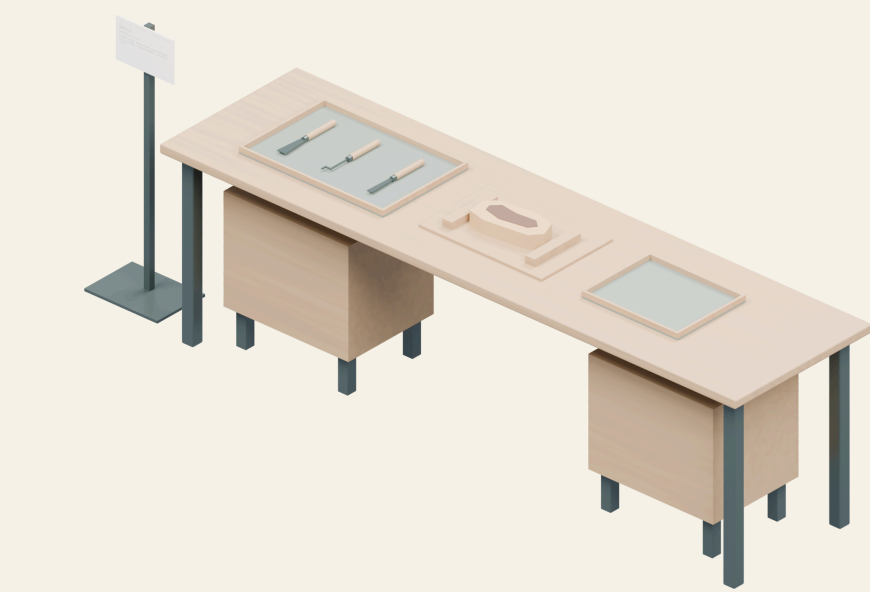

C06 手工艺示范台

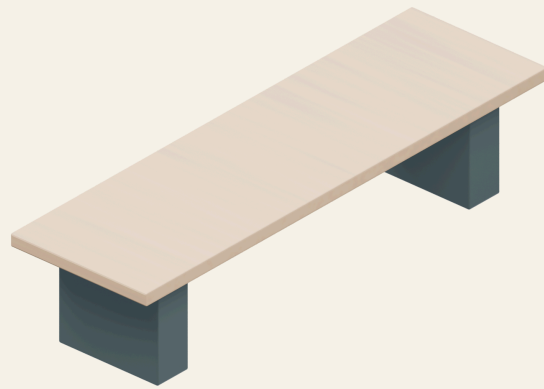

C07 休憩座椅

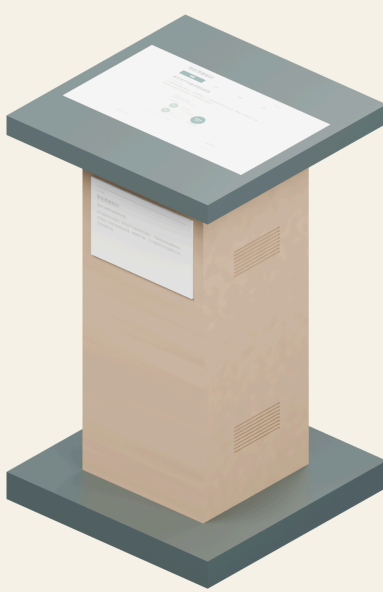


C08 知识终端


板材承担底板、墙片和屋面，打印件用于家具及细部。
实际板厚、切缝、壁厚与插接公差需结合店家工艺和实体试件确定。



600×400mm底板 / 可拆屋顶

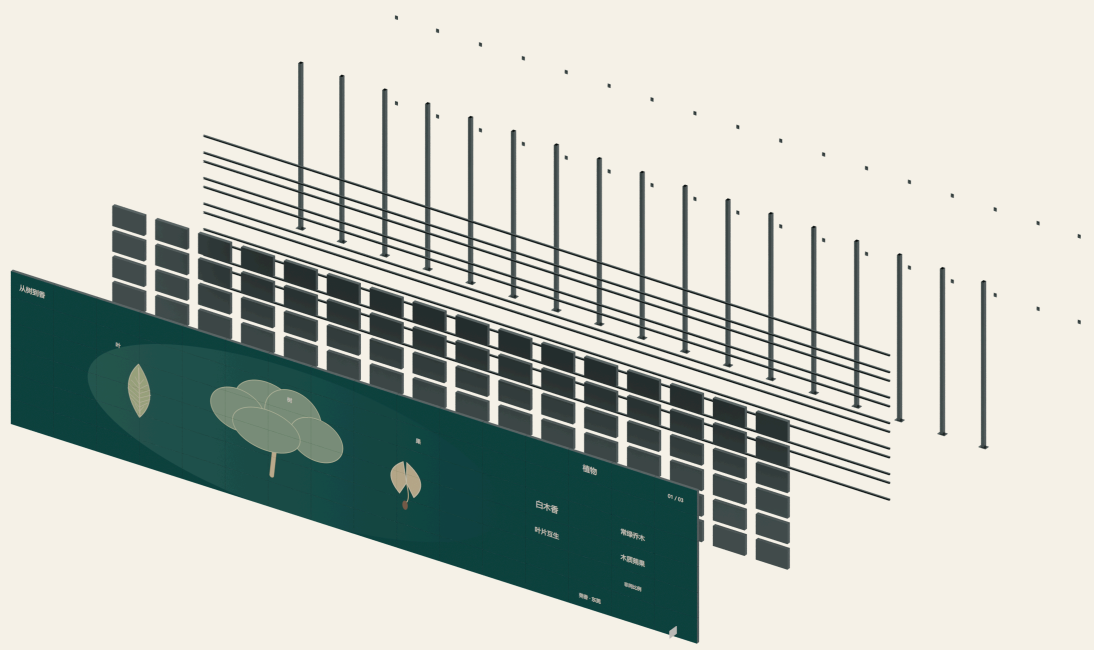

液晶墙：屏幕、框架与导轨分层

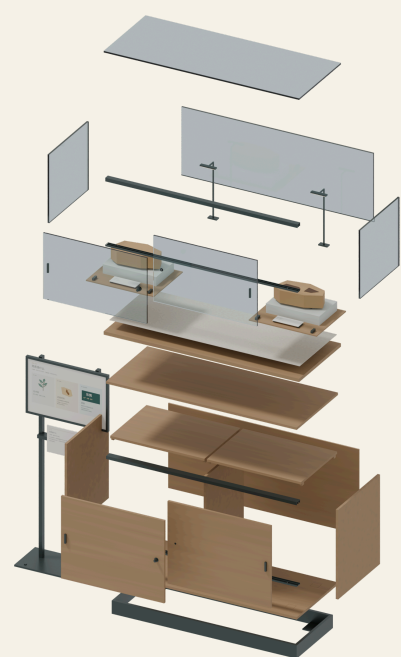

典型展柜：罩体、陈设、柜体与底座