
寻香厅 · 平面布置

弧墙圆景 / 主陈列墙 / 6席互动长台 / 一主三辅展位　　A3原幅比例 1:60

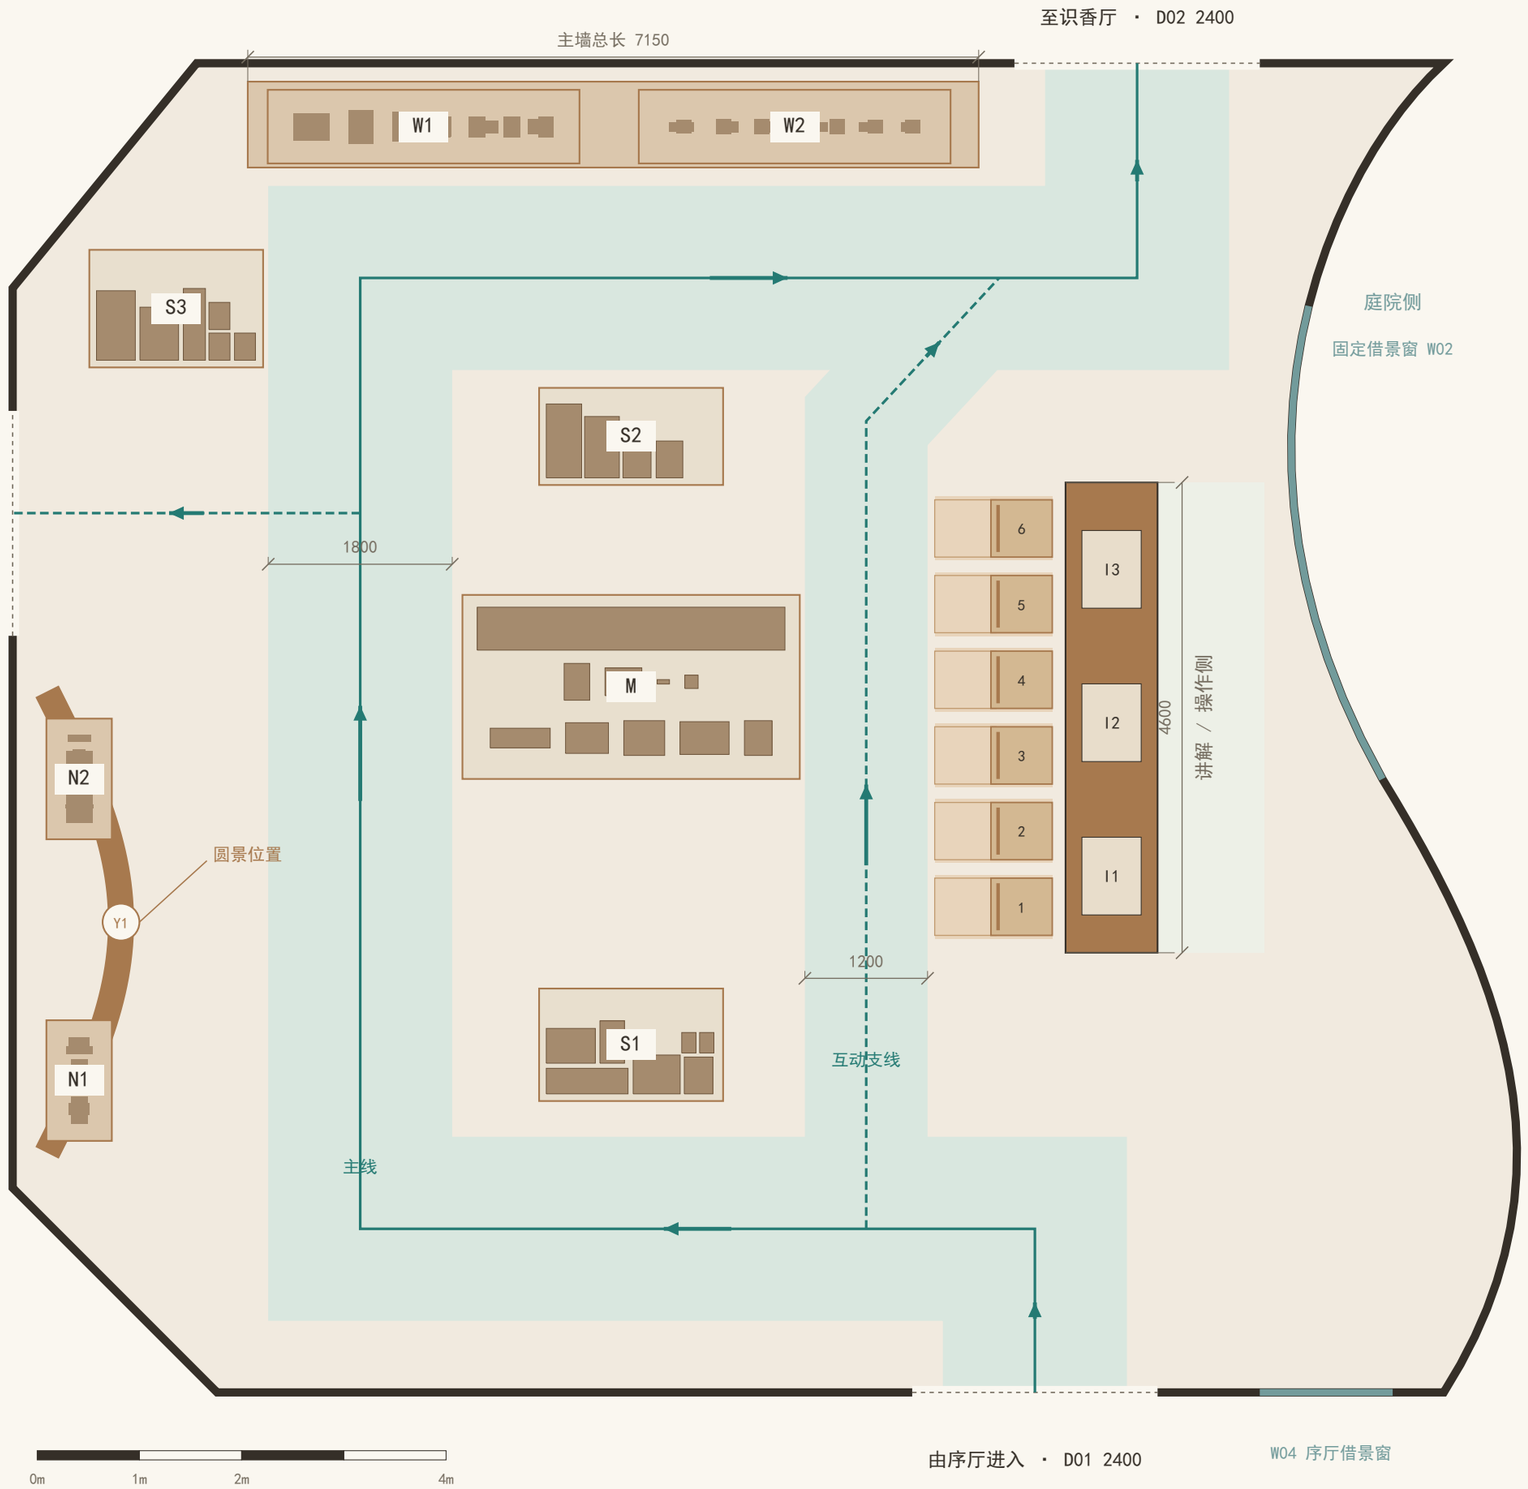

布局与陈列

W1+W2　一面主陈列墙

长7.15m，柜深0.72m；26件或组。
香市交易与运输贸易连续组织。

Y1+N1+N2　弧墙圆景

圆形景框为竖向立面，直径1.80m。
前后两处嵌龛，共12件或组。

M　香市重点主台

3.30 × 1.80m；10件或组。
保留原尺寸3.01m街铺解释模型。

S1 / S2 / S3　三个辅助展位

S1 香农：1800×1100，8组。
S2 陆运：1800×950，4组。
S3 水运：1700×1150，6组。

T　六席互动长台

4.60 × 0.90m，高0.75m。
六席朝向讲解侧，椅后另留支线。

通行与使用

实线：1.80m主参观通路。
虚线：1.20m互动及对外开口连接。
浅棕范围：座椅使用与0.55m拉出。
浅绿范围：讲解侧1.04m操作区。

保留与调整

保留外轮廓、门洞、借景窗和地面。
寻香66组原有拟展品全部有新定位。
三组互动托盘另册登记。
原传香8席、咖啡8桌16席延续。


本图为二维方案，三维仍为r24。
尺寸单位：mm；细部与使用关系待深化。

寻香厅 · 坐席与墙柜关系

左：互动区放大平面 1:30　　右：墙柜与圆景示意　　本页配合总平面审核


6席单侧排列 · 座位中心间距740

浅棕：椅子使用范围；虚框：局部木格天花投影

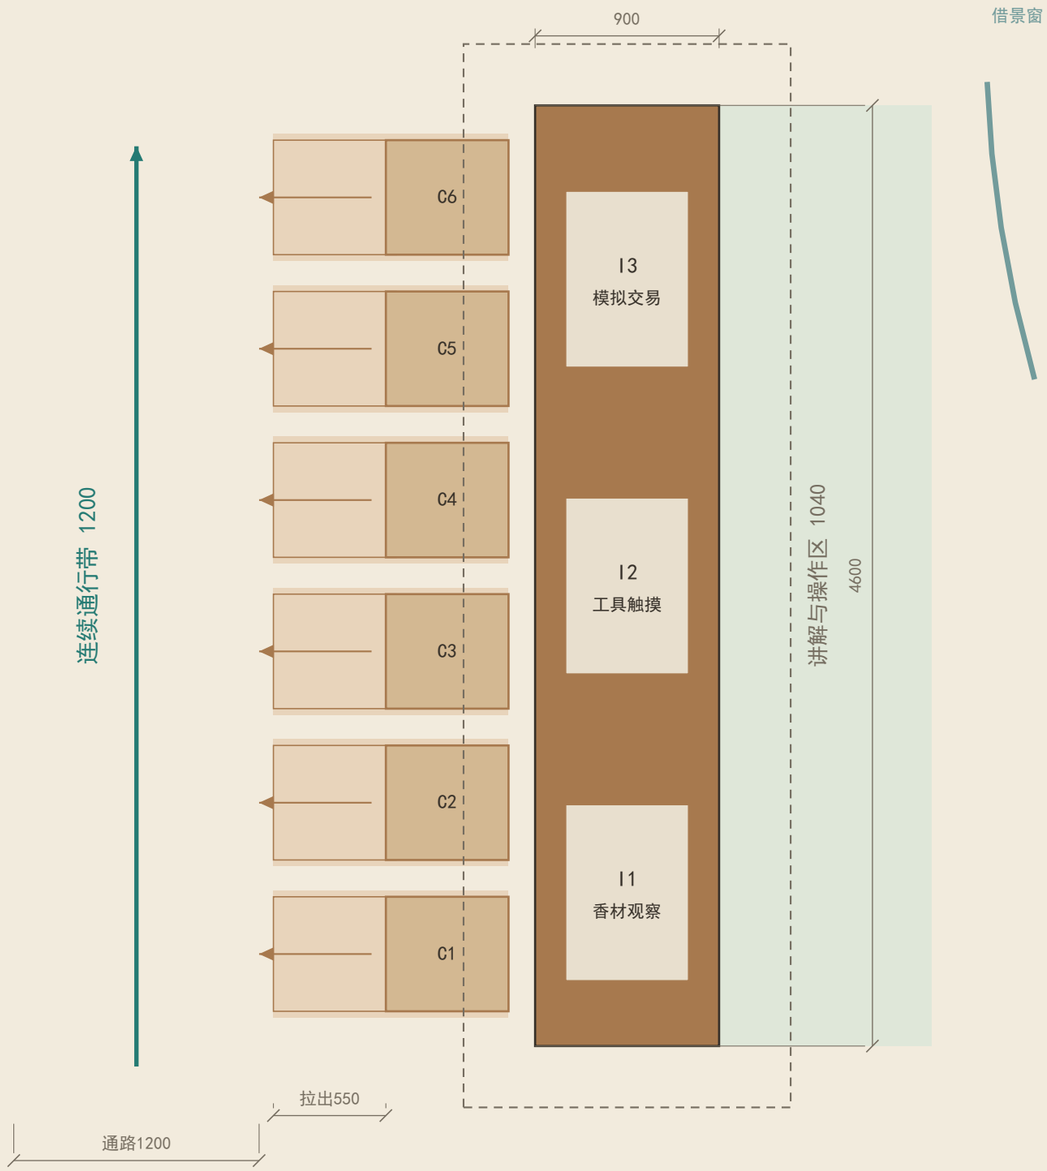

台高750；观众侧留膝部空间，储藏向讲解侧及端部组织。


主陈列墙 · 连续框架与不同展示窗

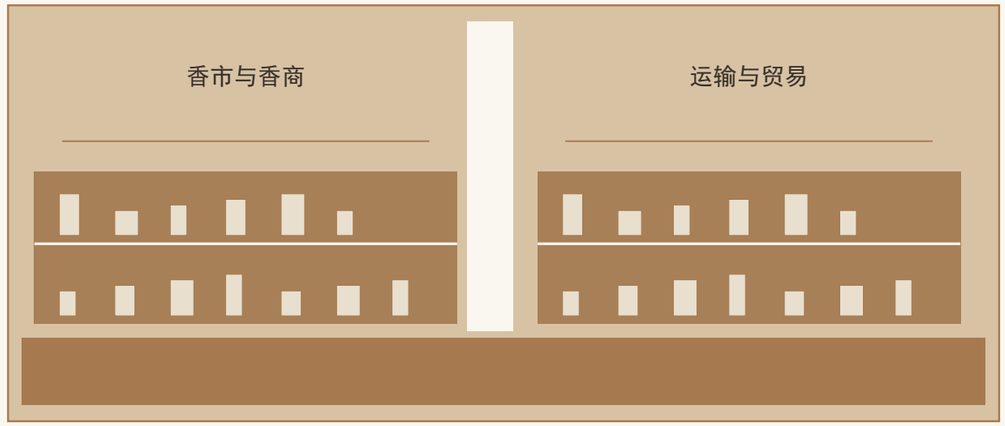

整体宽7150；柜深720。图景、柜窗与下部储藏一体收口。

中棕木作配米灰浅砂墙面，陈列格随内容变化。

弧墙圆景 · 正面展开示意

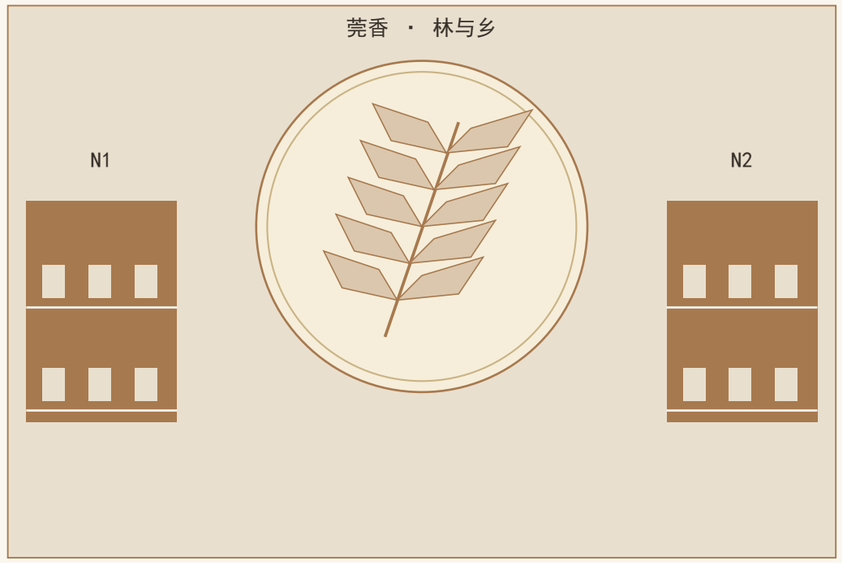

圆景直径1800，封闭背板与柔和环光；侧龛共12组。

立面为设计关系示意，具体细部将在平面确认后建模。