


围合与开放，形成参观秩序

平面、剖面与四向立面 / 标注单位：毫米；标高单位：米


全馆家具与展陈平面 1:100

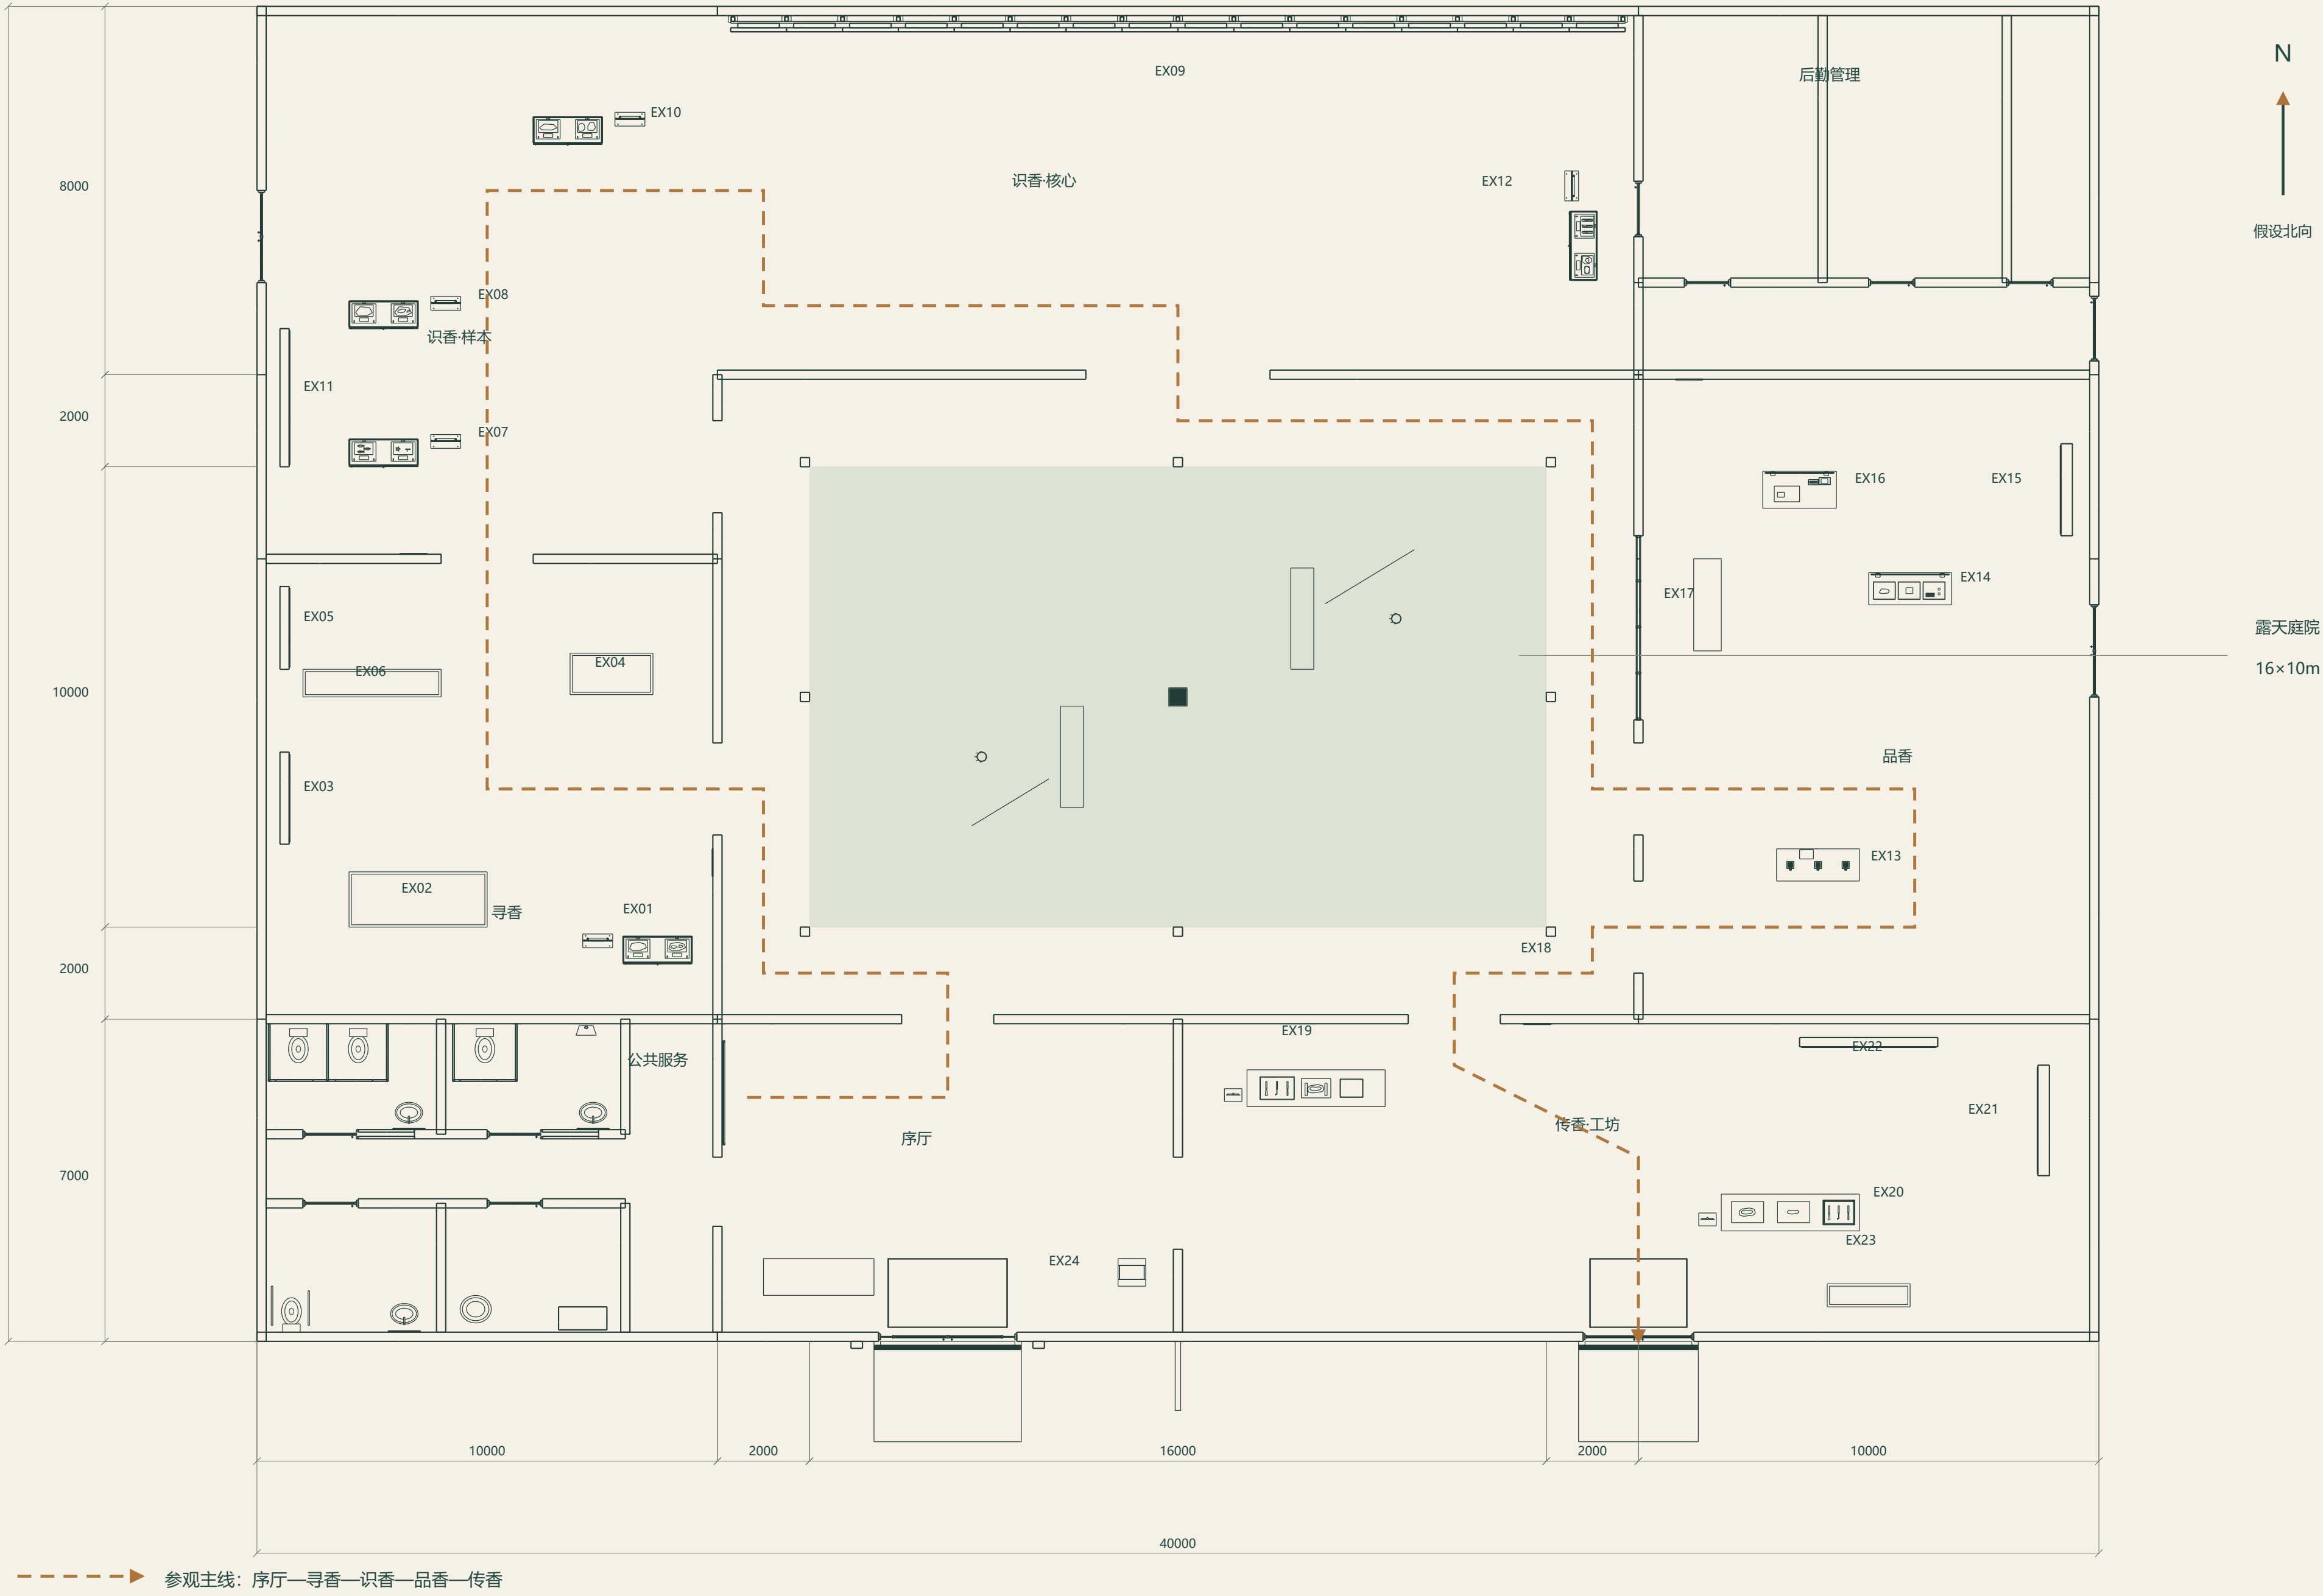


参观主线：序厅—寻香—识香—品香—传香

剖切索引：A—A沿x=15000向西看；B—B沿y=14000向北看。


A—A 南北剖面 / 向西看 1:100

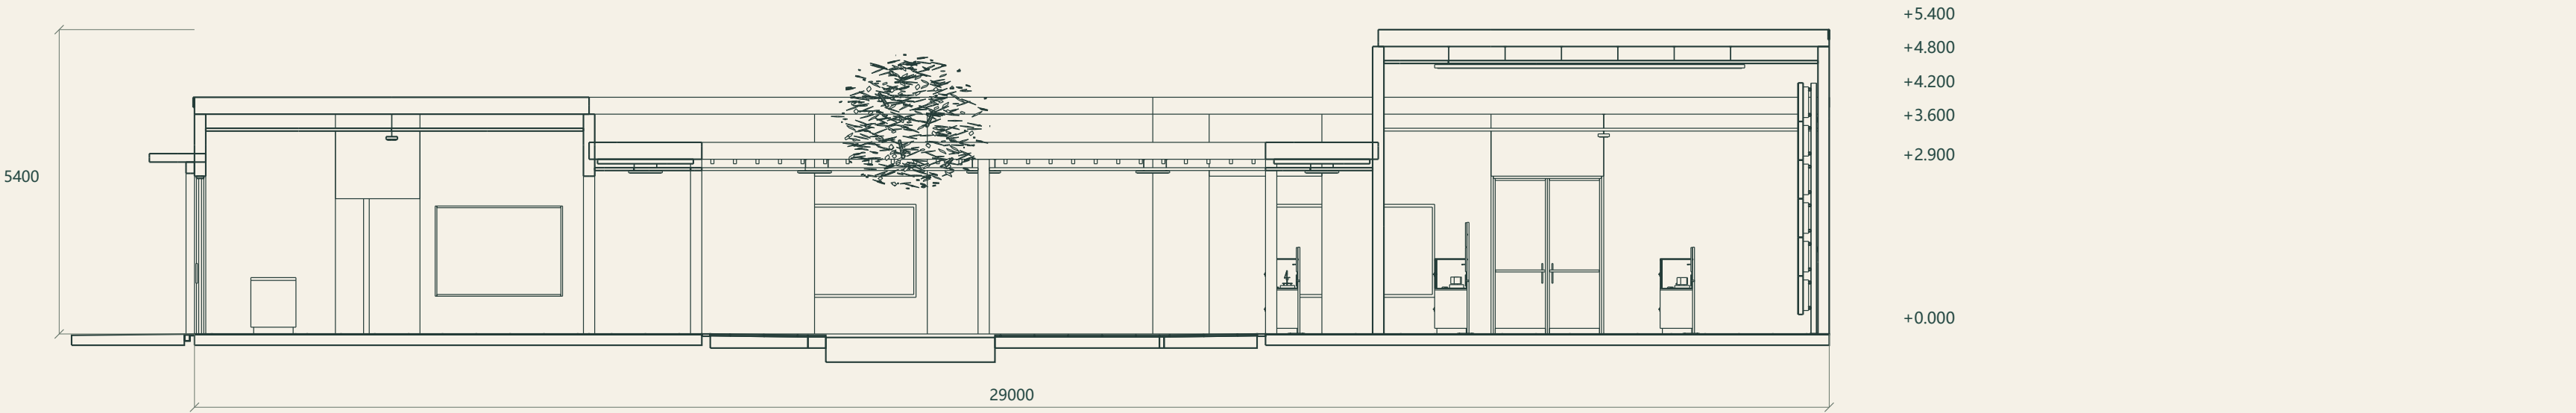


B—B 东西剖面 / 向北看 1:100

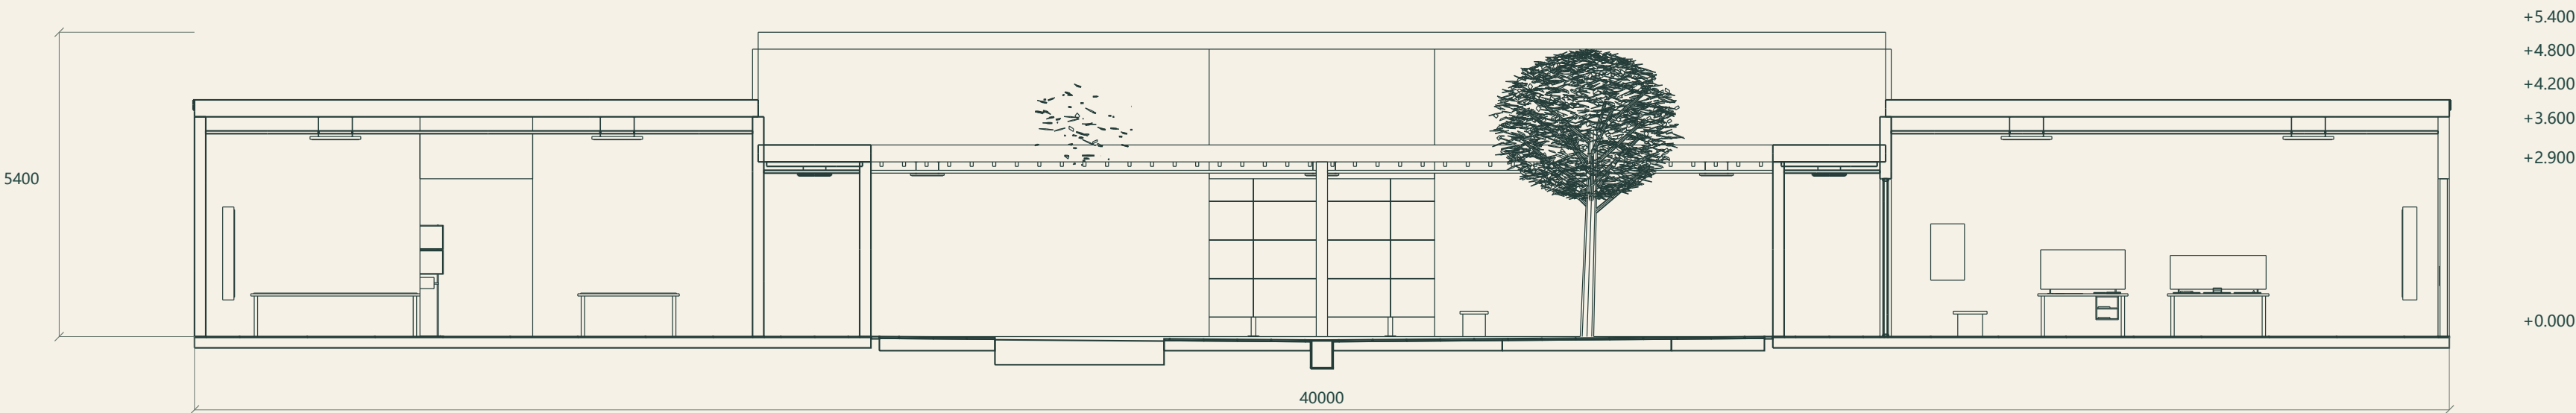


南立面 1:200

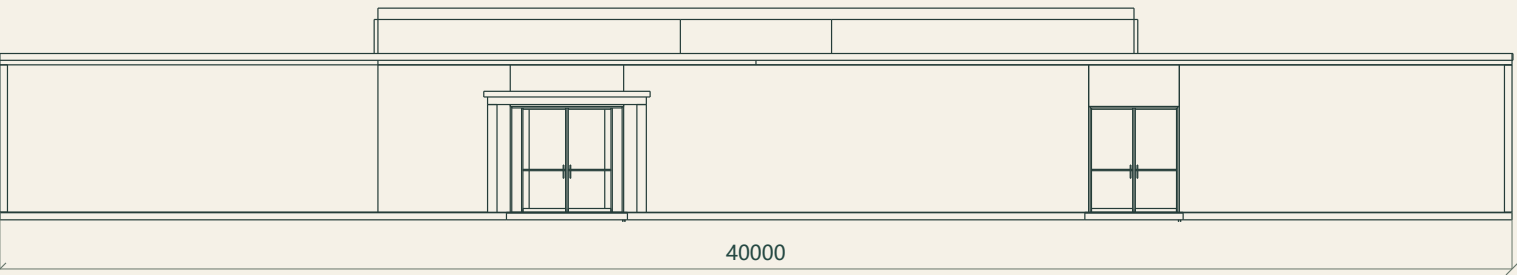

北立面 1:200

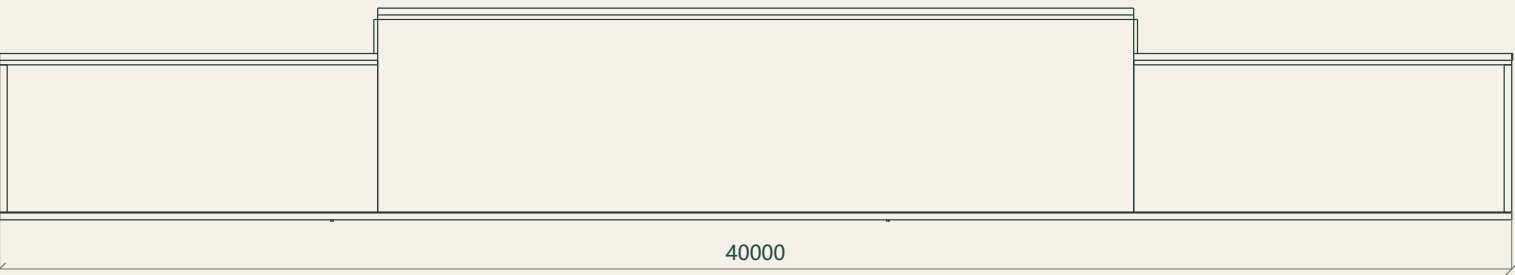

东立面 1:200

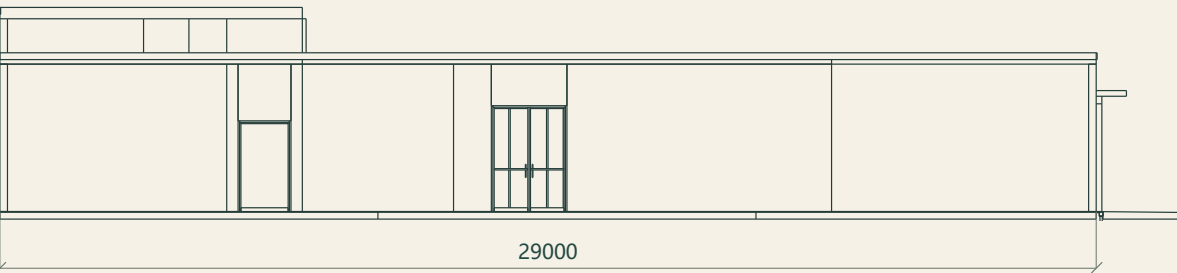

西立面 1:200

